

LOG OF BORING No. OW-23/5

PROJECT : MRT Orange Line Project Bang Khun Non -

LOCATION : Bangkok

Min Buri (Suwinthawong) Section Public - Private Partnership Contract

DEPTH, m.	SAMPLE No.	TYPE OF SAMPLE	SAMPLE DIST.	RECOVERY	DESCRIPTION OF MATERIAL	GRAPHIC LOG	Natural Water Content		Plastic Limit		Liquid Limit		Su (UC)		Su' (UC)		Su (FV)		Su' (FV)		Qp/2		Su (UU)	
							(%)	(%)	(%)	(%)	(t/m ²)	(t/m ²)	(t/m ²)	(t/m ²)	(t/m ²)	(t/m ²)	(t/m ²)	(t/m ²)						
0																								
					(A)	0.25 m.																		
					(B)	0.5 m.																		
5																								
10					(Wash out)																			
15																								
20	01	SS				19.5 m.																		
					(C)	20.5 m.																		
	02	SS			(D)	21.3 m.																		
					(E)	22.0 m.																		
	03	SS																						
	04	SS			Silty clay, trace fine sand, greyish brown, stiff to very stiff.																			
25																								
	05	SS																						



BORING STARTED : 08/03/25

RIG. ACKER

WL. -2.50 m 24 Hrs. After Boring

BORING FINISHED : 11/03/25

FOREMAN : WN.


JOB No. : 1168049

LOG OF BORING No. OW-23/5

PROJECT : MRT Orange Line Project Bang Khun Non -

LOCATION : Bangkok

Min Buri (Suwinthawong) Section Public - Private Partnership Contract

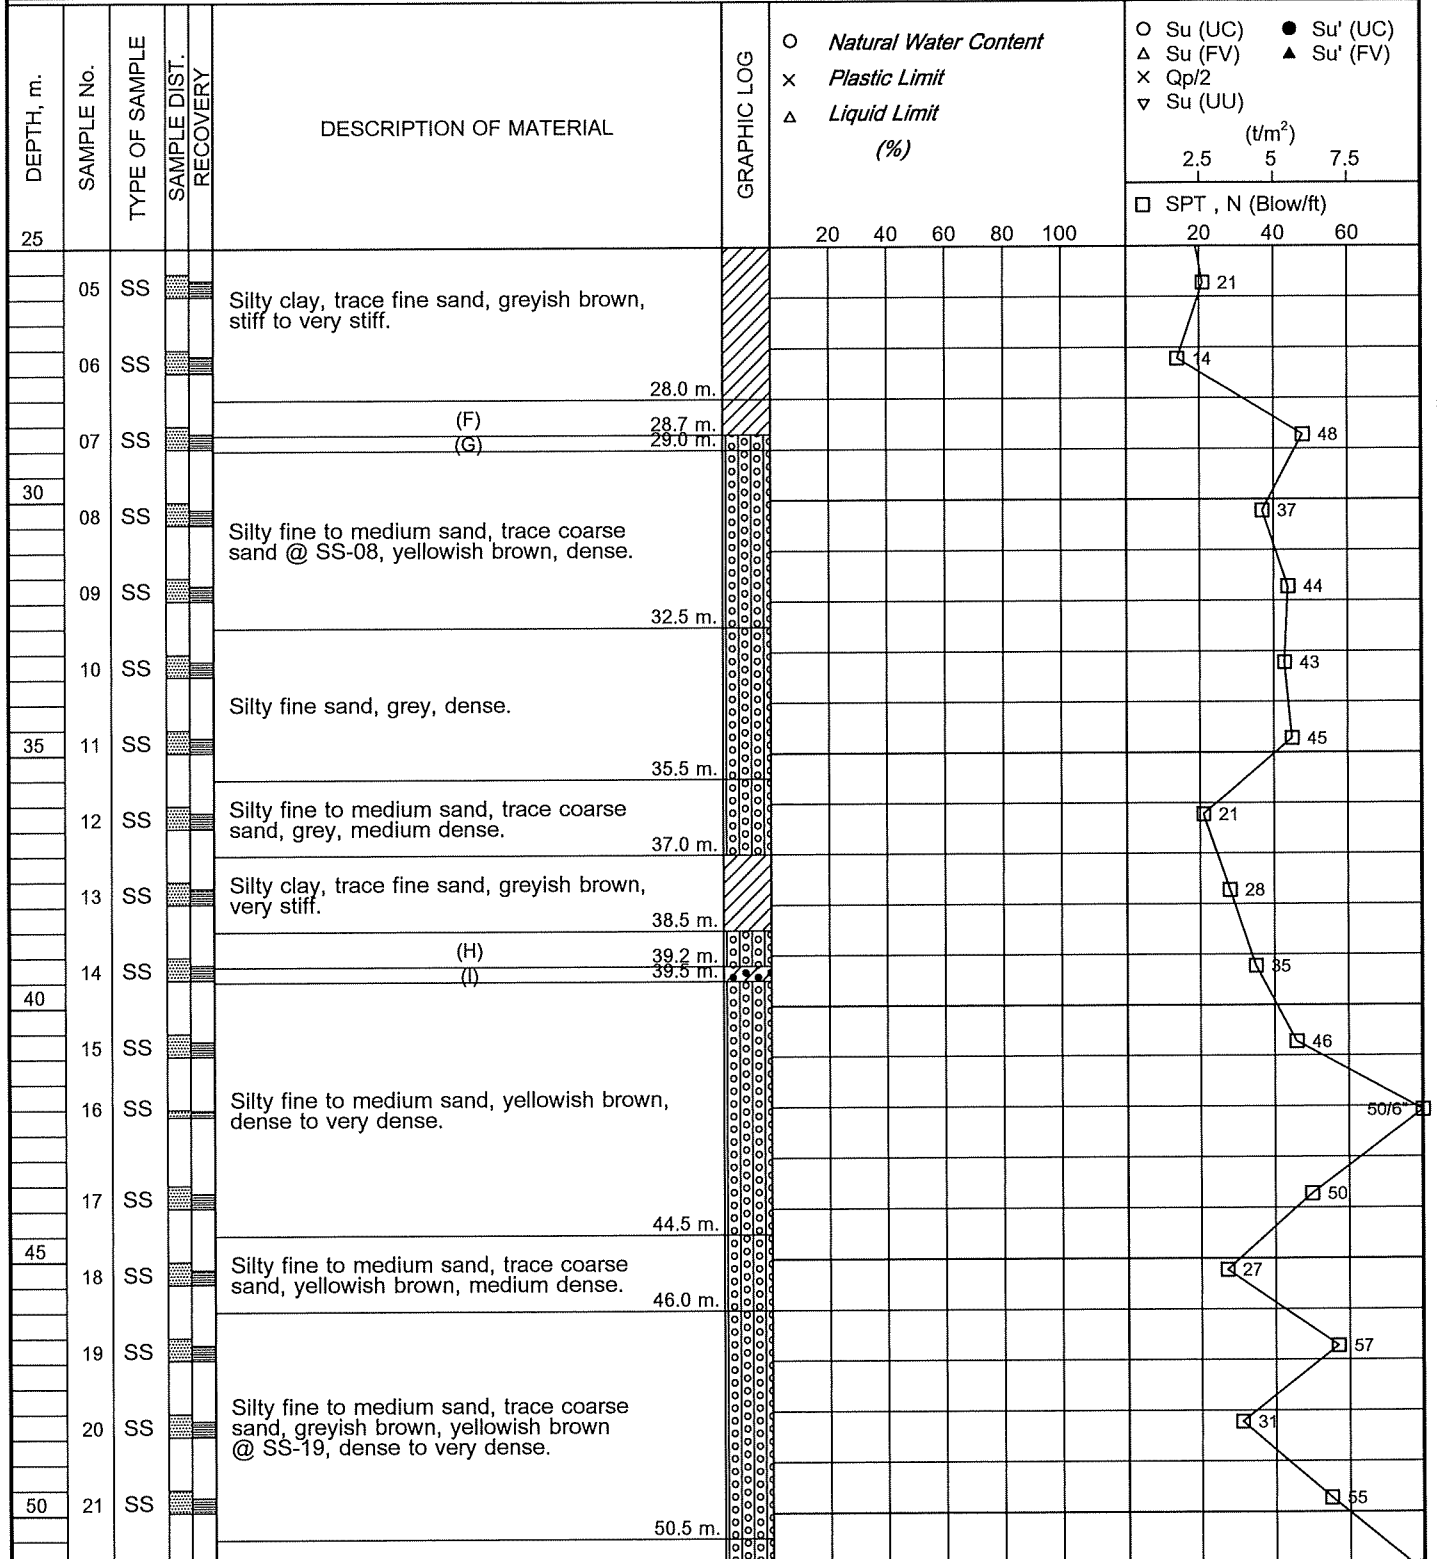

BORING STARTED : 08/03/25

RIG. ACKER

WL. -2.50 m 24 Hrs. After Boring

BORING FINISHED : 11/03/25

FOREMAN : WN.


JOB No. : 1168049

LOG OF BORING No. OW-23/5

PROJECT : MRT Orange Line Project Bang Khun Non -

LOCATION : Bangkok

Min Buri (Suwinthawong) Section Public - Private Partnership Contract

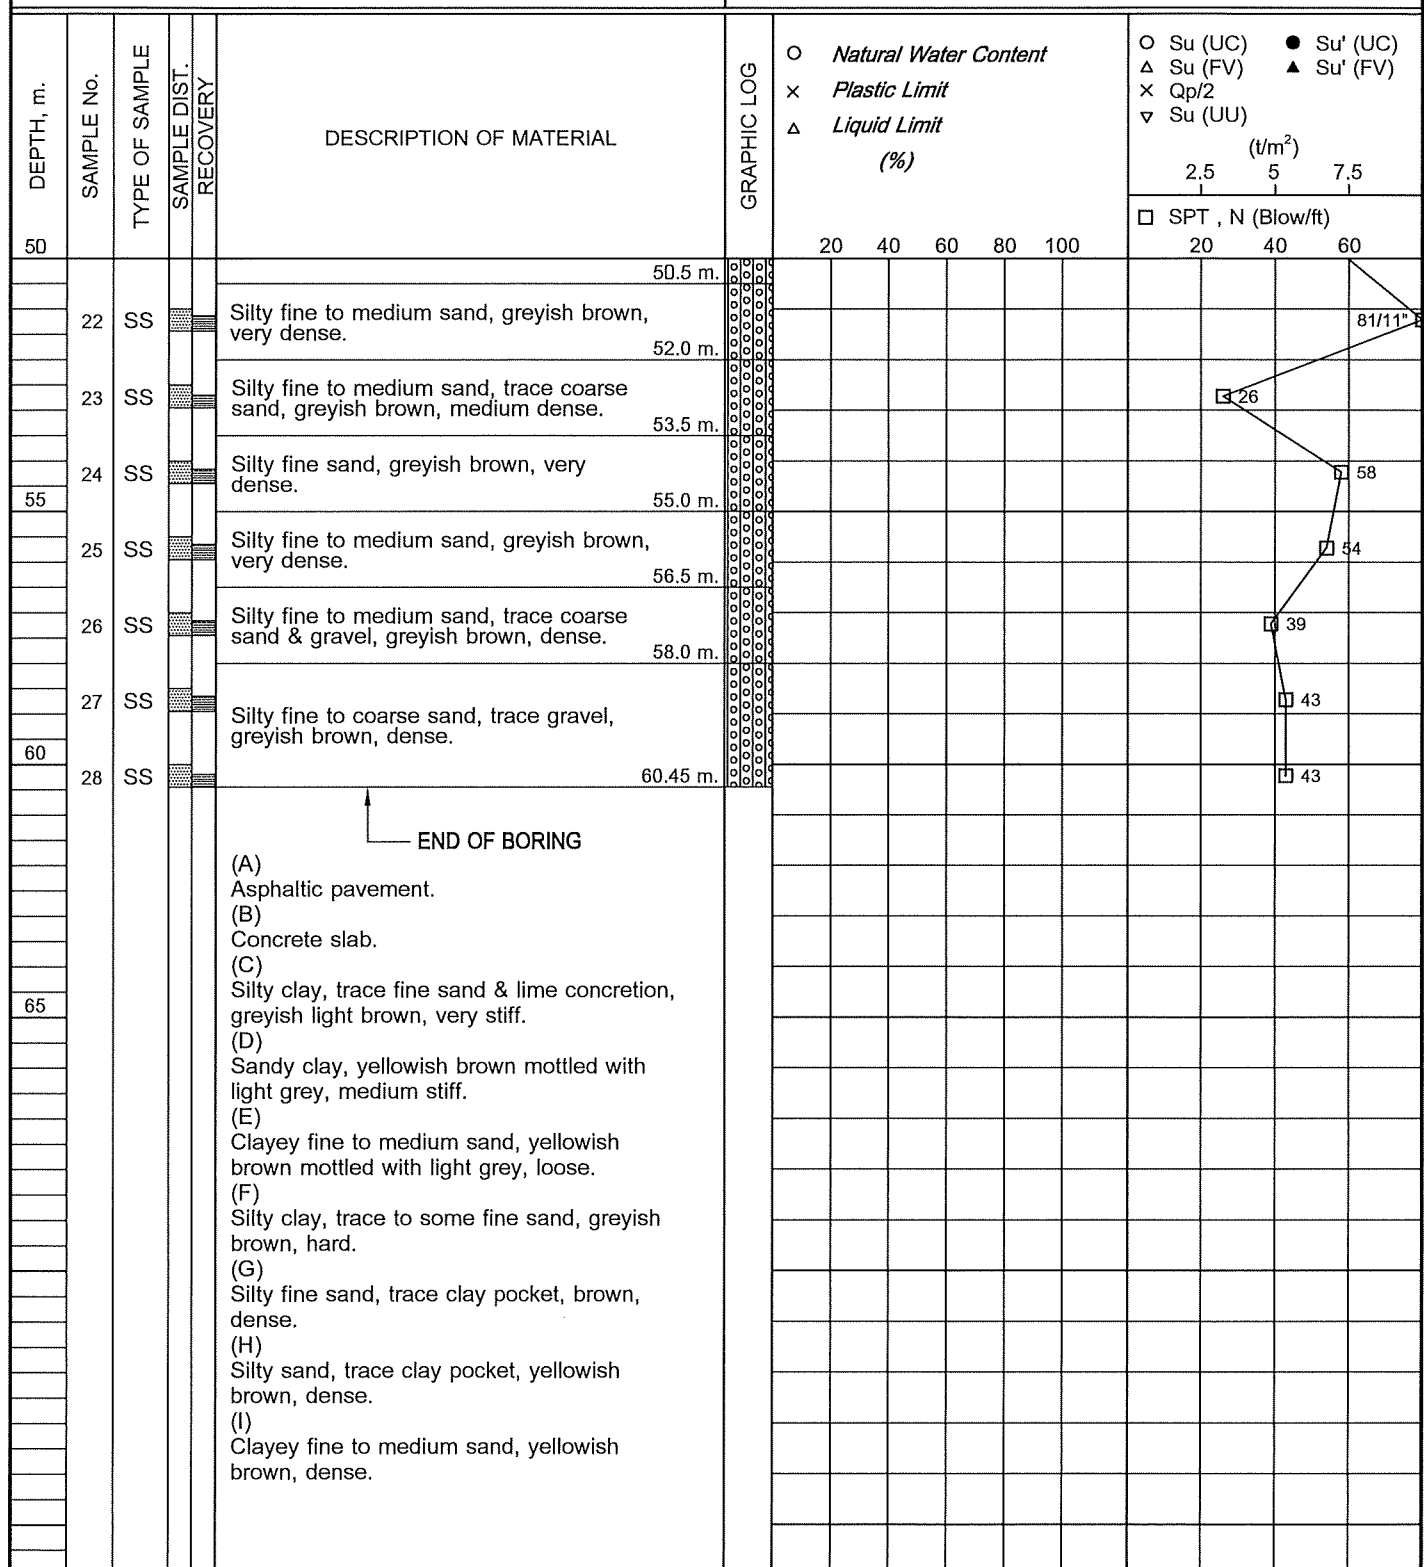

BORING STARTED : 08/03/25

R/G. ACKER

WL. -2.50 m

24 Hrs.
After Boring

BORING FINISHED : 11/03/25

FOREMAN : WN.

JOB No. : 1168049