


LOG OF BORING No. OW-37

PROJECT : MRT Orange Line Project : Bang Khun Non -

LOCATION : Bangkok

Min Buri (Suwinthawong) Section

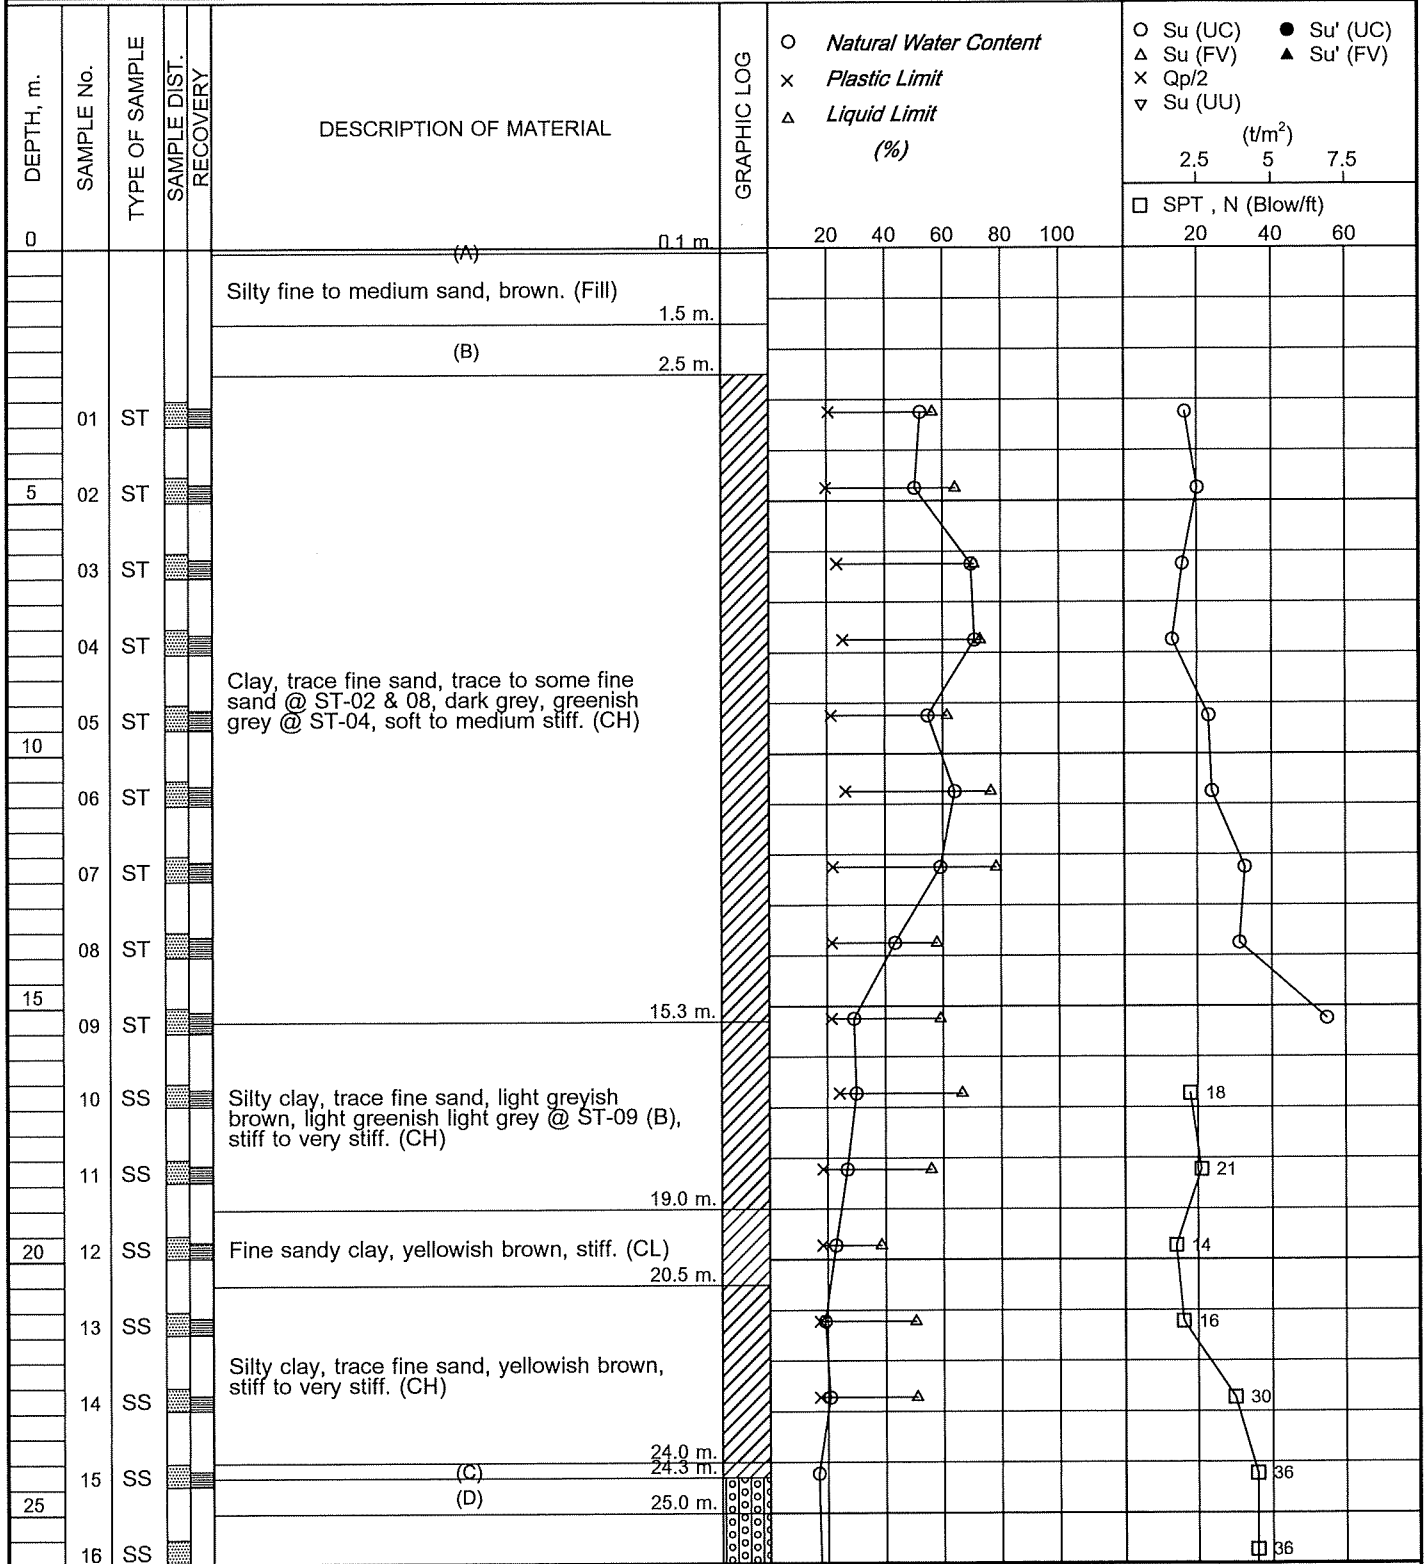

BORING STARTED : 05/02/25

RIG. ACKER

WL. -2.50 m 24 Hrs. After Boring

BORING FINISHED : 09/02/25

FOREMAN : WN.


JOB No. : 1167287

LOG OF BORING No. OW-37

PROJECT : MRT Orange Line Project : Bang Khun Non -

LOCATION : Bangkok

Min Buri (Suwinthawong) Section

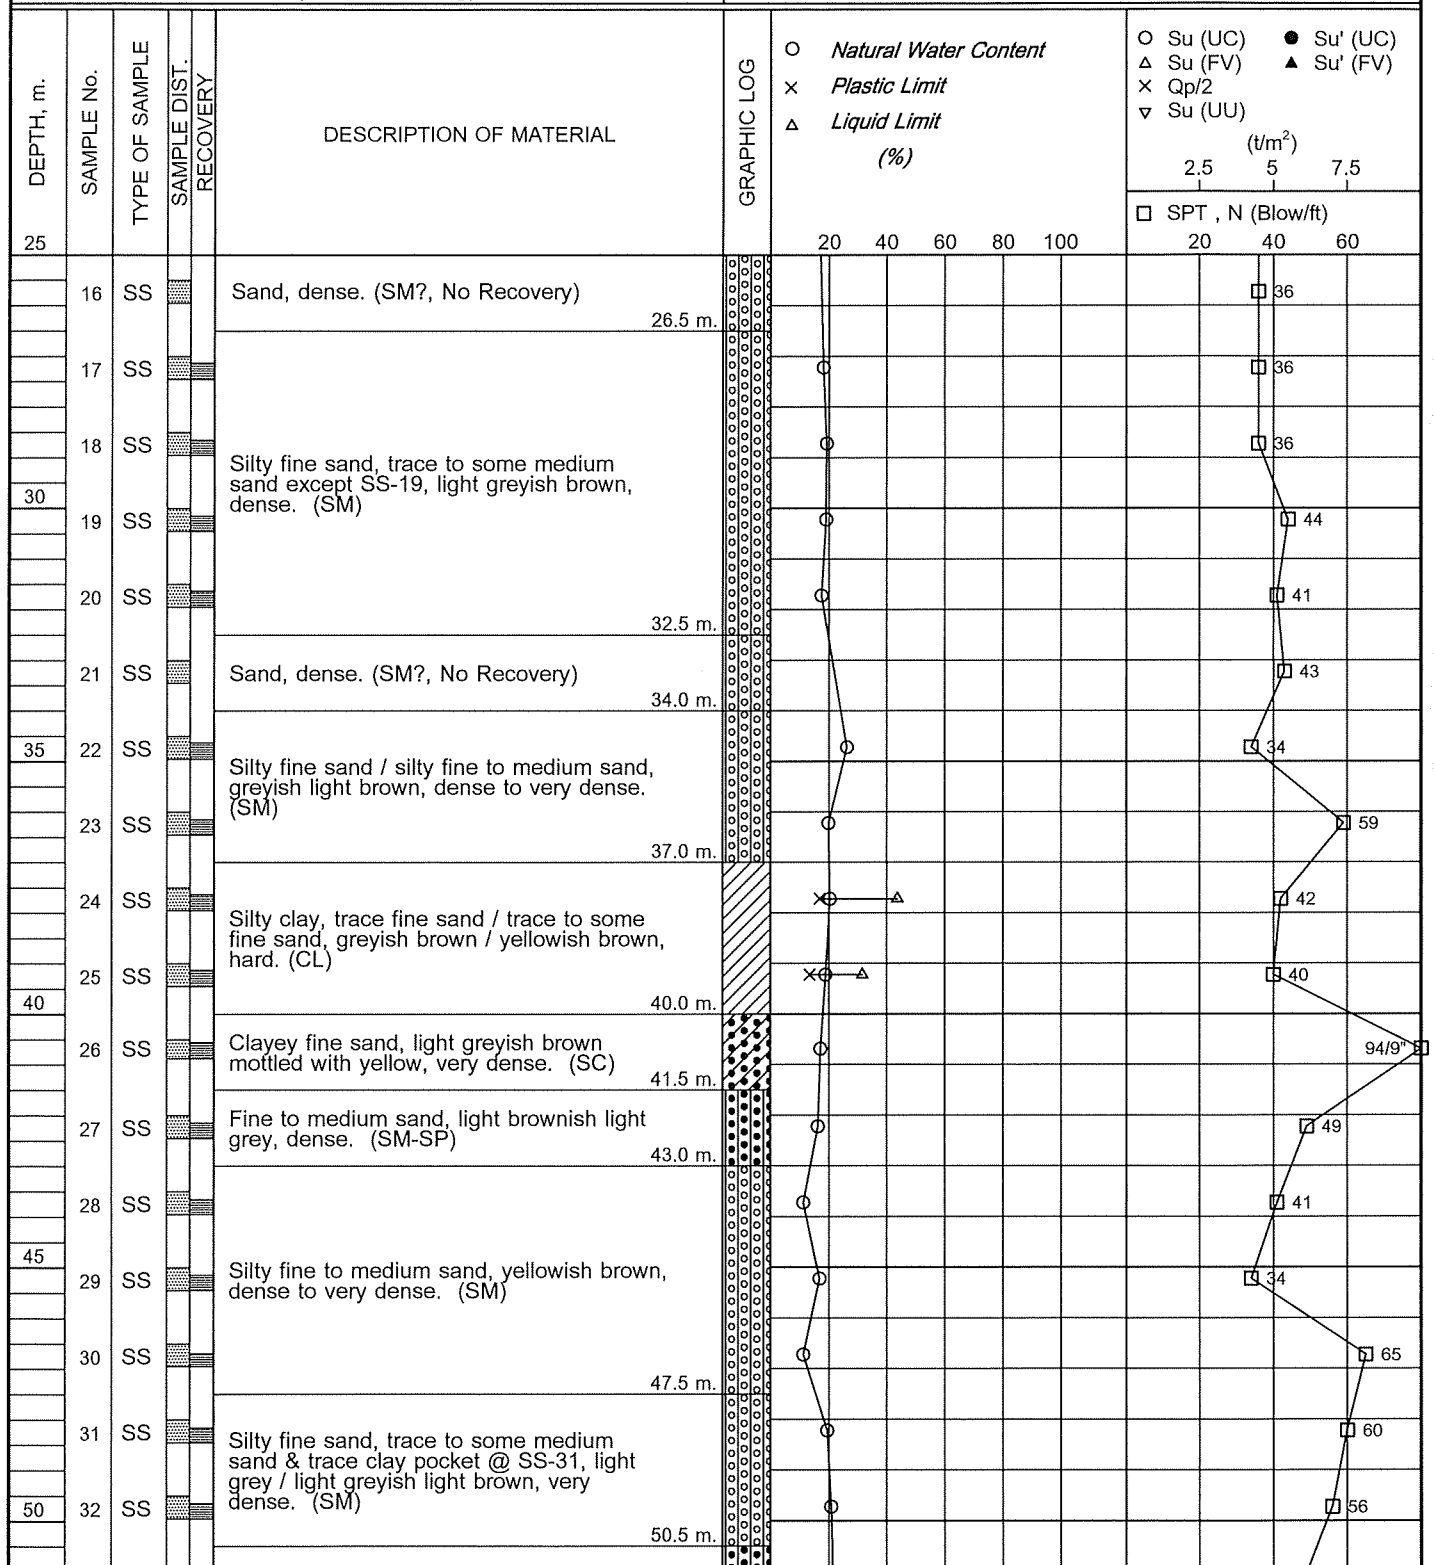

BORING STARTED : 05/02/25

RIG. ACKER

WL. -2.50 m

24 Hrs.
After Boring

BORING FINISHED : 09/02/25

FOREMAN : WN.


JOB No. : 1167287

LOG OF BORING No. OW-37

PROJECT : MRT Orange Line Project : Bang Khun Non -

LOCATION : Bangkok

Min Buri (Suwinthawong) Section

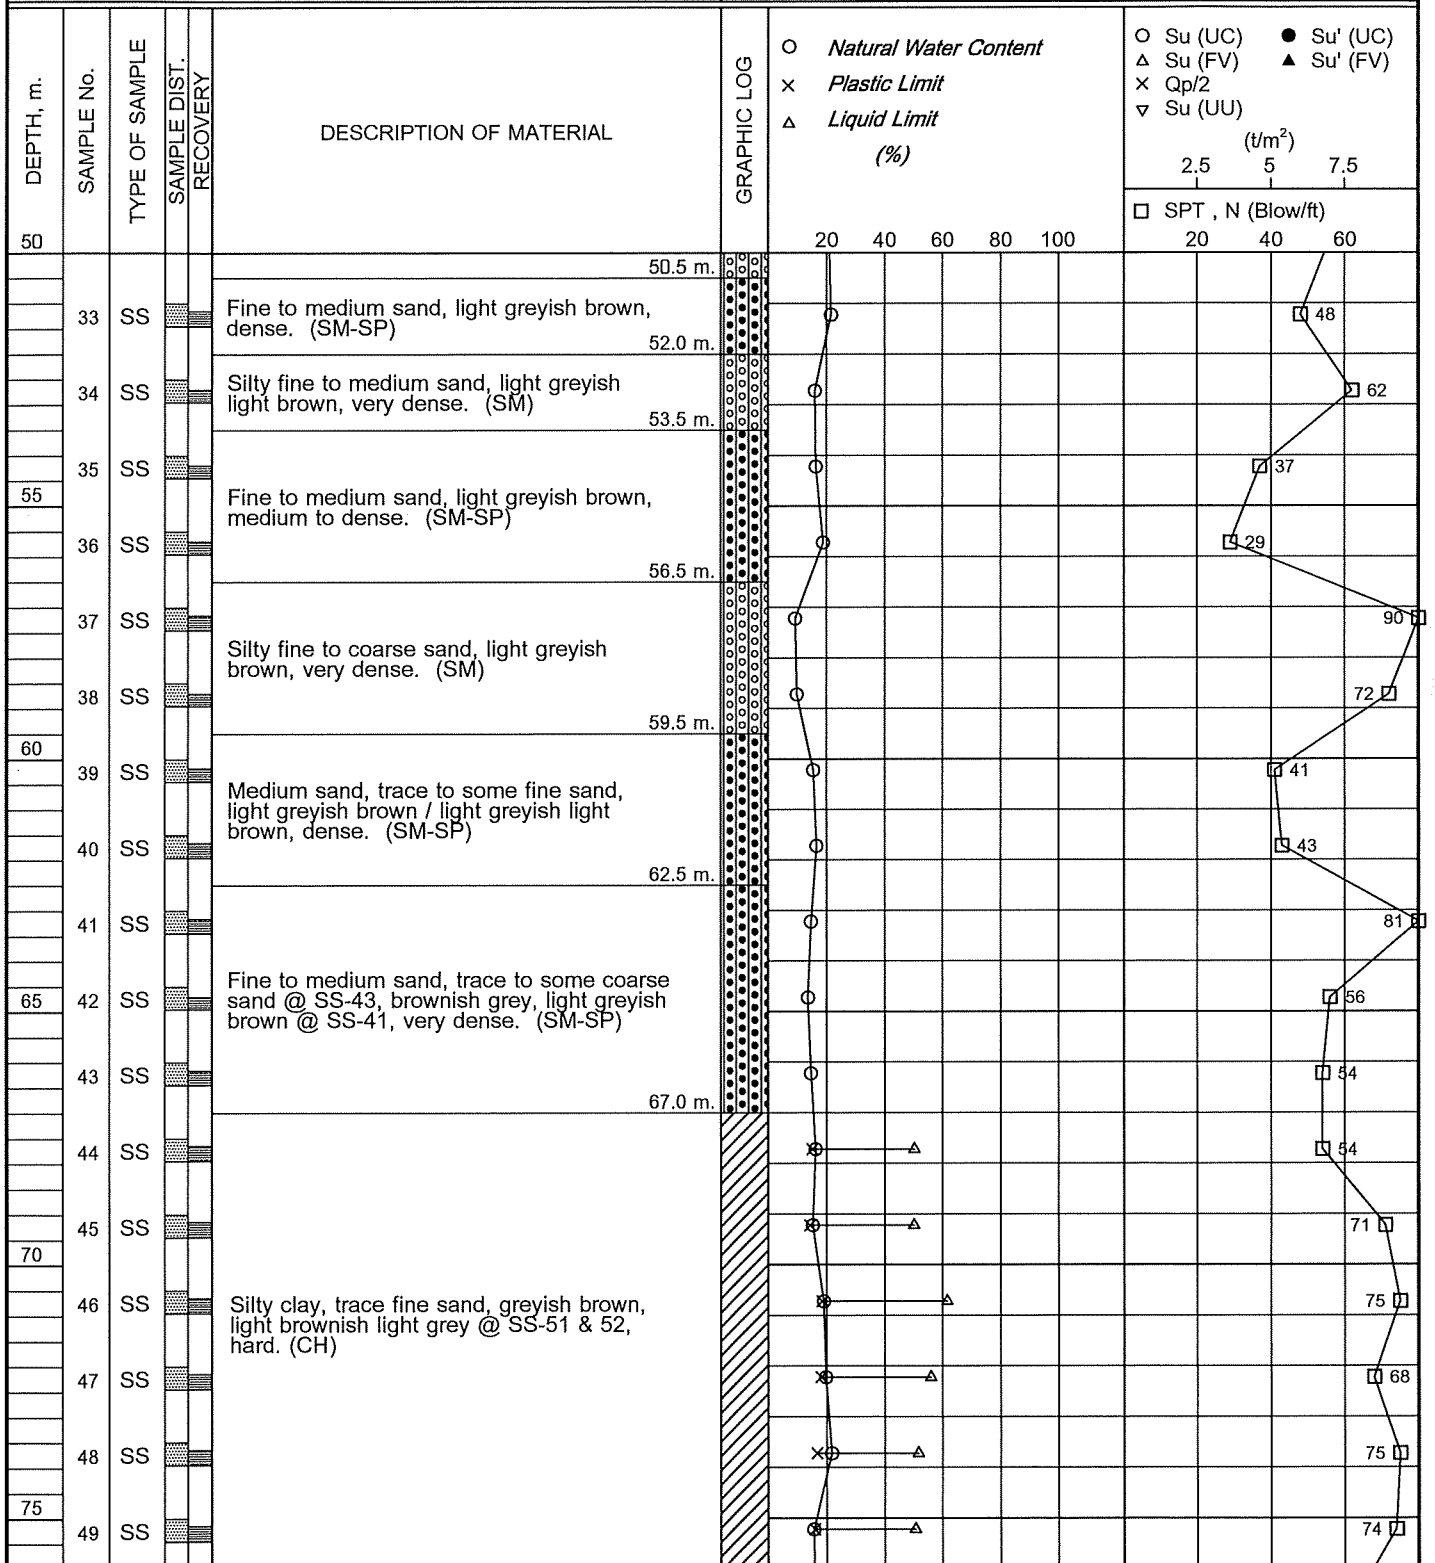

BORING STARTED : 05/02/25

RIG. ACKER

WL. -2.50 m 24 Hrs. After Boring

BORING FINISHED : 09/02/25

FOREMAN : WN.

JOB No. : 1167287

LOG OF BORING No. OW-37

PROJECT : MRT Orange Line Project : Bang Khun Non -

LOCATION : Bangkok

Min Buri (Suwinthawong) Section

DEPTH, m.	SAMPLE No.	TYPE OF SAMPLE	SAMPLE DIST. RECOVERY	DESCRIPTION OF MATERIAL	GRAPHIC LOG	○ Natural Water Content × Plastic Limit △ Liquid Limit (%) ○ Su (UC) ● Su' (UC) △ Su (FV) ▲ Su' (FV) × Qp/2 ▽ Su (UU) (t/m²) 2.5 5 7.5 □ SPT, N (Blow/ft) 20 40 60
-----------	------------	----------------	-----------------------	-------------------------	-------------	---



BORING STARTED : 05/02/25

RIG. ACKER

WL. -2.50 m

24 Hrs.
After Boring

BORING FINISHED : 09/02/25

FOREMAN : WN.

JOB No. : 1167287