


LOG OF BORING No. OW-39

PROJECT : MRT Orange Line Project : Bang Khun Non -

LOCATION : Bangkok

Min Buri (Suwinthawong) Section

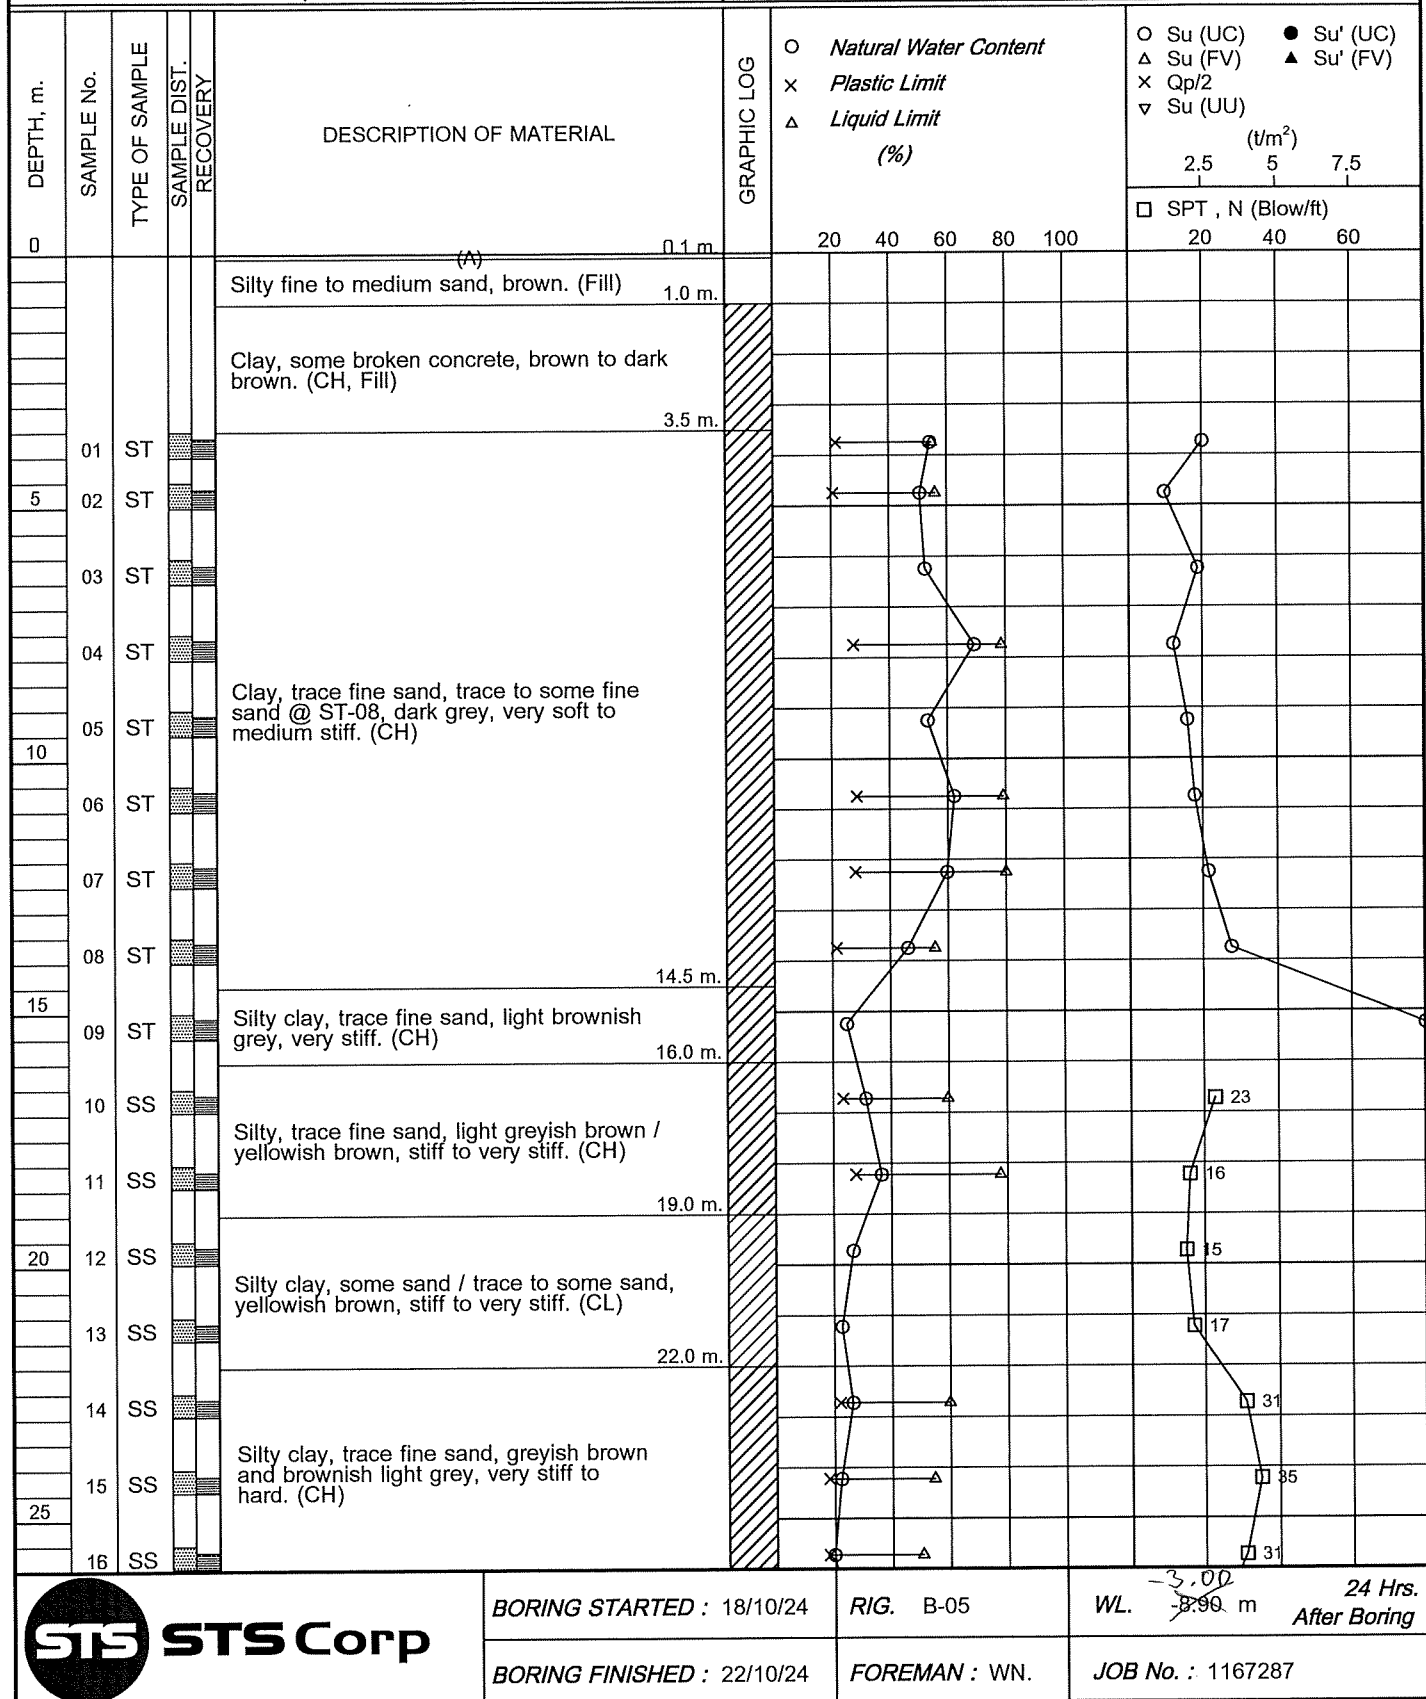


LOG OF BORING No. OW-39

PROJECT : MRT Orange Line Project : Bang Khun Non -

LOCATION : Bangkok

Min Buri (Suwinthawong) Section

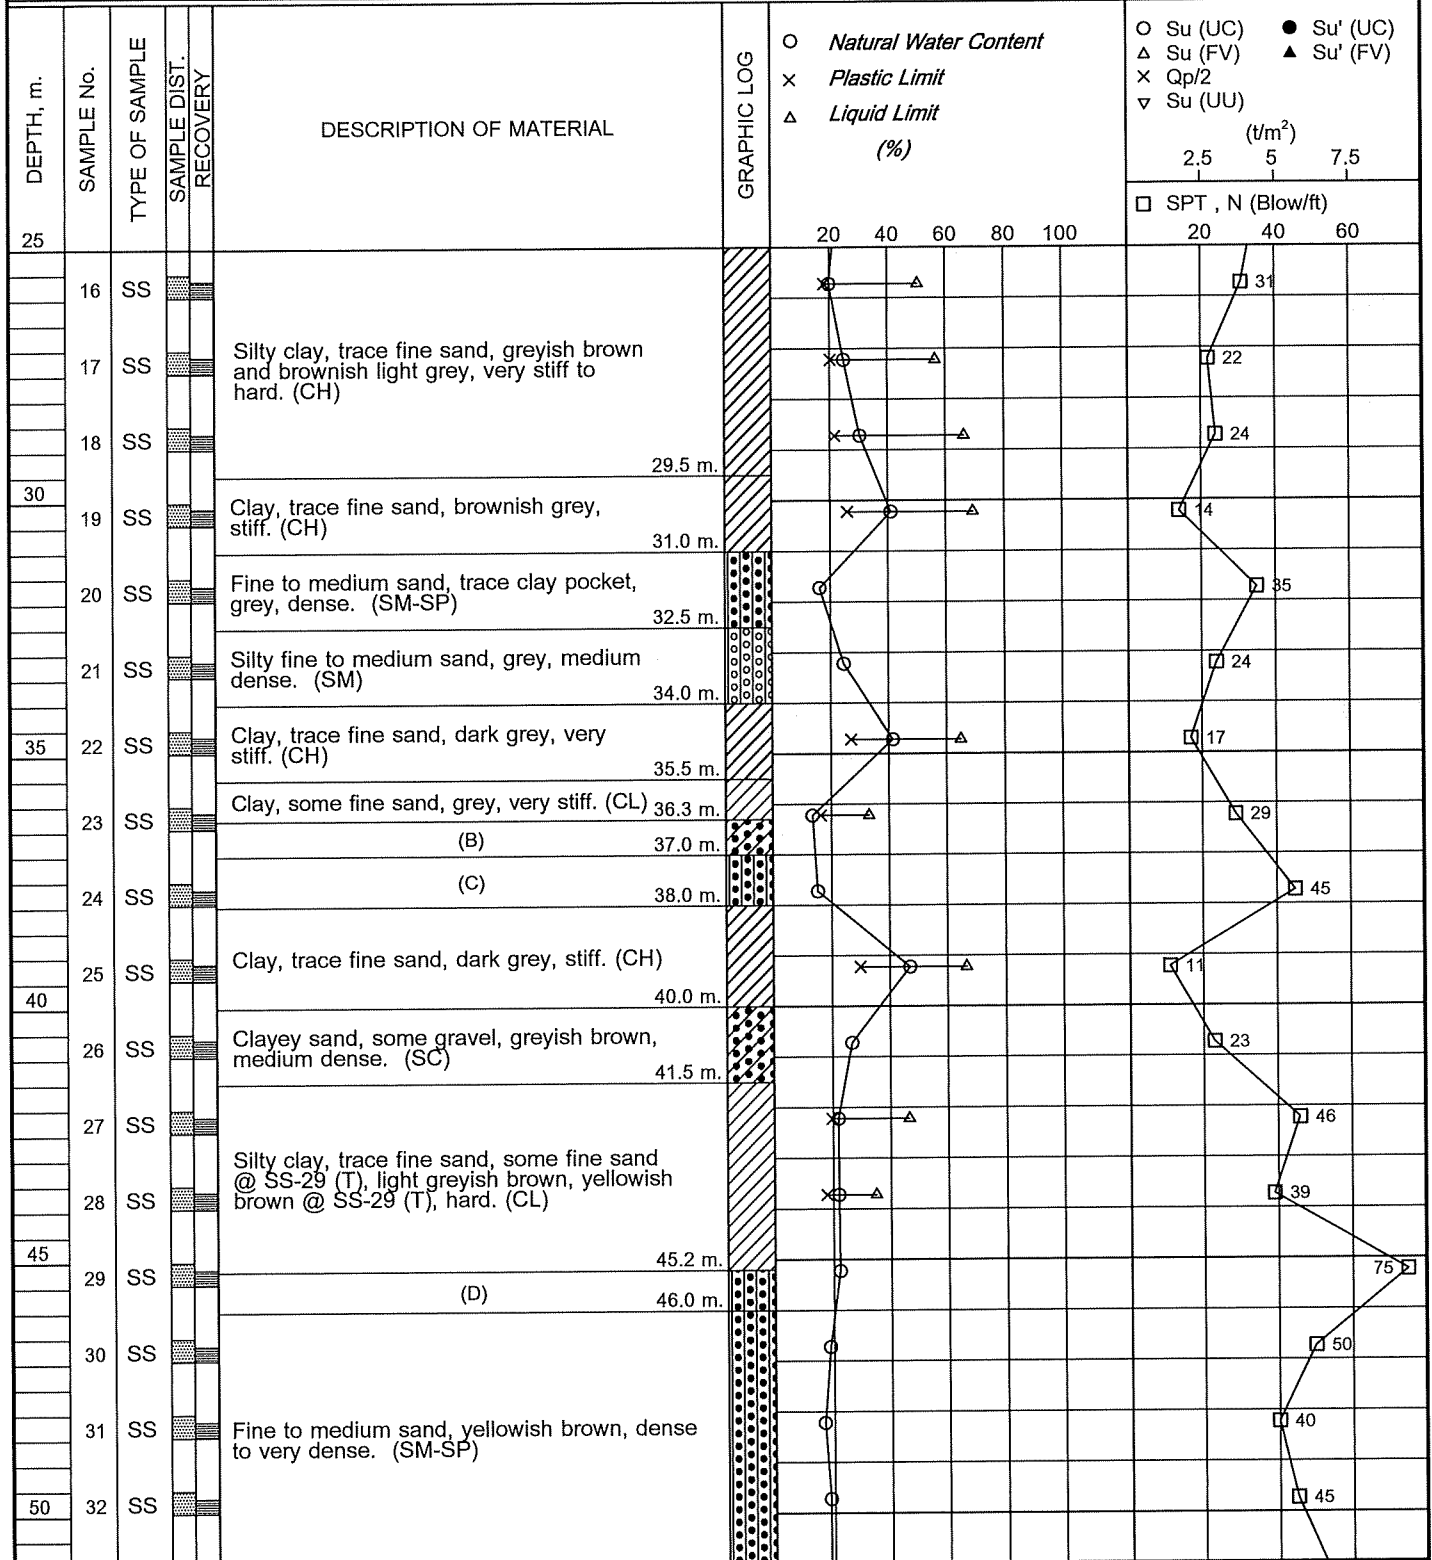

BORING STARTED : 18/10/24

RIG. B-05

WL. -3.00
-8.90 m 24 Hrs.
After Boring

BORING FINISHED : 22/10/24

FOREMAN : WN.


JOB No. : 1167287

LOG OF BORING No. OW-39

PROJECT : MRT Orange Line Project : Bang Khun Non -

LOCATION : Bangkok

Min Buri (Suwinthawong) Section

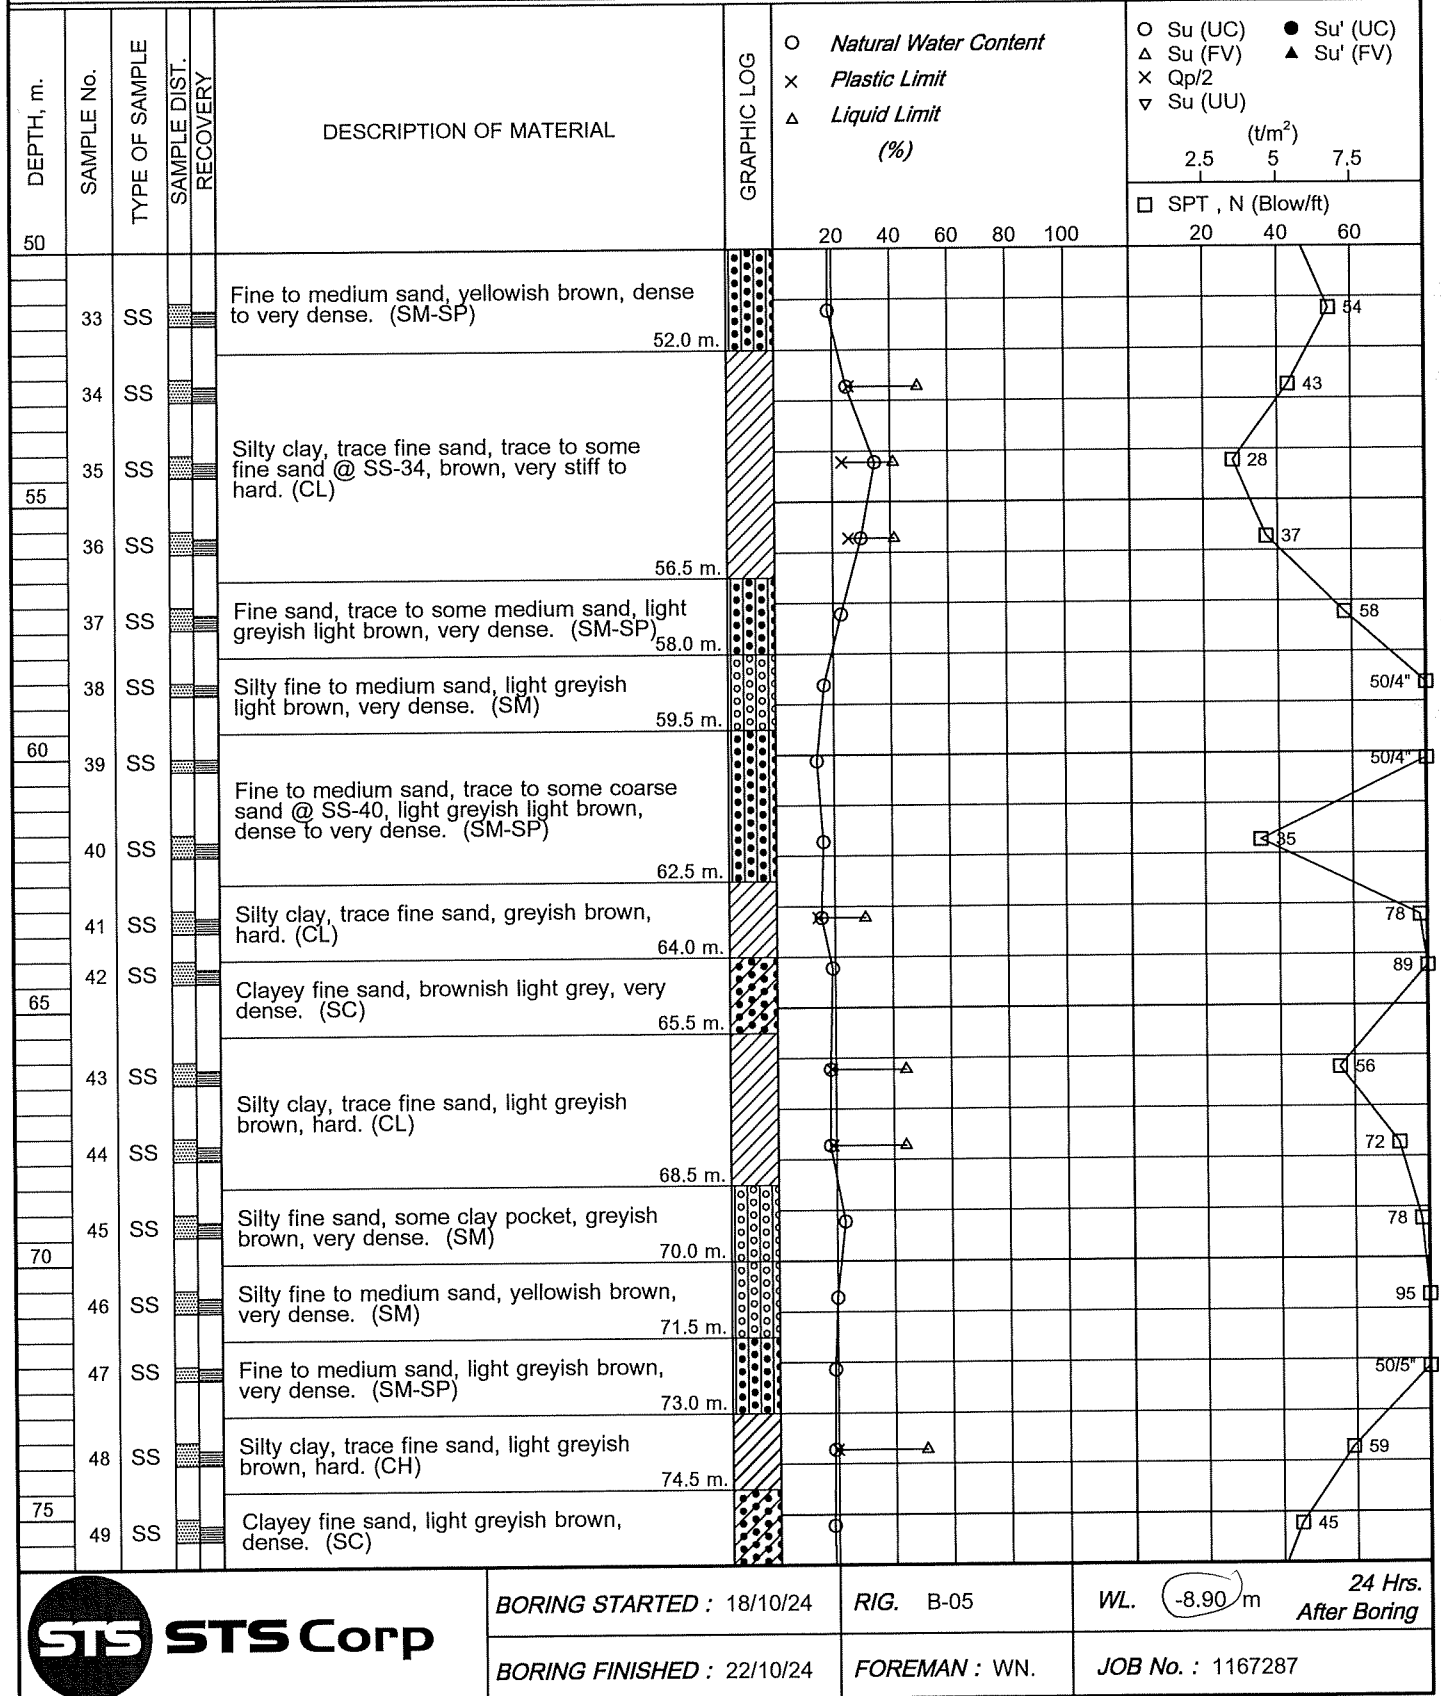


LOG OF BORING No. OW-39

PROJECT : MRT Orange Line Project : Bang Khun Non -

LOCATION : Bangkok

Min Buri (Suwinthawong) Section

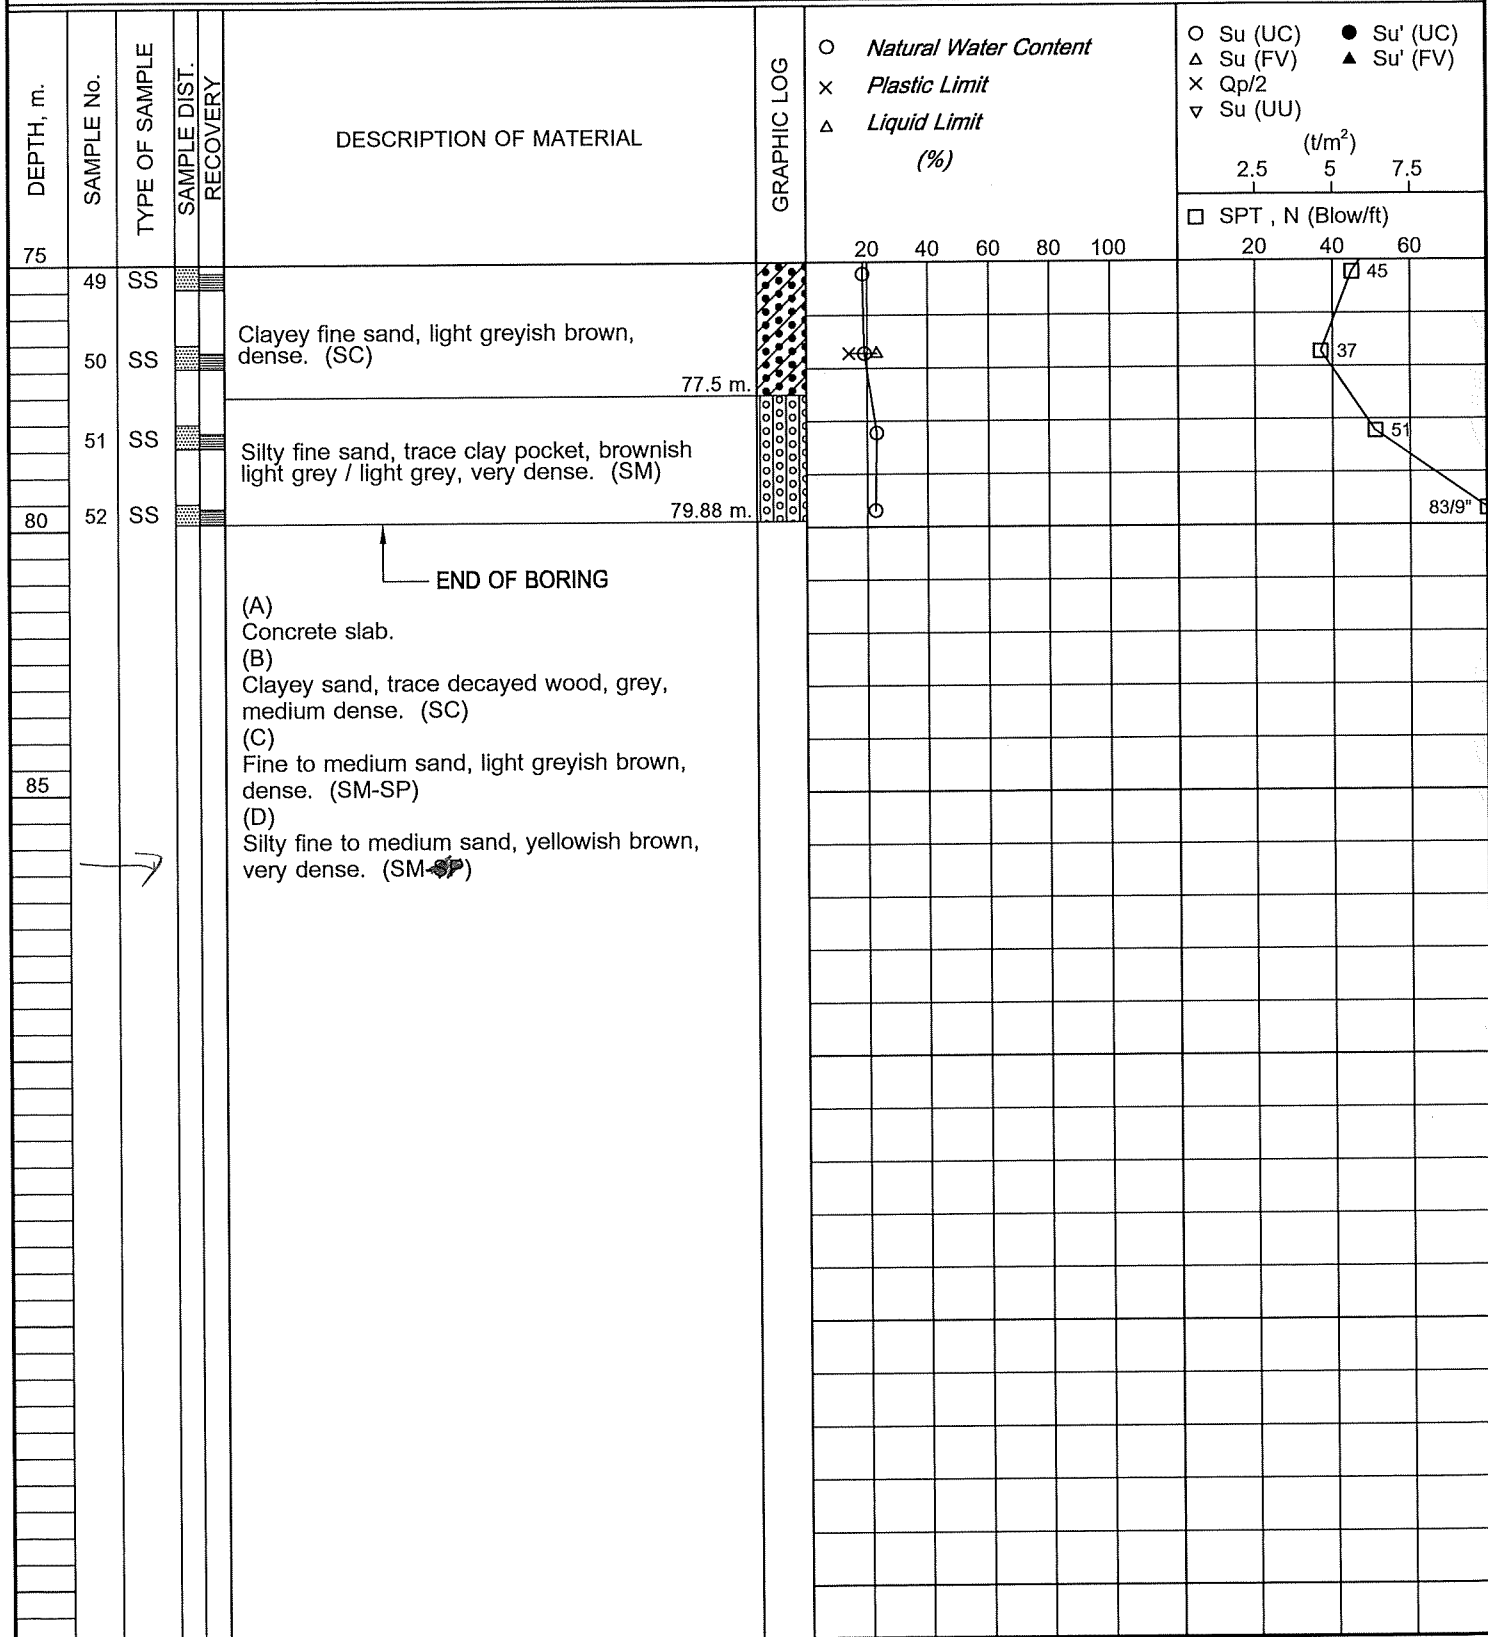

BORING STARTED : 18/10/24

RIG. B-05

WL. -8.90 m 24 Hrs. After Boring

BORING FINISHED : 22/10/24

FOREMAN : WN.

JOB No. : 1167287