


LOG OF BORING No. OW-42

PROJECT : MRT Orange Line Project : Bang Khun Non -

LOCATION : Bangkok

Min Buri (Suwinthawong) Section

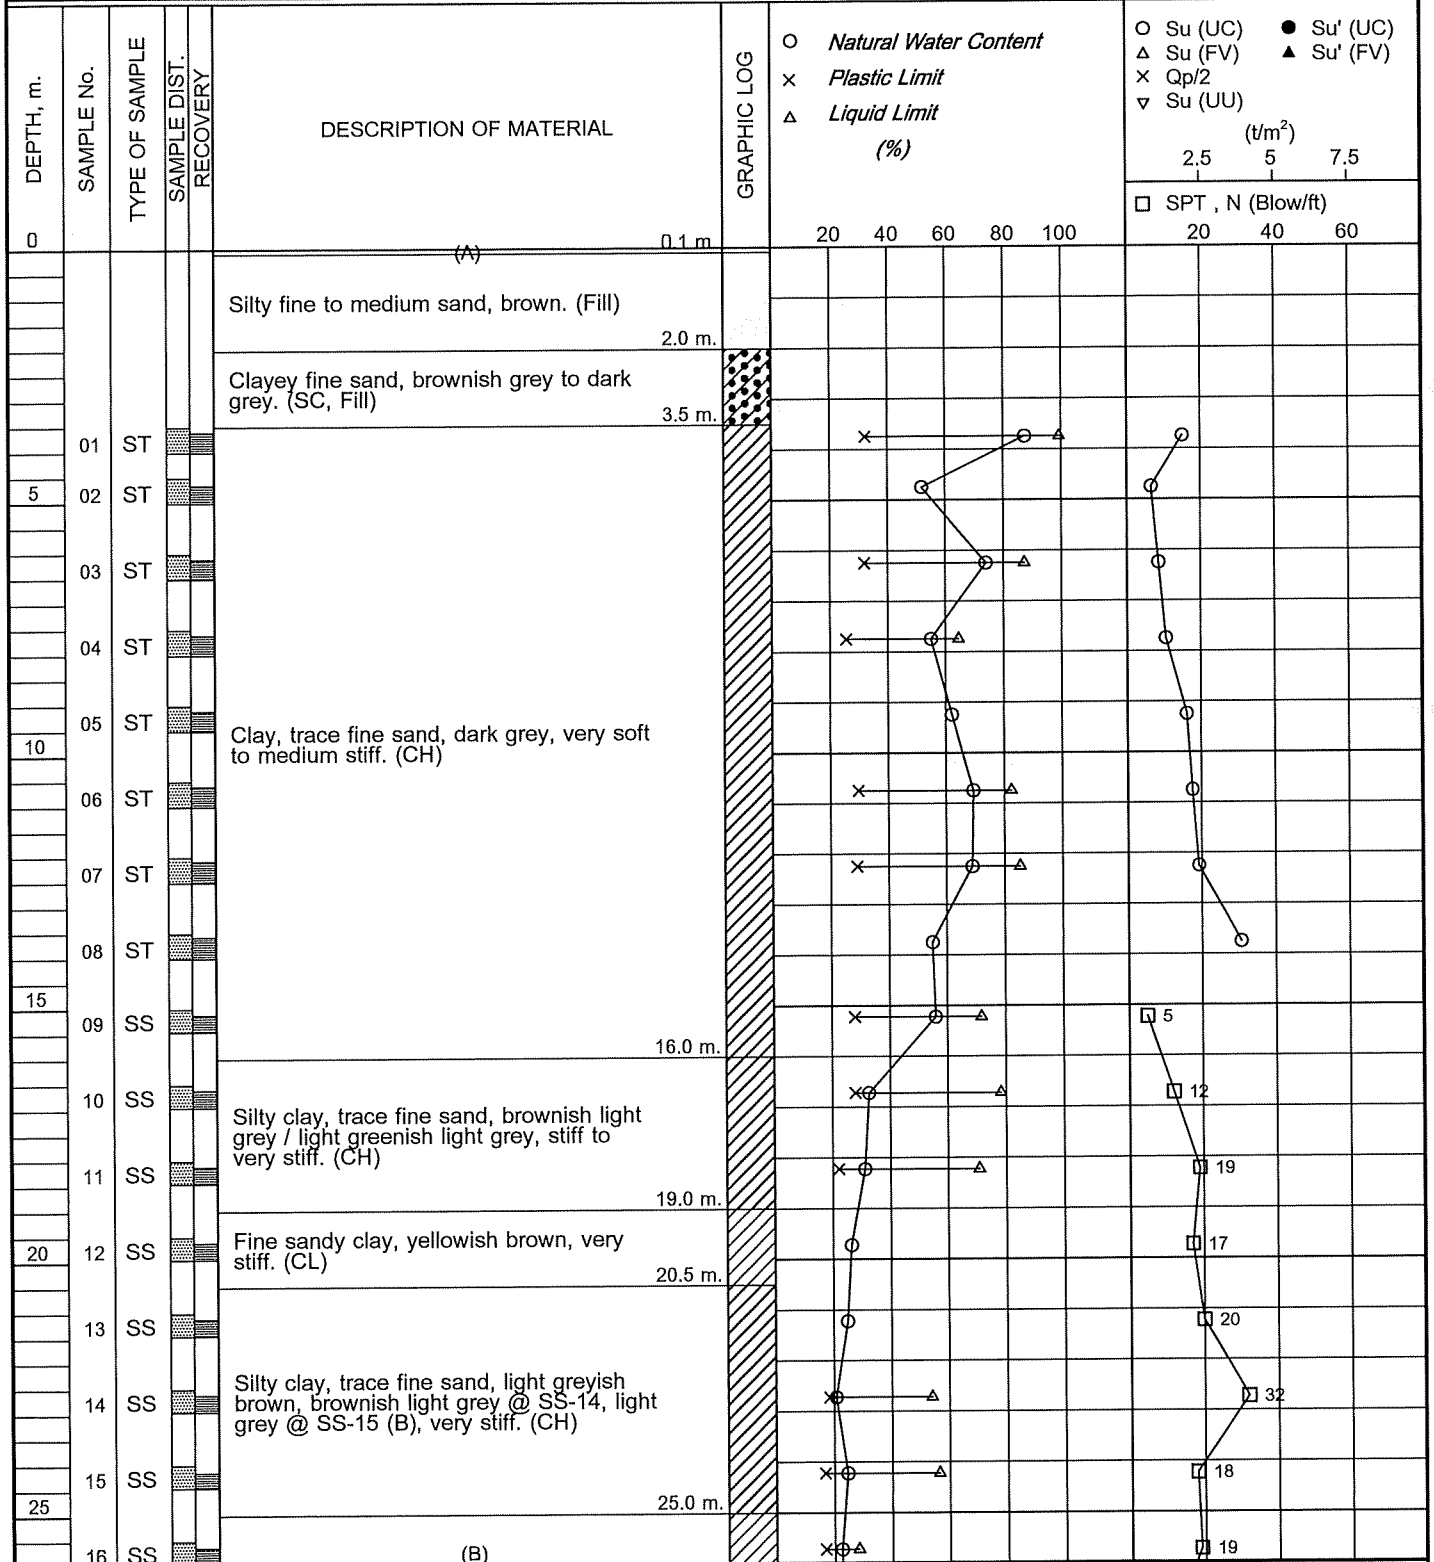

BORING STARTED : 08/10/24

RIG. ACKER

WL. ~~-3.00~~ -9.00 m 24 Hrs. After Boring

BORING FINISHED : 12/10/24

FOREMAN : WN.


JOB No. : 1167287

LOG OF BORING No. OW-42

PROJECT : MRT Orange Line Project : Bang Khun Non -

LOCATION : Bangkok

Min Buri (Suwinthawong) Section

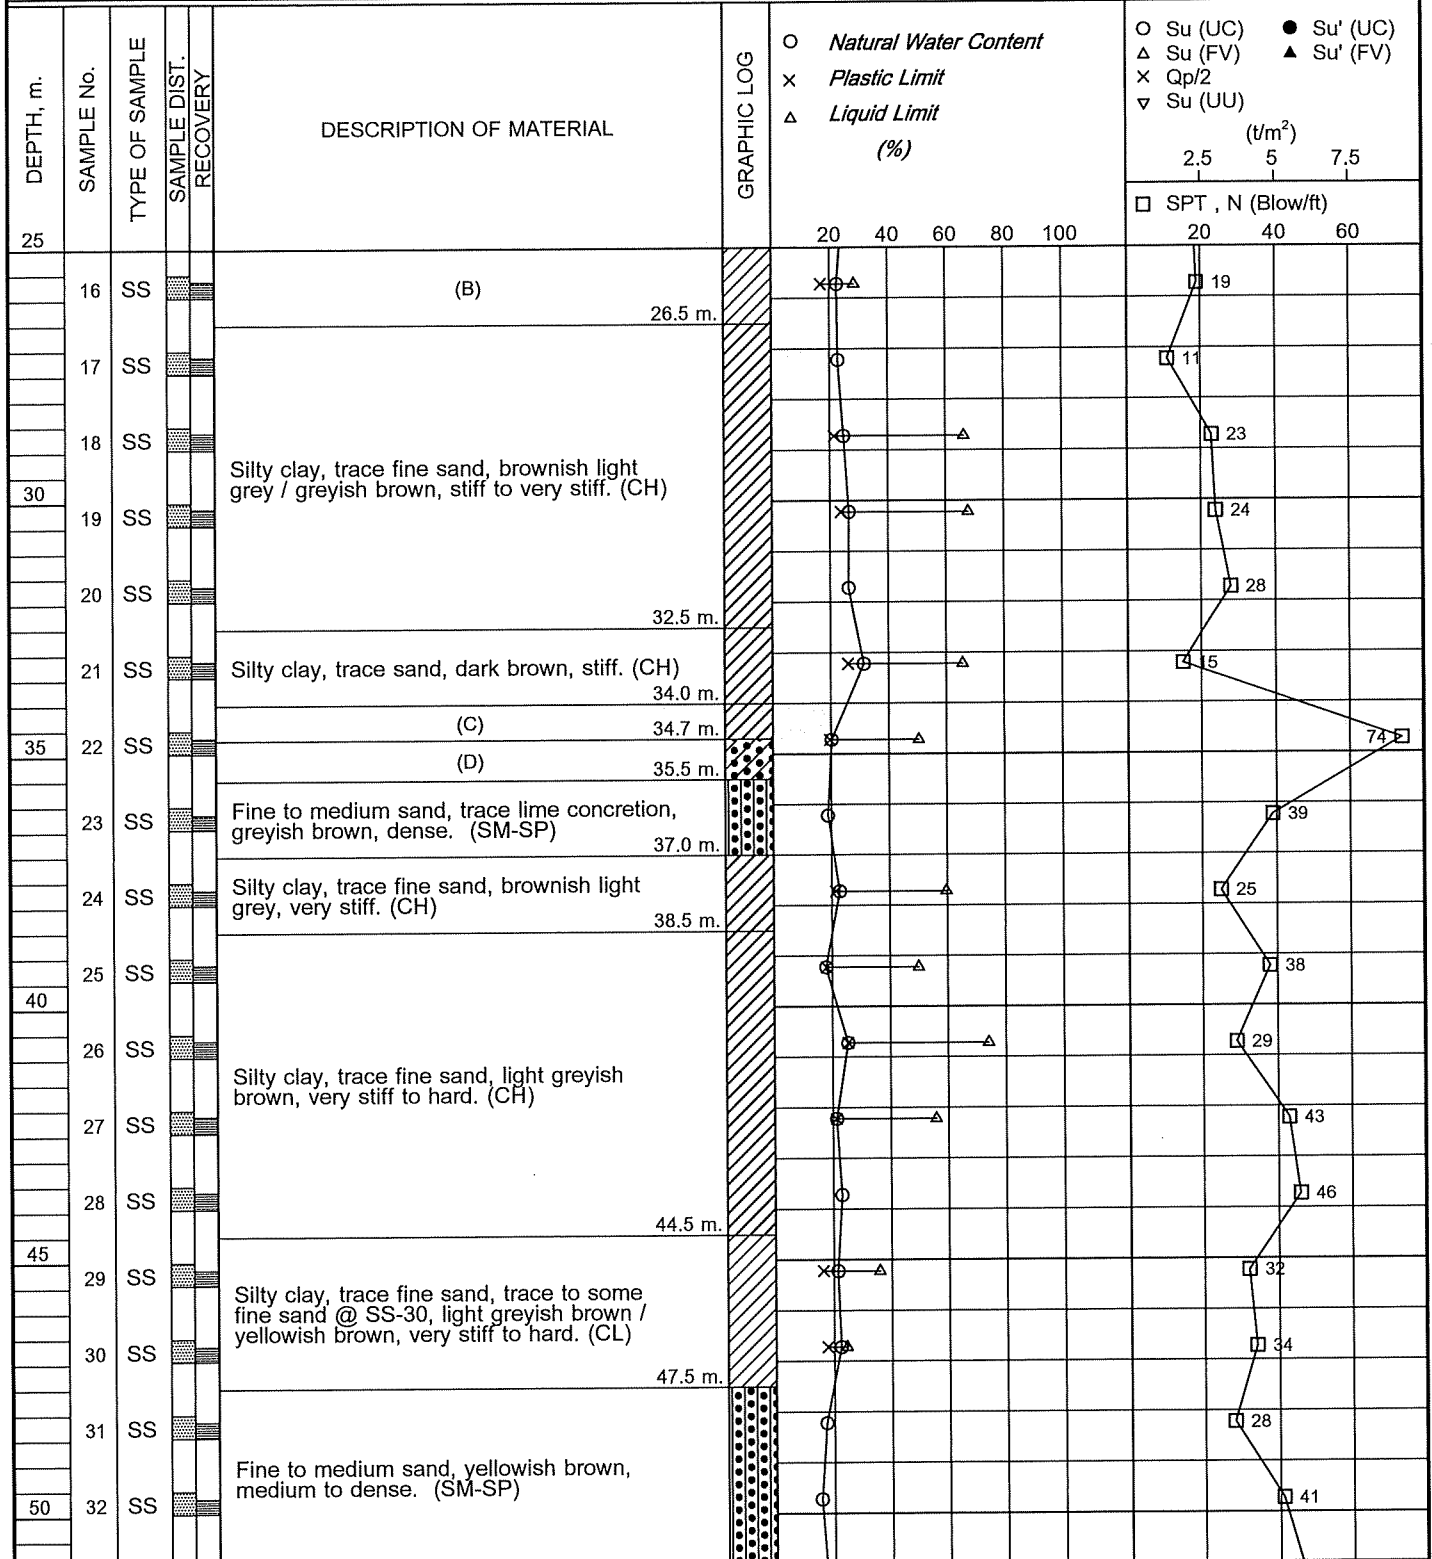

BORING STARTED : 08/10/24

RIG. ACKER

WL. -3.00 24 Hrs. After Boring
-9.00 m

BORING FINISHED : 12/10/24

FOREMAN : WN.


JOB No. : 1167287

LOG OF BORING No. OW-42

PROJECT : MRT Orange Line Project : Bang Khun Non -

LOCATION : Bangkok

Min Buri (Suwinthawong) Section

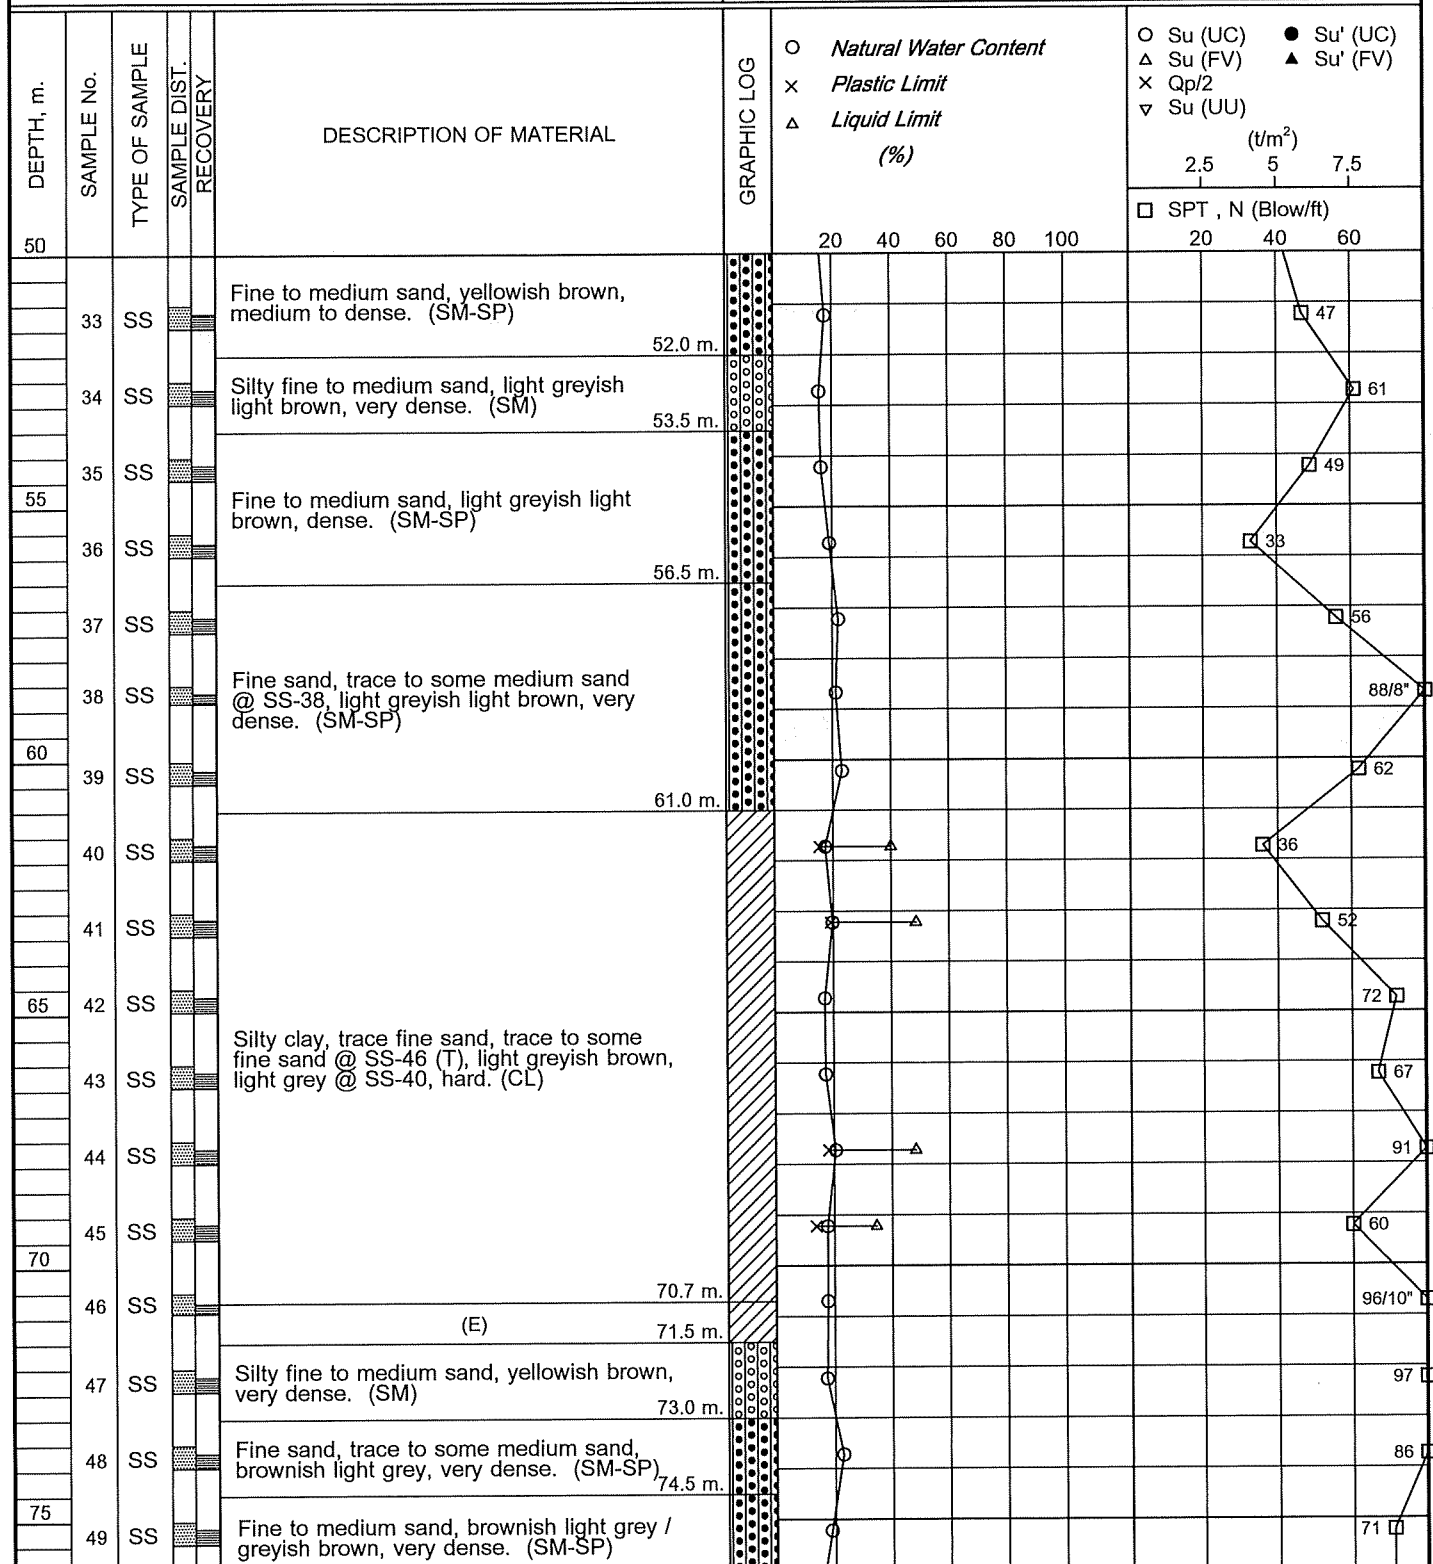

BORING STARTED : 08/10/24

RIG. ACKER

WL. $\frac{-3.00}{-9.00}$ m 24 Hrs. After Boring

BORING FINISHED : 12/10/24

FOREMAN : WN.

JOB No. : 1167287

LOG OF BORING No. OW-42

PROJECT : MRT Orange Line Project : Bang Khun Non -

LOCATION : Bangkok

Min Buri (Suwinthawong) Section

DEPTH, m.	SAMPLE No.	TYPE OF SAMPLE	SAMPLE DIST. RECOVERY	DESCRIPTION OF MATERIAL	GRAPHIC LOG	○ <i>Natural Water Content</i> × <i>Plastic Limit</i> △ <i>Liquid Limit (%)</i>		○ Su (UC) ● Su' (UC) △ Su (FV) ▲ Su' (FV) × Qp/2 ▽ Su (UU)		2.5 5 7.5 (t/m²)		□ SPT, N (Blow/ft) 20 40 60	
						20	40	60	80	100	20	40	60
75													
	49	SS		Fine to medium sand, brownish light grey / greyish brown, very dense. (SM-SP)									71
	50	SS											71
				77.7 m.									
	51	SS		Silty clay, trace fine sand, trace lime concretion @ SS-51, greyish brown, hard. (CL)									69
	52	SS											81
80				79.95 m.									
				END OF BORING									
				(A) Concrete slab.									
				(B) Silty clay, trace to some fine sand, yellowish brown mottled with red, very stiff. (CL)									
				(C) Clay, trace fine sand, grey, stiff. (CH)									
85				(D) Clayey fine to medium sand, grey, very dense. (SC)									
				(E) Fine sandy clay, brown, hard. (CL)									



BORING STARTED : 08/10/24

RIG. ACKER

WL. ~~-3.00~~ ^{-9.00} m 24 Hrs. After Boring

BORING FINISHED : 12/10/24

FOREMAN : WN.

JOB No. : 1167287