


LOG OF BORING No. OW-43

PROJECT : MRT Orange Line Project : Bang Khun Non -

LOCATION : Bangkok

Min Buri (Suwinthawong) Section

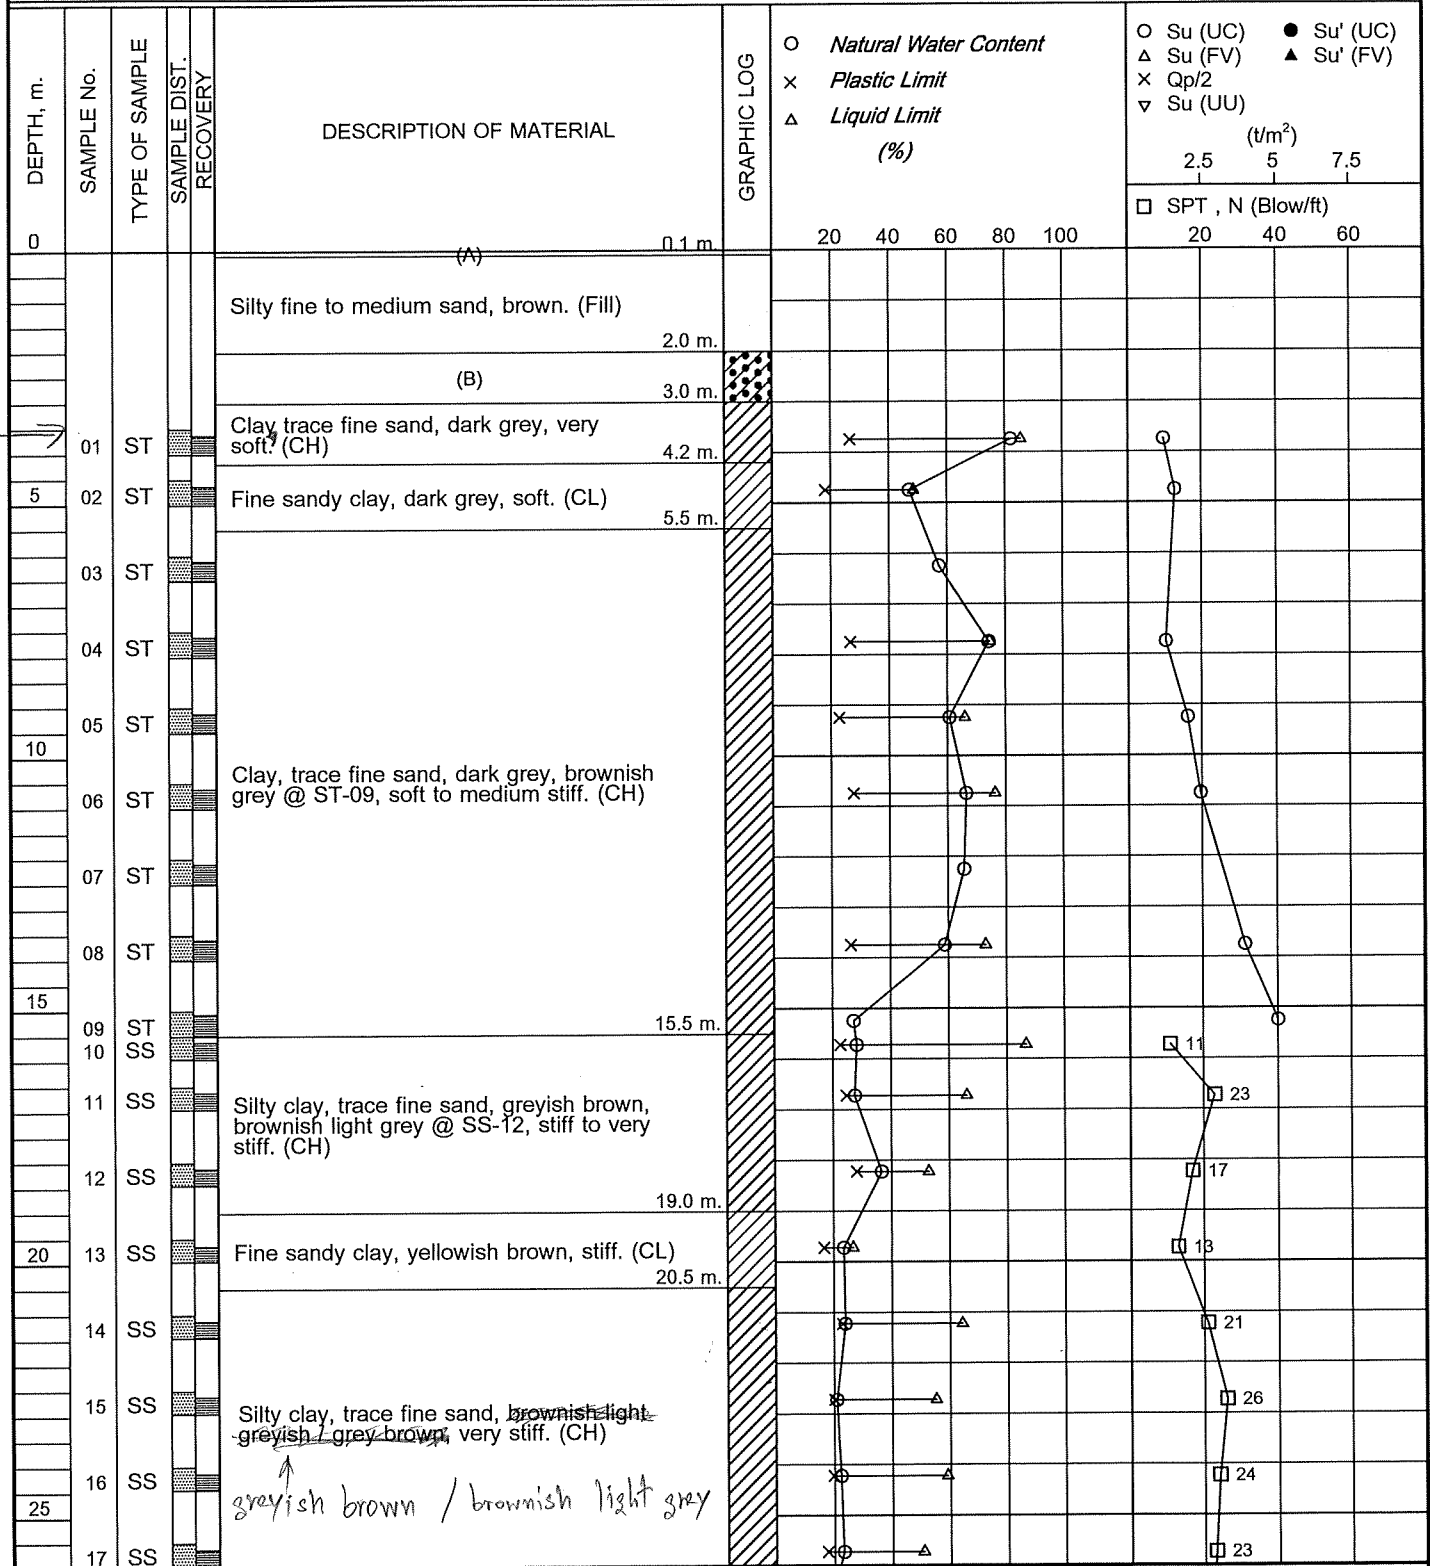

BORING STARTED : 02/10/00

RIG. ACKER

WL. -3.00 m 24 Hrs. After Boring

BORING FINISHED : 06/09/24

FOREMAN : WN.


JOB No. : 1167287

LOG OF BORING No. OW-43

PROJECT : MRT Orange Line Project : Bang Khun Non -

LOCATION : Bangkok

Min Buri (Suwinthawong) Section

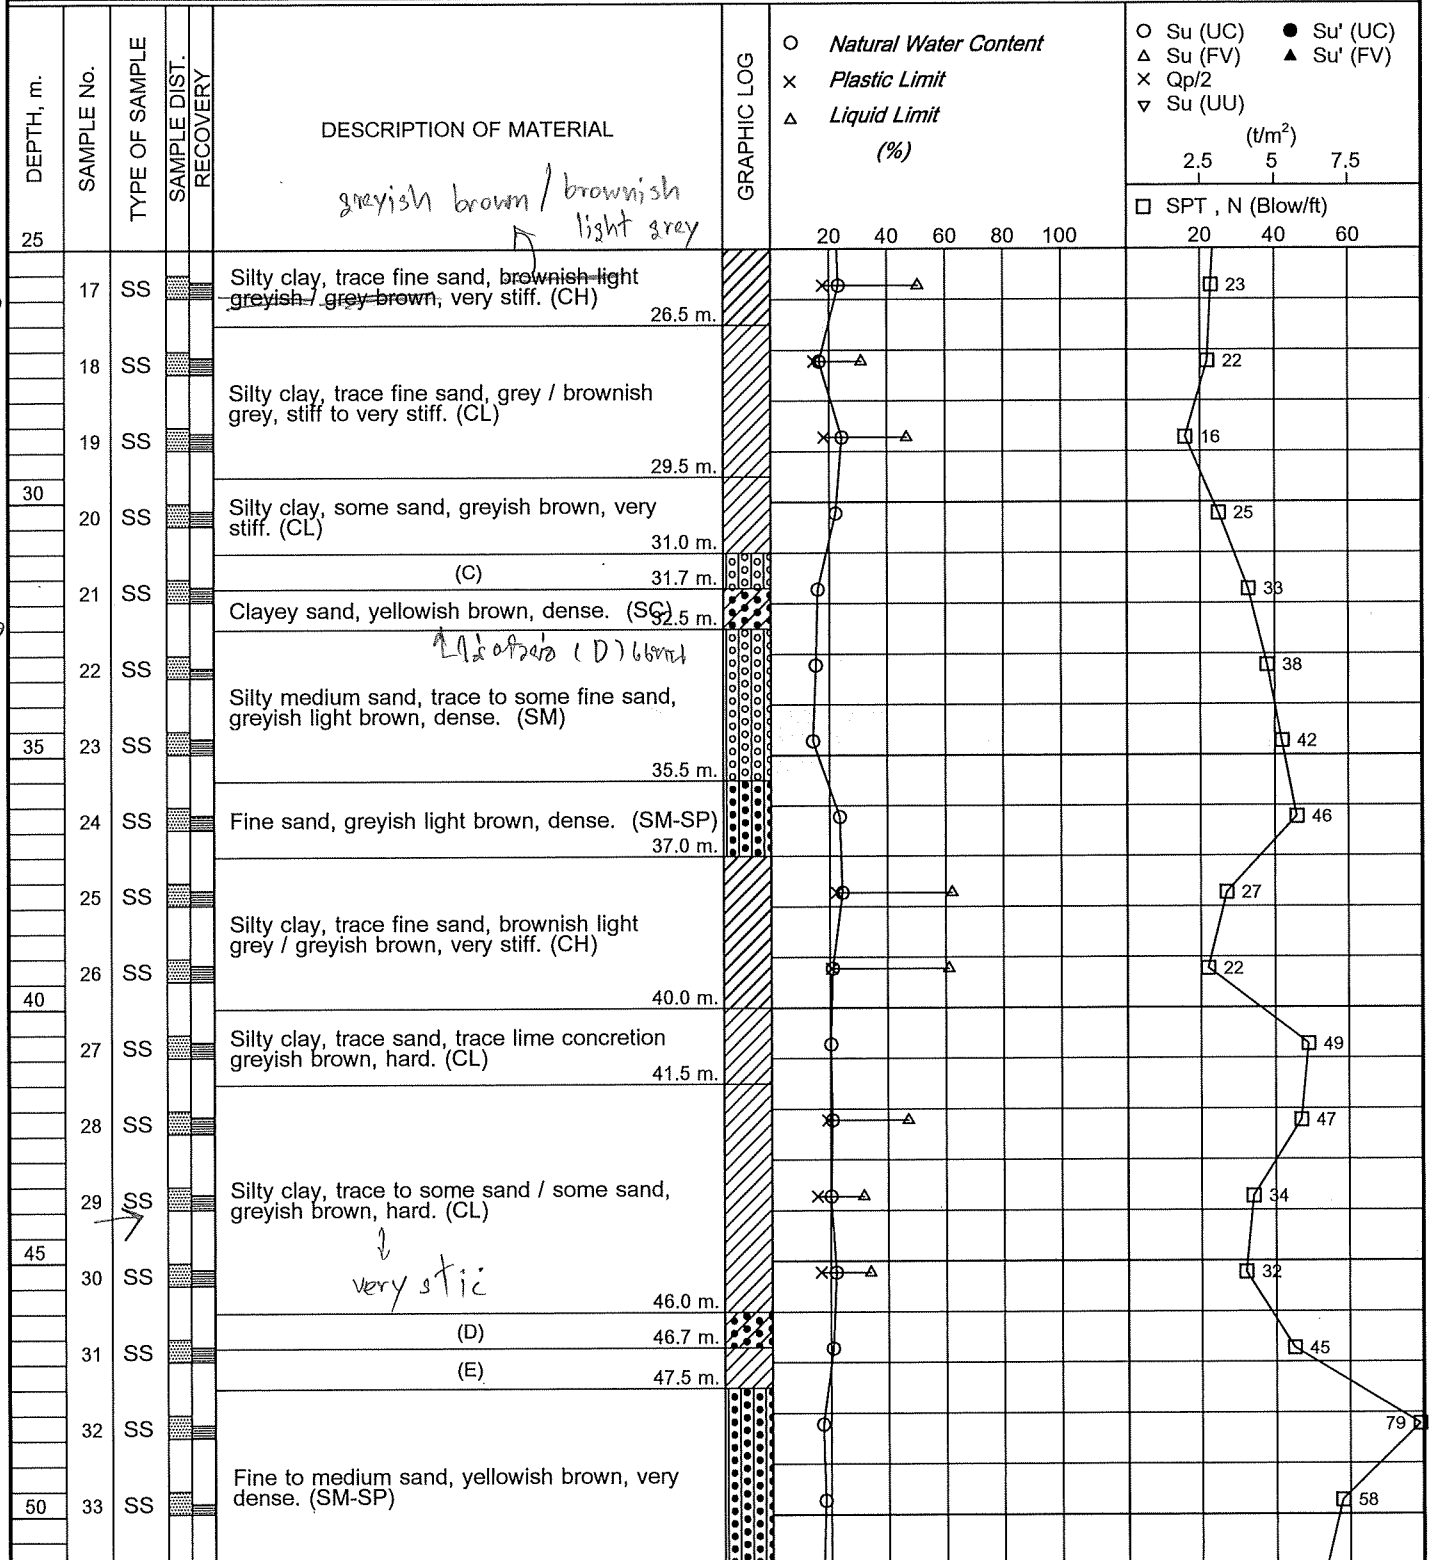

BORING STARTED : 02/10/00

RIG. ACKER

WL. -9.00 m

24 Hrs. After Boring

BORING FINISHED : 06/09/24

FOREMAN : WN.


JOB No. : 1167287

LOG OF BORING No. OW-43

PROJECT : MRT Orange Line Project : Bang Khun Non -

LOCATION : Bangkok

Min Buri (Suwinthawong) Section

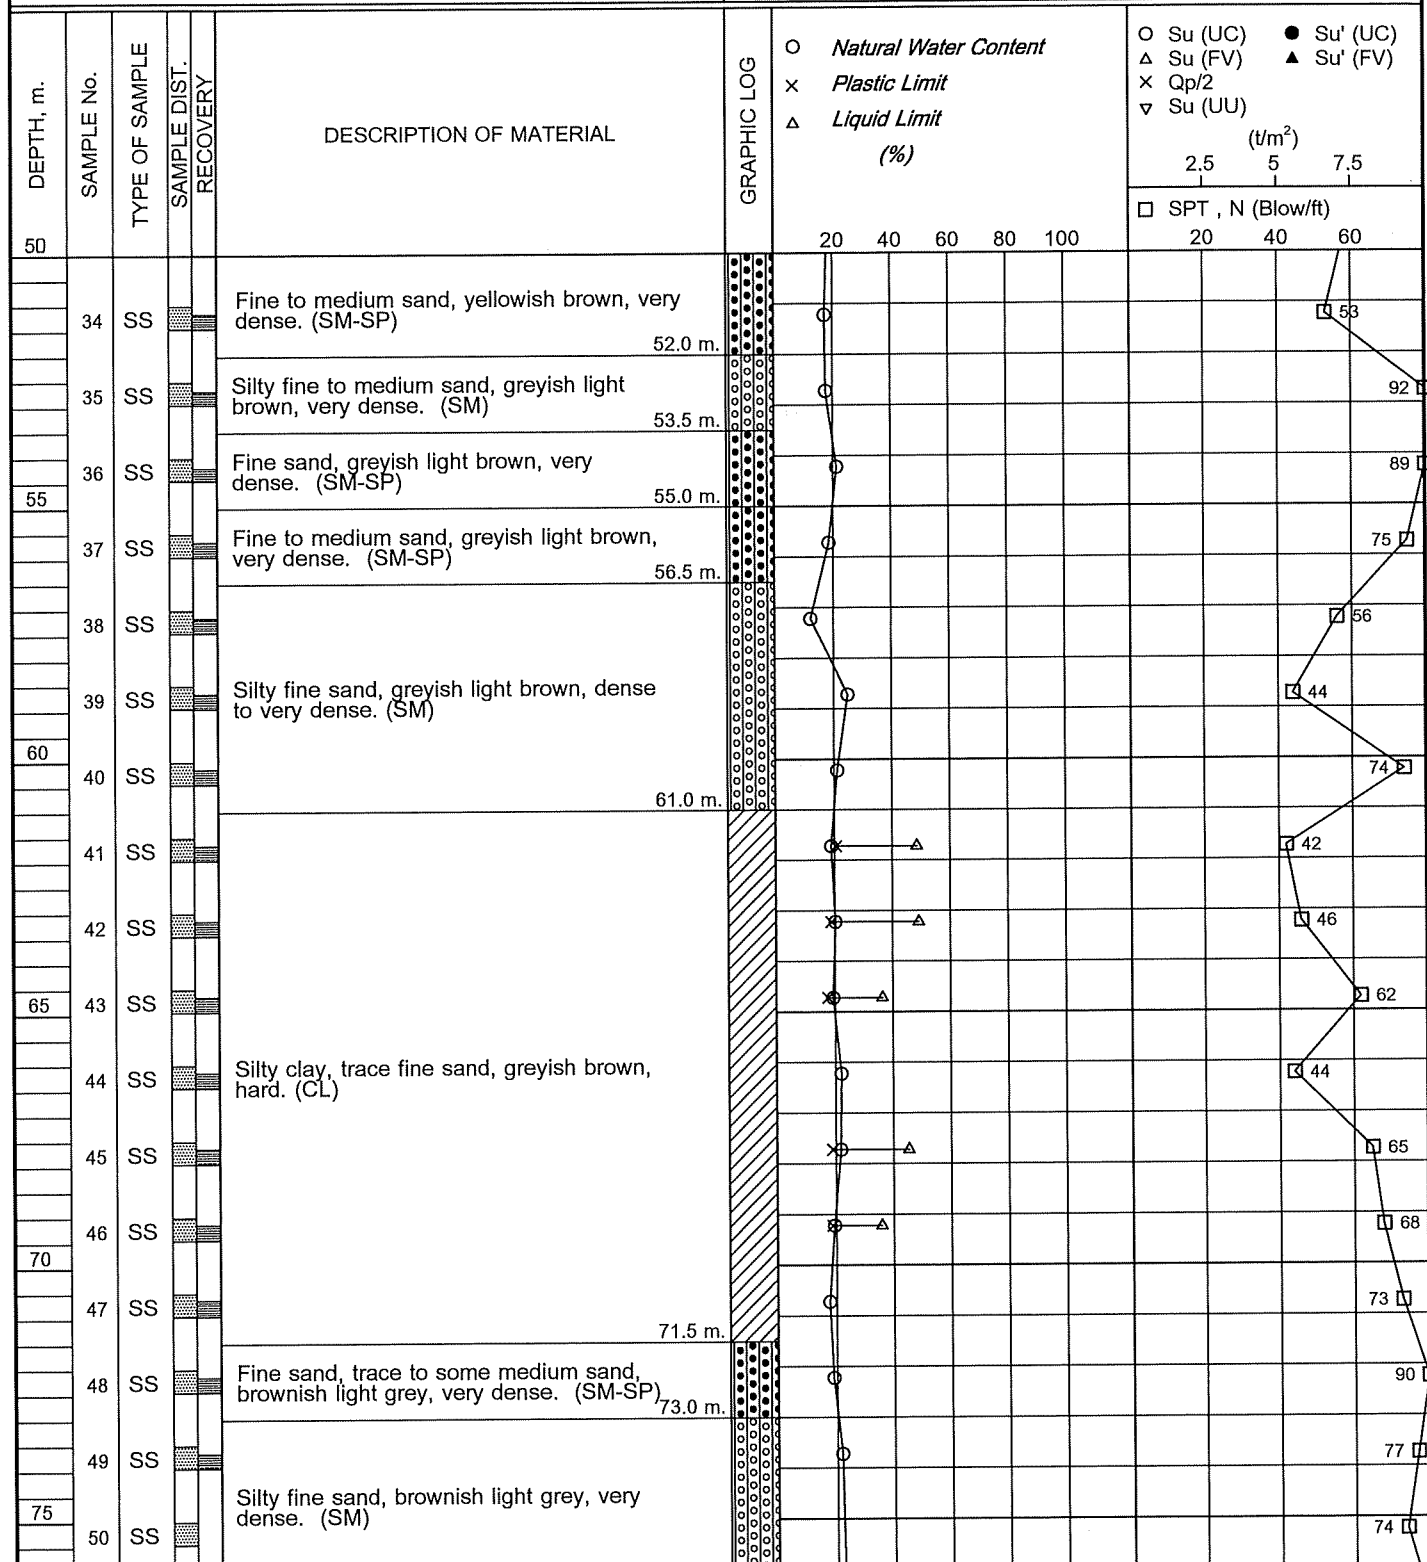

BORING STARTED : 02/10/00

RIG. ACKER

WL.

9.00 m

24 Hrs.
After Boring

BORING FINISHED : 06/09/24

FOREMAN : WN.


JOB No. : 1167287

LOG OF BORING No. OW-43

PROJECT : MRT Orange Line Project : Bang Khun Non -

LOCATION : Bangkok

Min Buri (Suwinthawong) Section

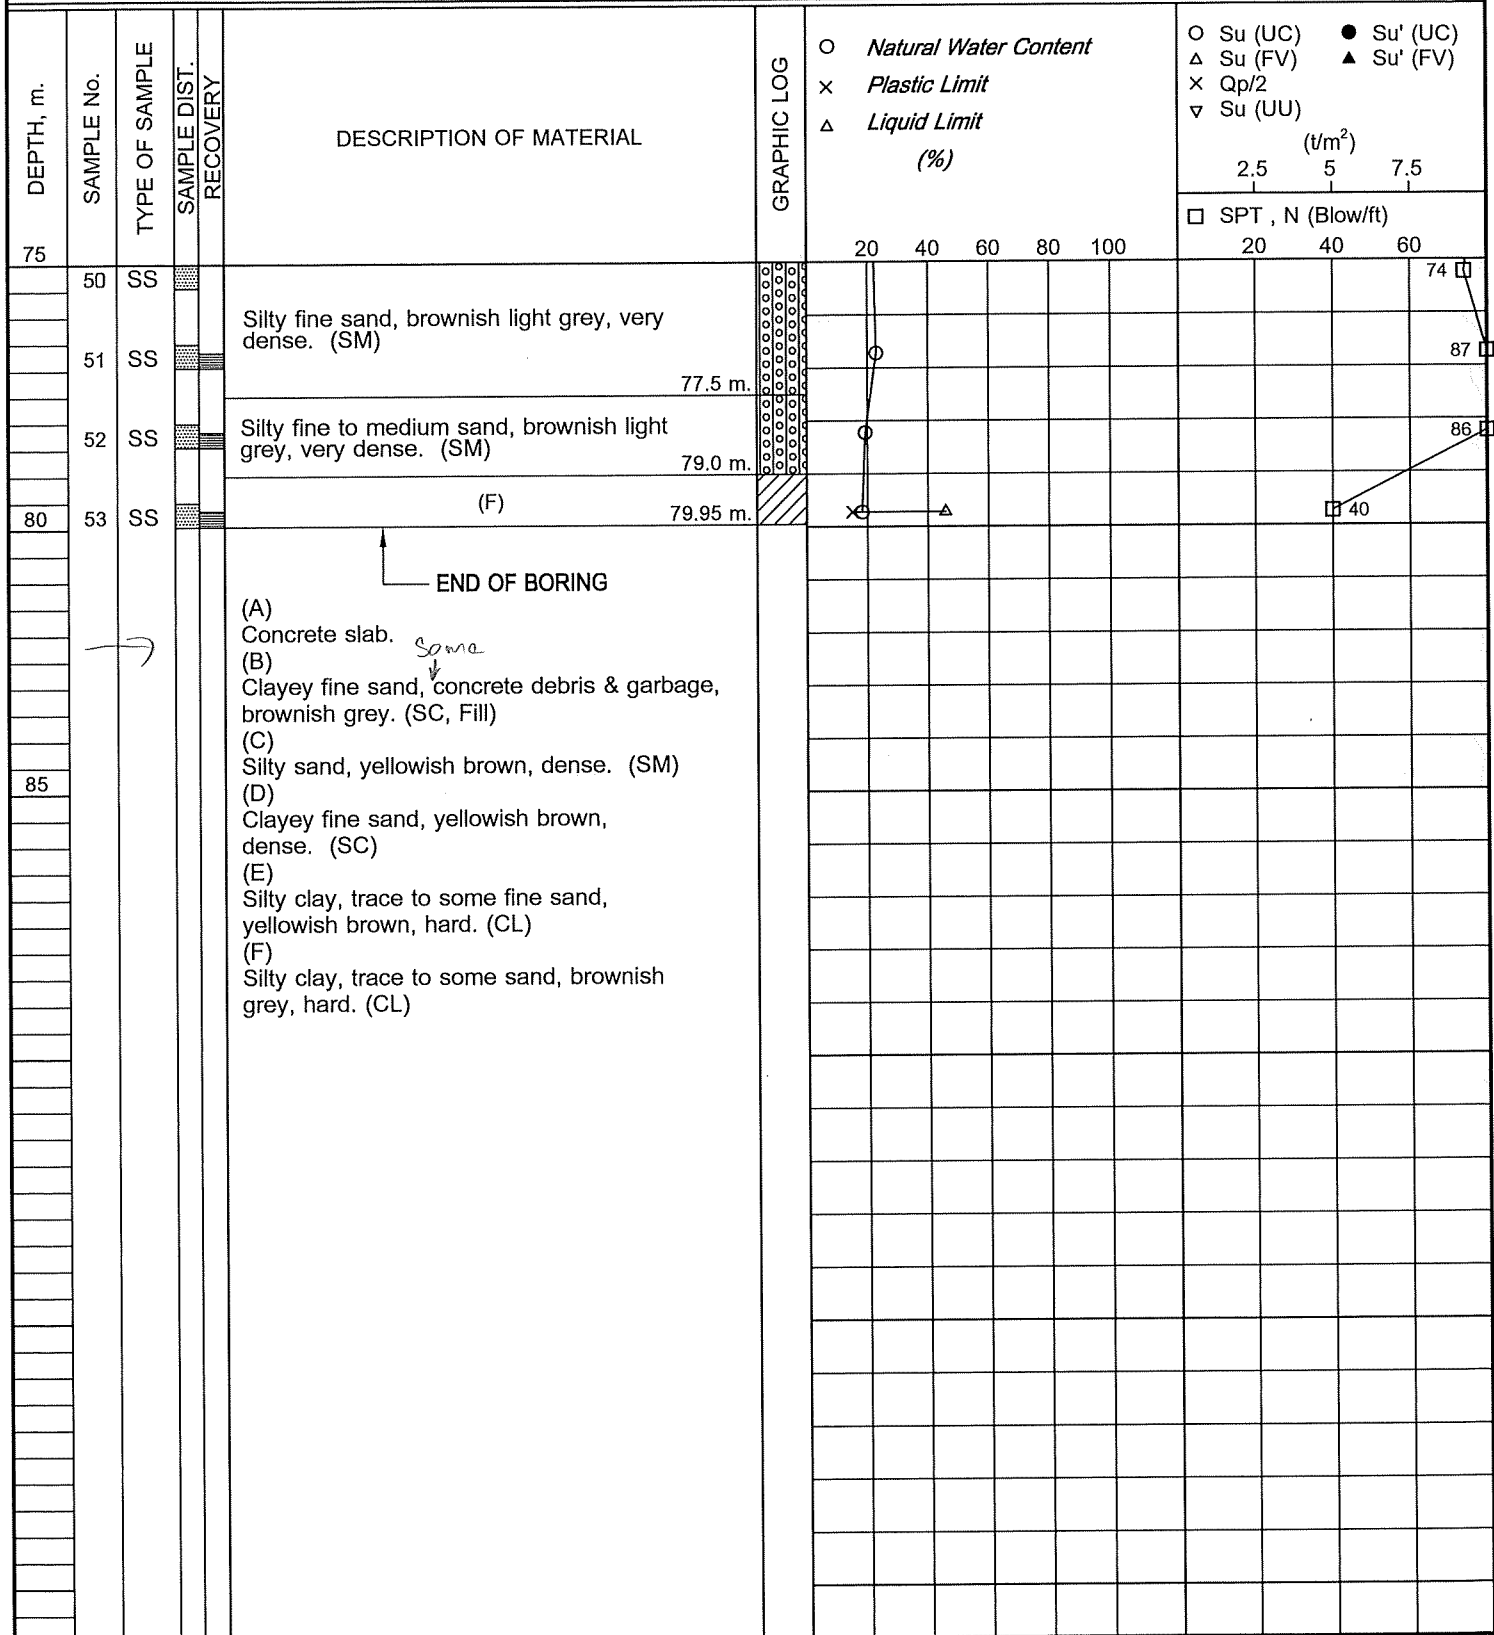

BORING STARTED : 02/10/00

RIG. ACKER

WL. -9.00 m 24 Hrs. After Boring

BORING FINISHED : 06/09/24

FOREMAN : WN.

JOB No. : 1167287