


LOG OF BORING No. OW-44

PROJECT : MRT Orange Line Project : Bang Khun Non -

LOCATION : Bangkok

Min Buri (Suwinthawong) Section

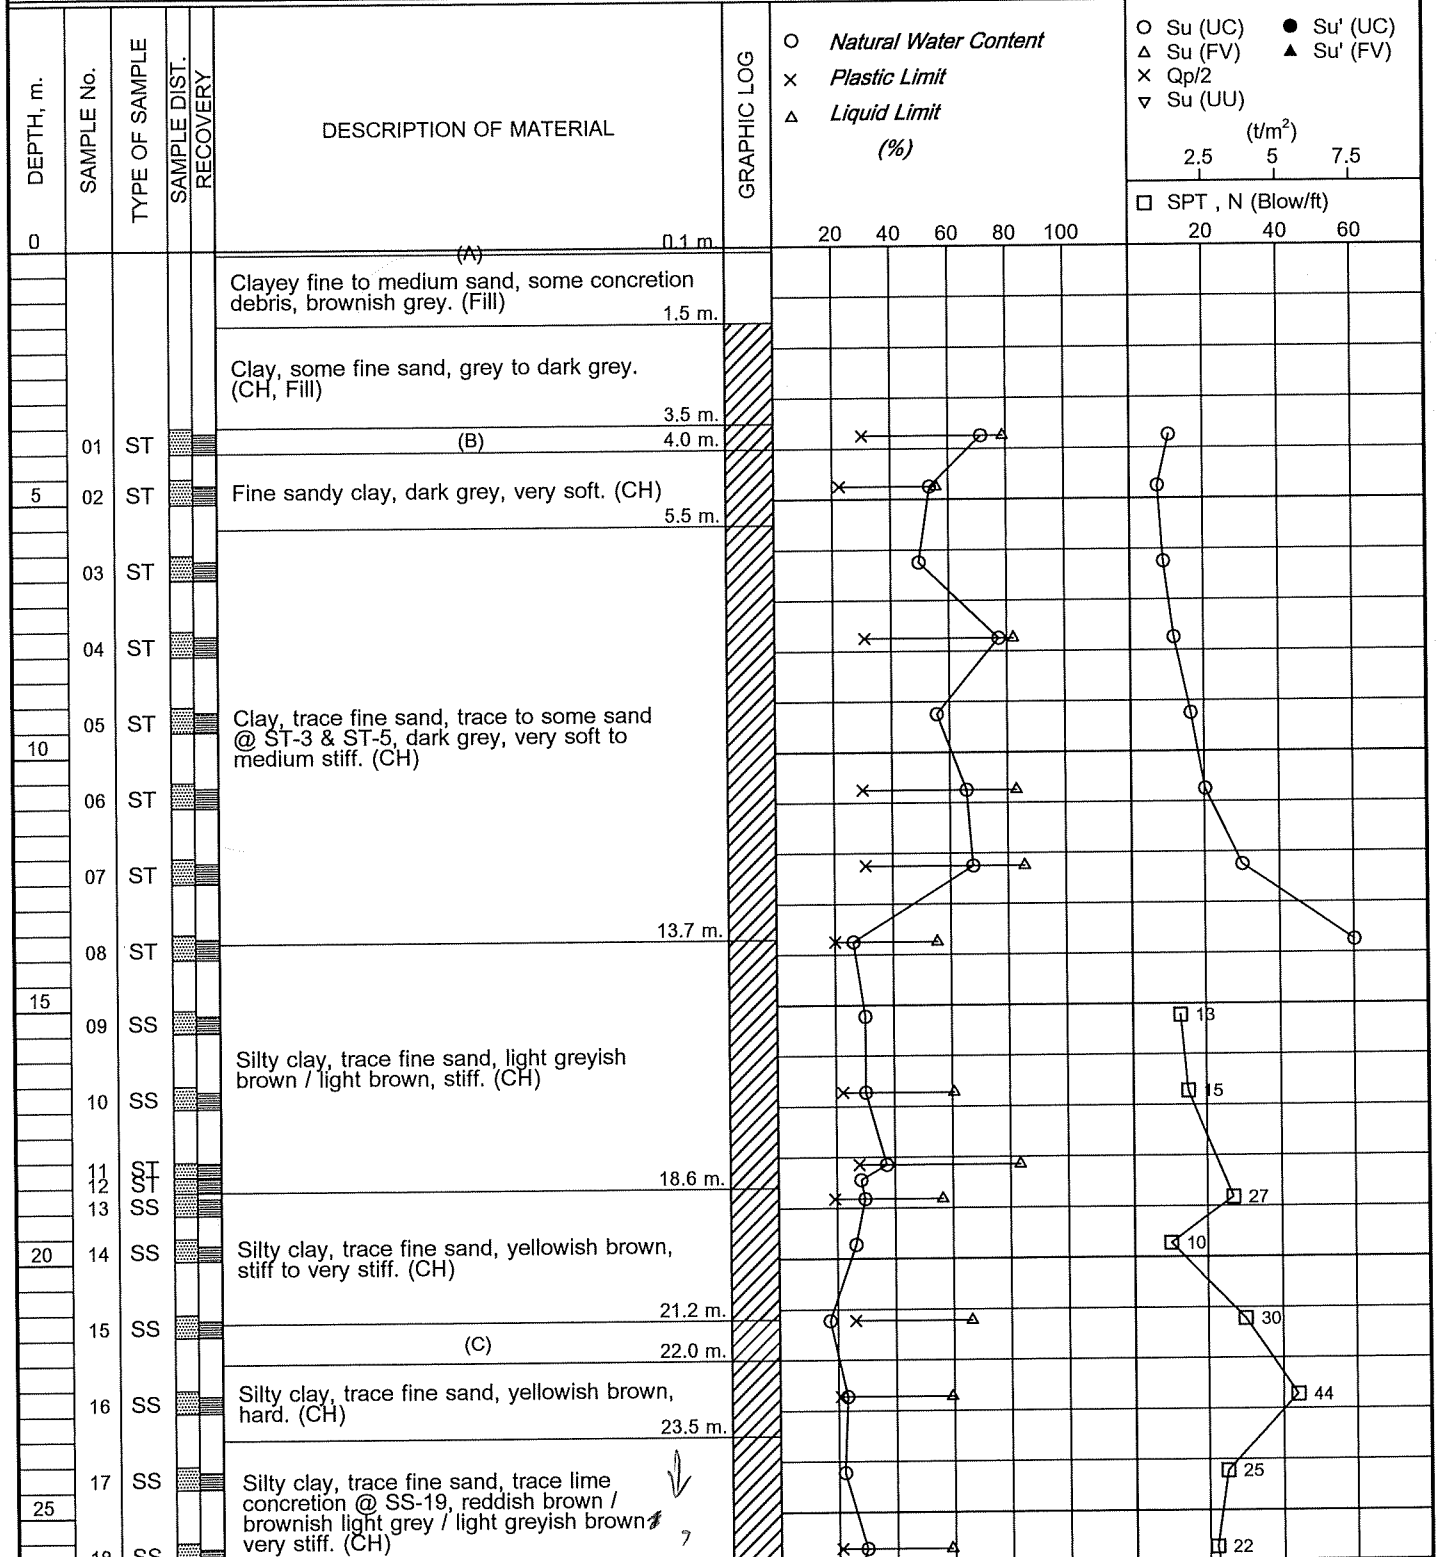

BORING STARTED : 16/10/24

RIG. Big no 35

WL. ~~-3.50~~ -9.60 m 24 Hrs. After Boring

BORING FINISHED : 20/10/24

FOREMAN : WN.


JOB No. : 1167287

LOG OF BORING No. OW-44

PROJECT : MRT Orange Line Project : Bang Khun Non -

LOCATION : Bangkok

Min Buri (Suwinthawong) Section

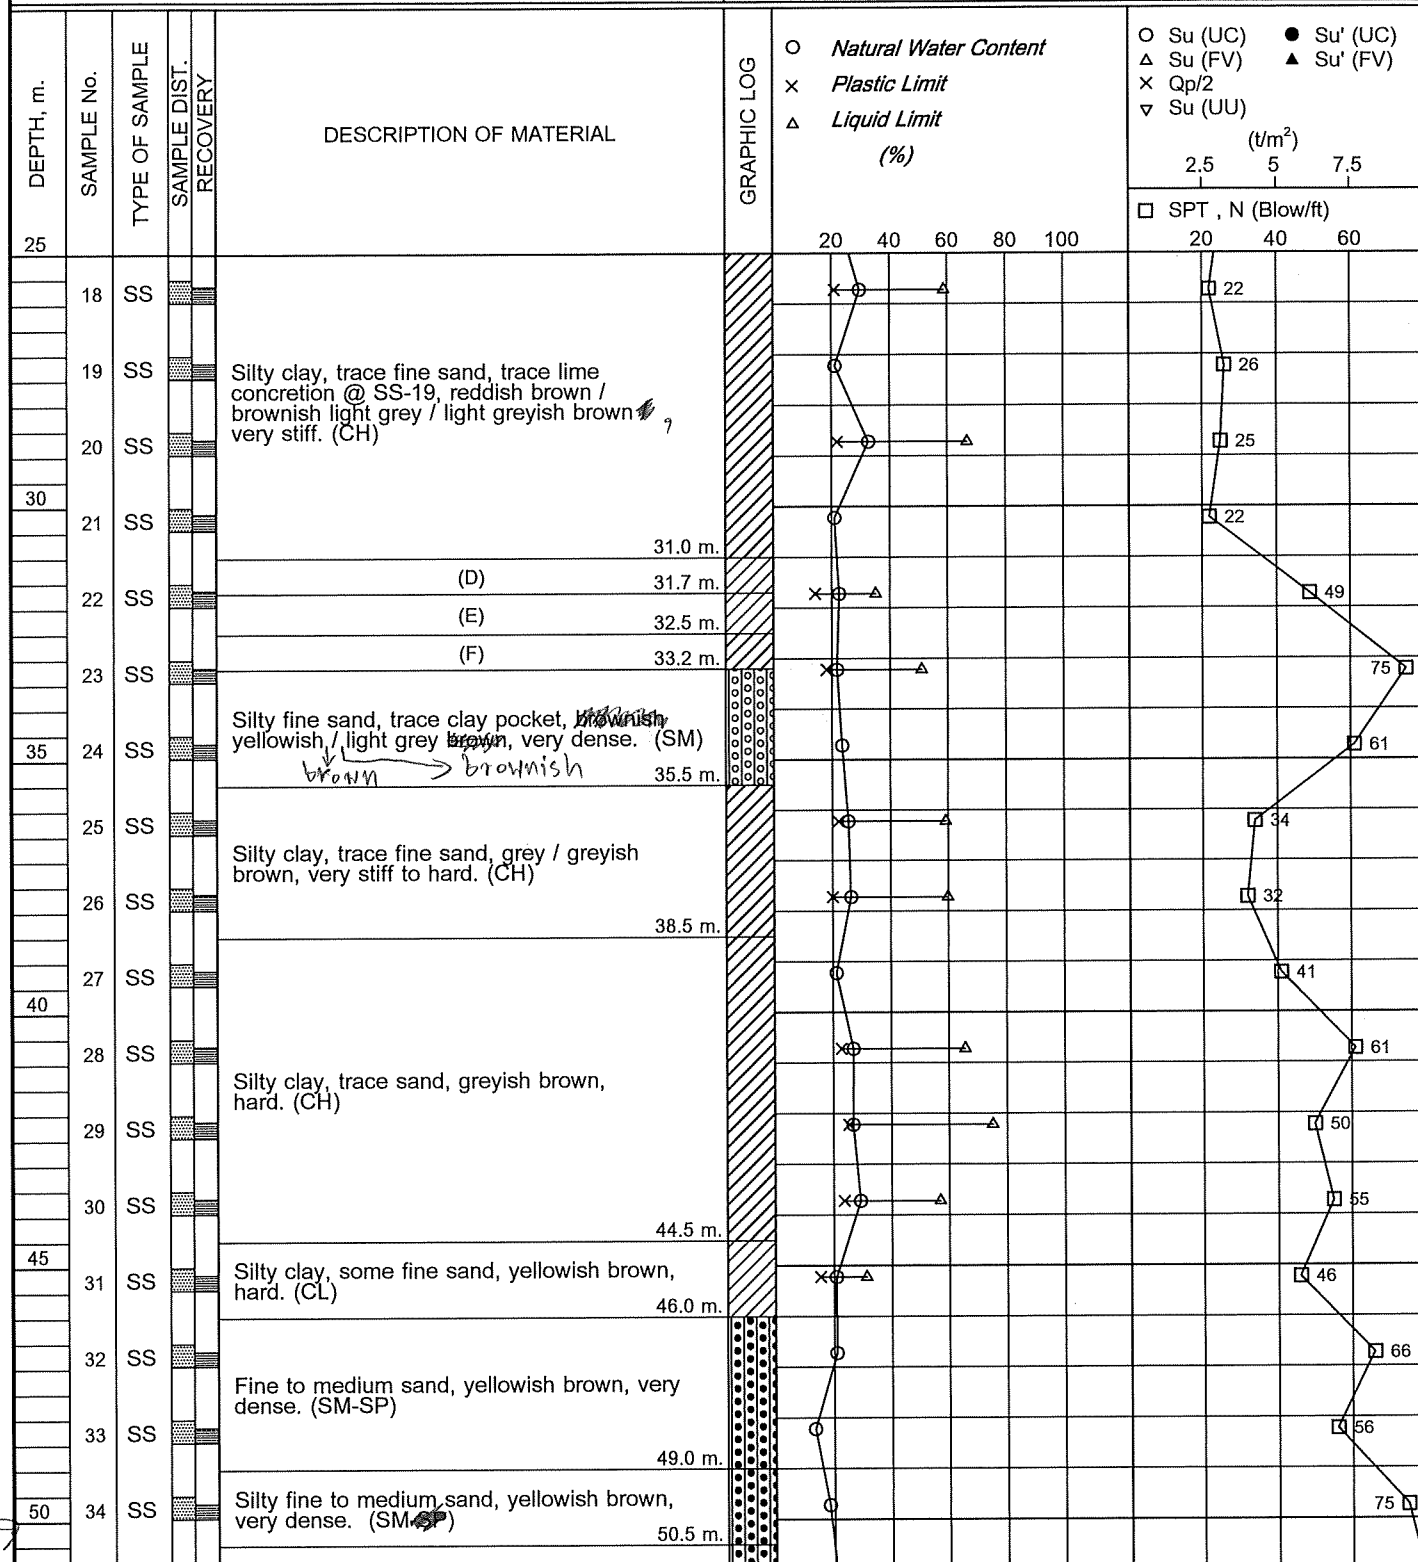

BORING STARTED : 16/10/24

RIG. Big no 35

WL. -3.50
-9.60 m 24 Hrs. After Boring

BORING FINISHED : 20/10/24

FOREMAN : WN.


JOB No. : 1167287

LOG OF BORING No. OW-44

PROJECT : MRT Orange Line Project : Bang Khun Non -

LOCATION : Bangkok

Min Buri (Suwinthawong) Section

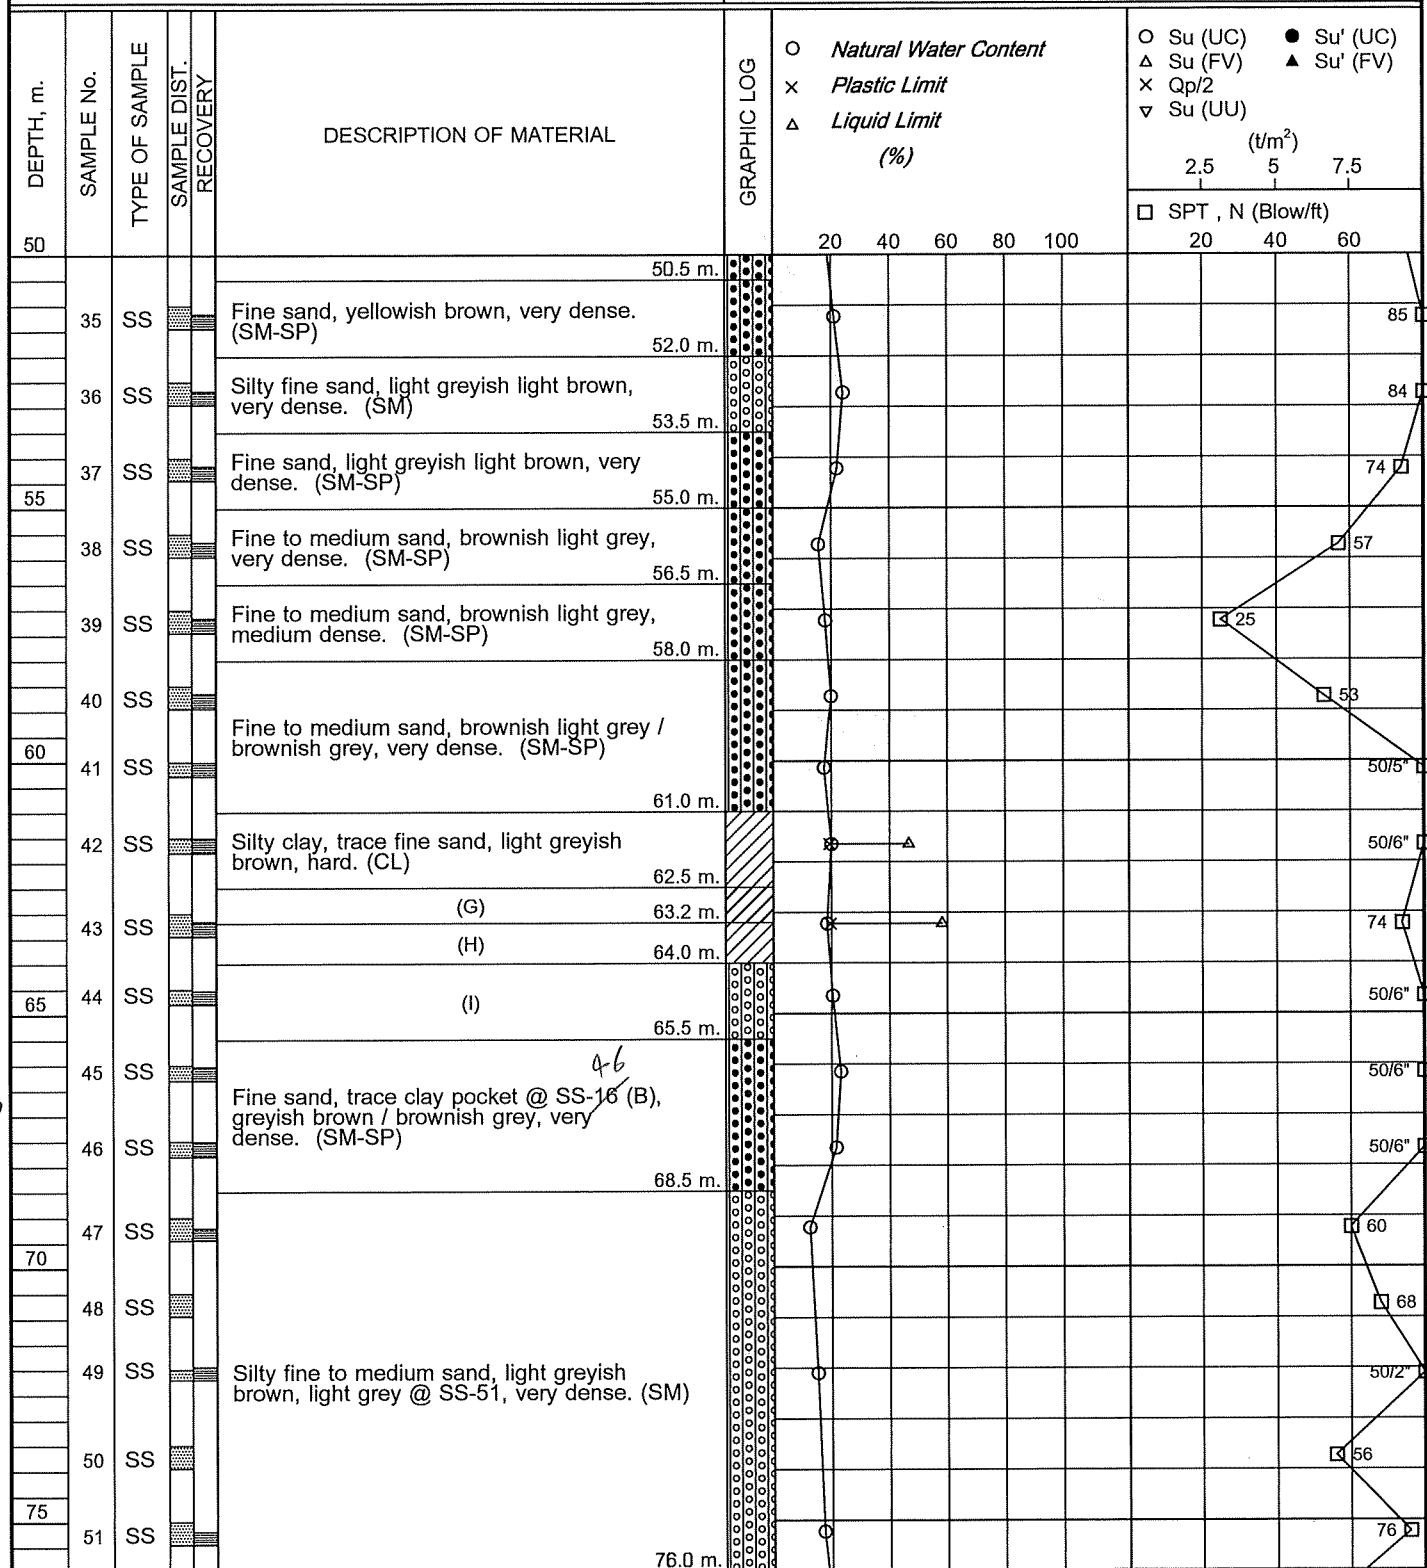

BORING STARTED : 16/10/24

RIG. Big no 35

WL. ^{-3.50}
~~-9.00~~ m 24 Hrs. After Boring

BORING FINISHED : 20/10/24

FOREMAN : WN.

JOB No. : 1167287

LOG OF BORING No. OW-44

PROJECT : MRT Orange Line Project : Bang Khun Non -

LOCATION : Bangkok

Min Buri (Suwinthawong) Section

DEPTH, m.	SAMPLE No.	TYPE OF SAMPLE	SAMPLE DIST. RECOVERY	DESCRIPTION OF MATERIAL	GRAPHIC LOG	○ Natural Water Content × Plastic Limit △ Liquid Limit (%) ○ Su (UC) ● Su' (UC) △ Su (FV) ▲ Su' (FV) × Qp/2 ▽ Su (UU) (t/m²) 2.5 5 7.5 □ SPT, N (Blow/ft) 20 40 60
-----------	------------	----------------	-----------------------	-------------------------	-------------	---



BORING STARTED : 16/10/24

RIG. Big no 35

WL. ^{-3.50}
-9.60 m 24 Hrs. After Boring

BORING FINISHED : 20/10/24

FOREMAN : WN.

JOB No. : 1167287