


LOG OF BORING No. OW-45

PROJECT : MRT Orange Line Project : Bang Khun Non -

LOCATION : Bangkok

Min Buri (Suwinthawong) Section

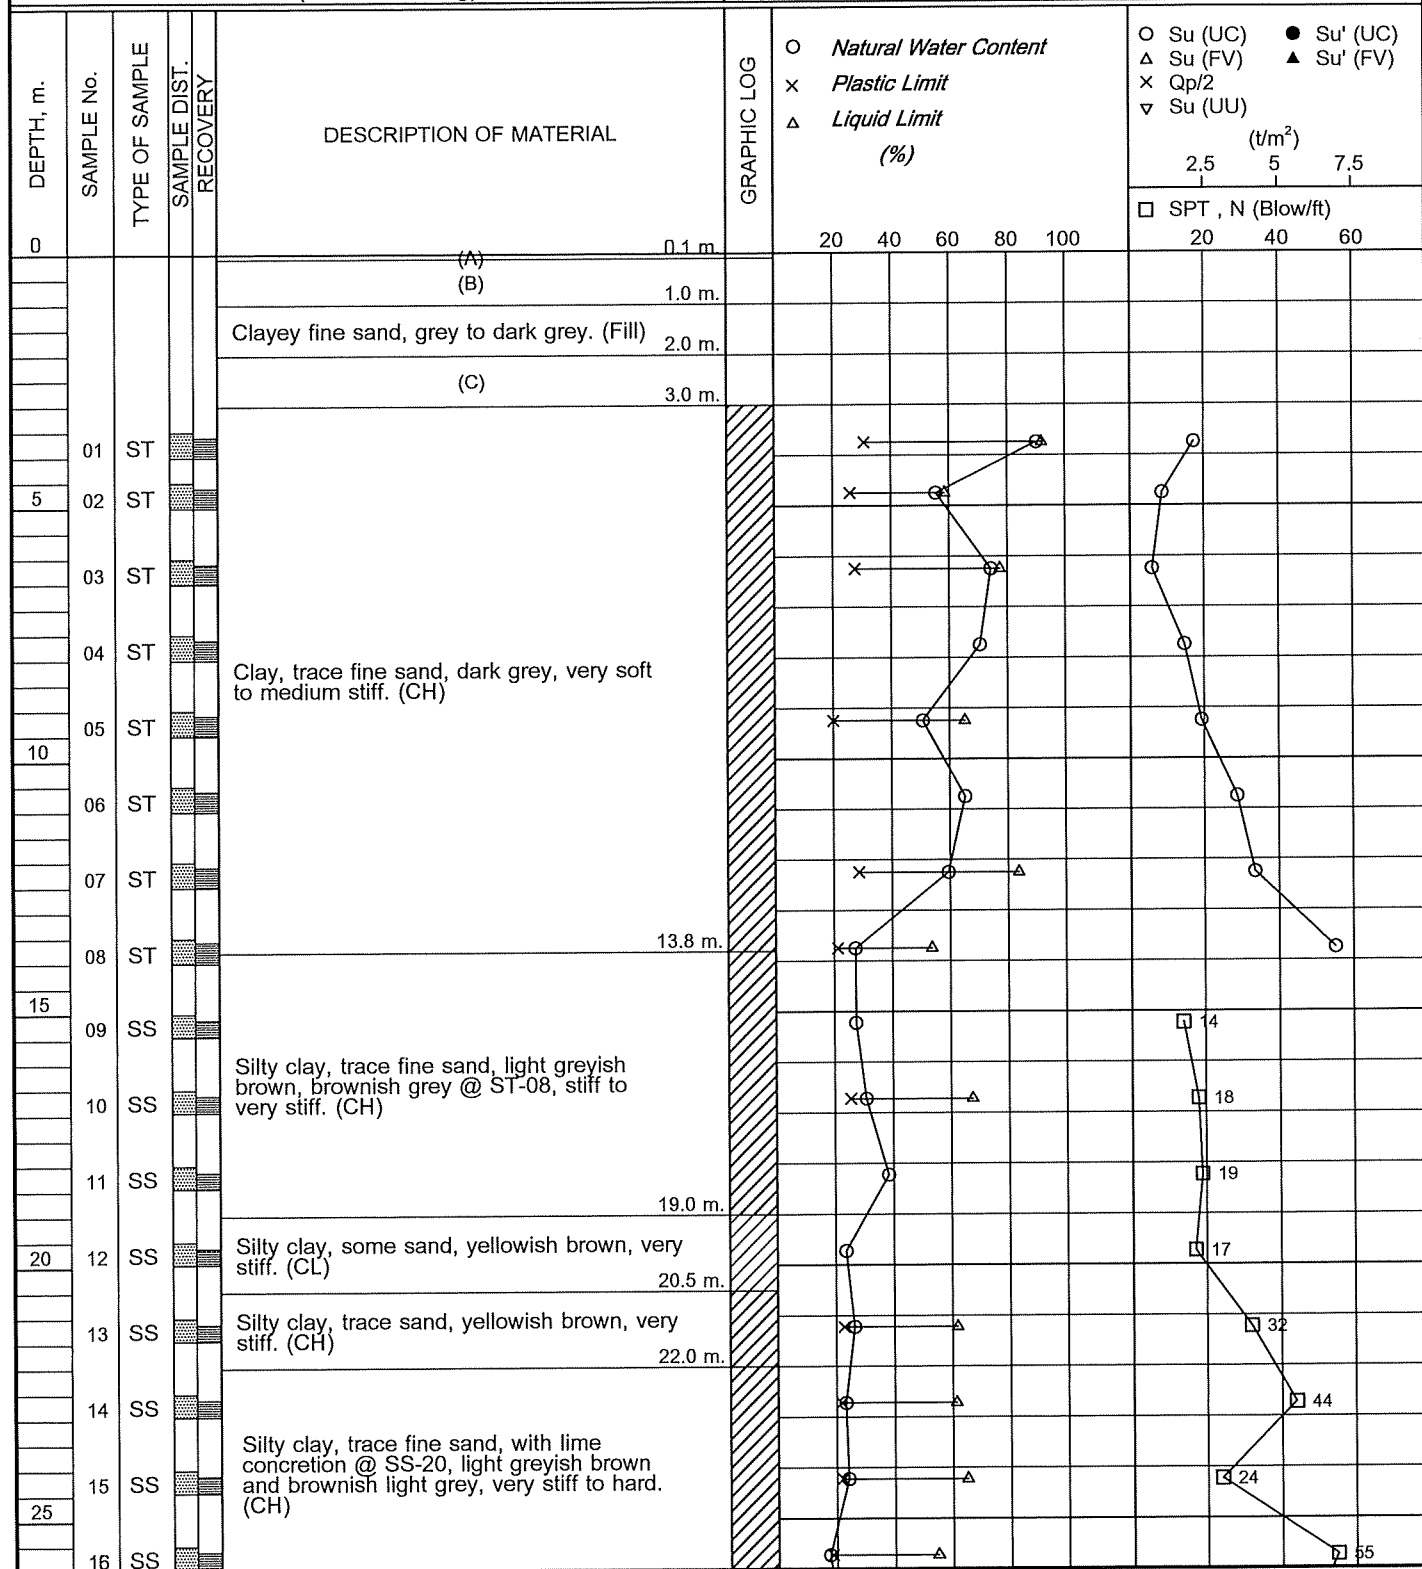

BORING STARTED : 24/10/24

RIG. ACKER

WL. -3.00 m 24 Hrs. After Boring

BORING FINISHED : 28/10/24

FOREMAN : WN.


JOB No. : 1167287

LOG OF BORING No. OW-45

PROJECT : MRT Orange Line Project : Bang Khun Non -

LOCATION : Bangkok

Min Buri (Suwinthawong) Section

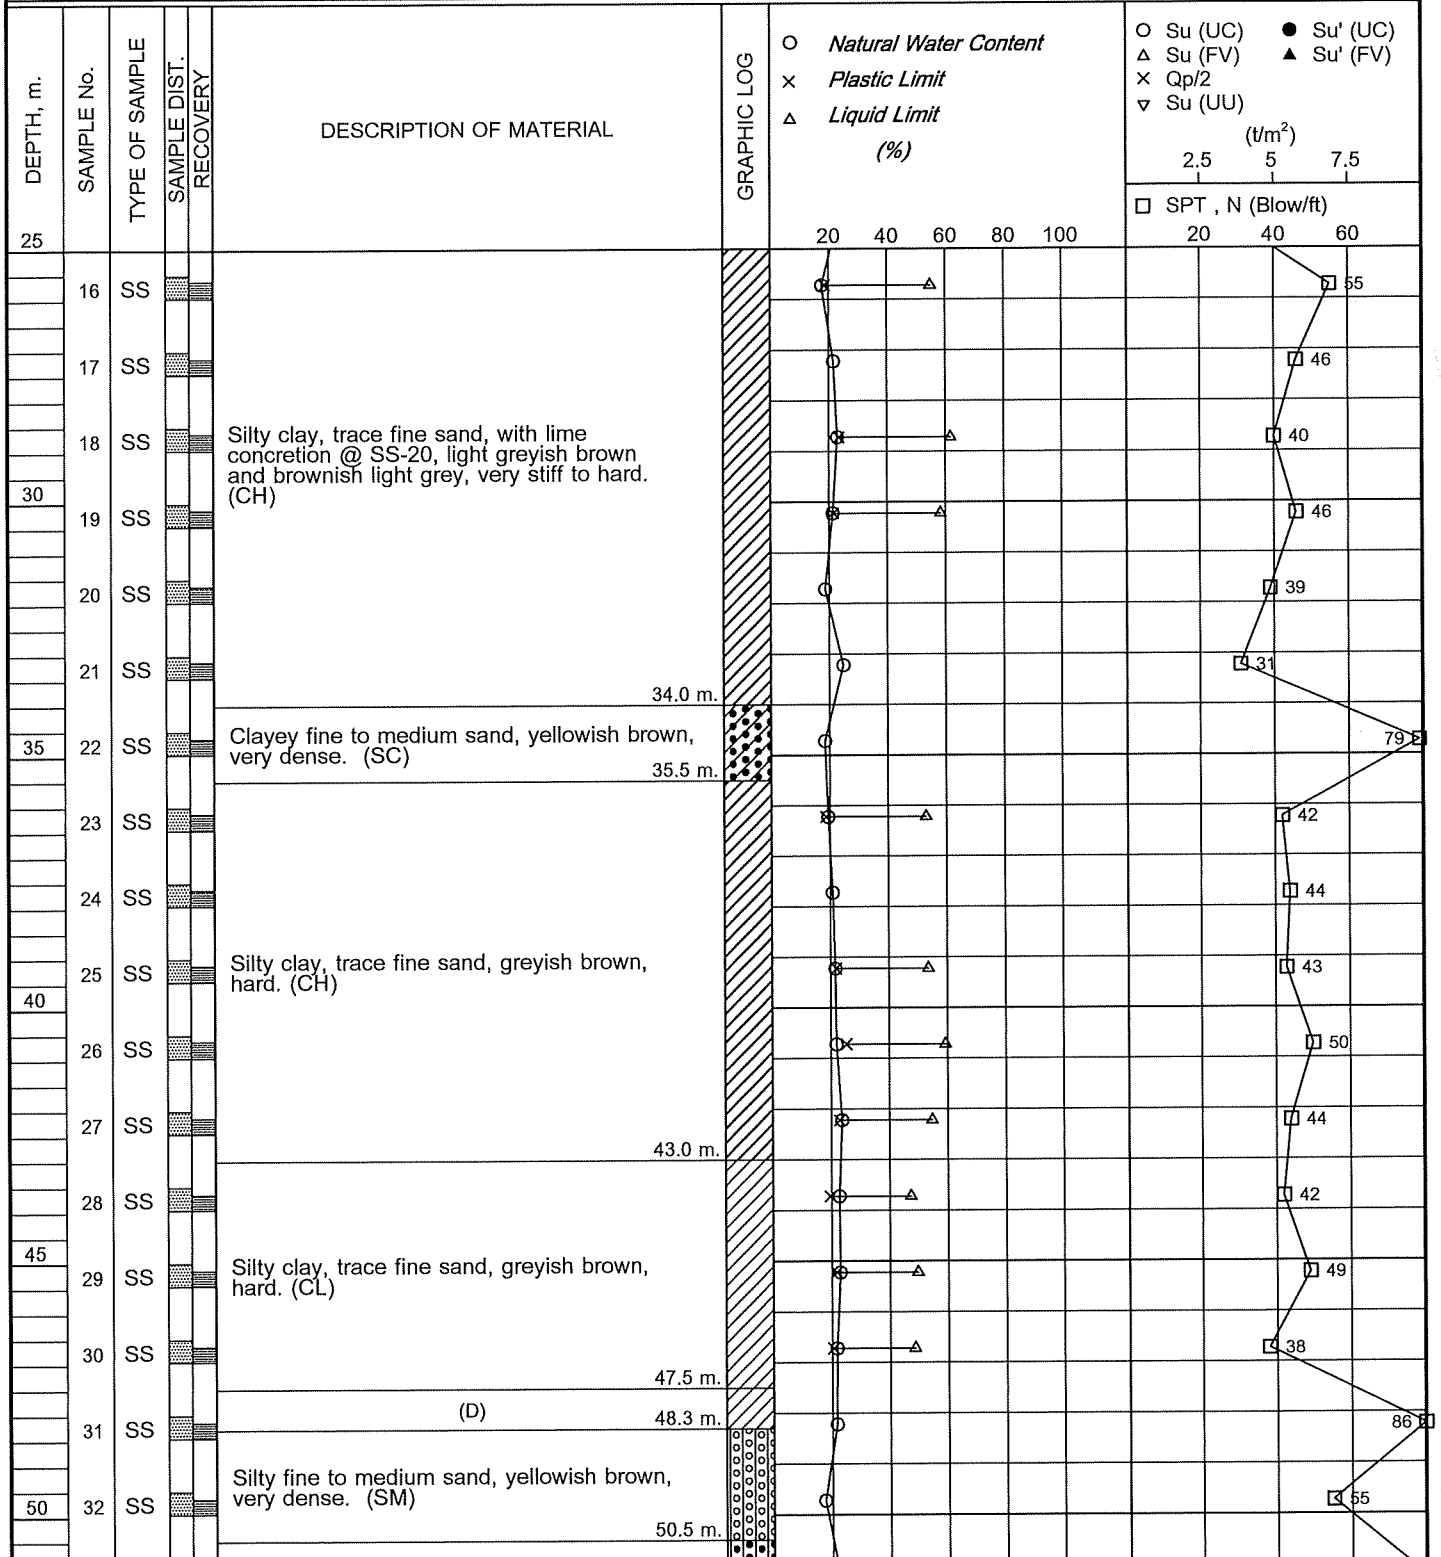

BORING STARTED : 24/10/24

RIG. ACKER

WL. -3.00 m 24 Hrs. After Boring

BORING FINISHED : 28/10/24

FOREMAN : WN.


JOB No. : 1167287

LOG OF BORING No. OW-45

PROJECT : MRT Orange Line Project : Bang Khun Non -

LOCATION : Bangkok

Min Buri (Suwinthawong) Section

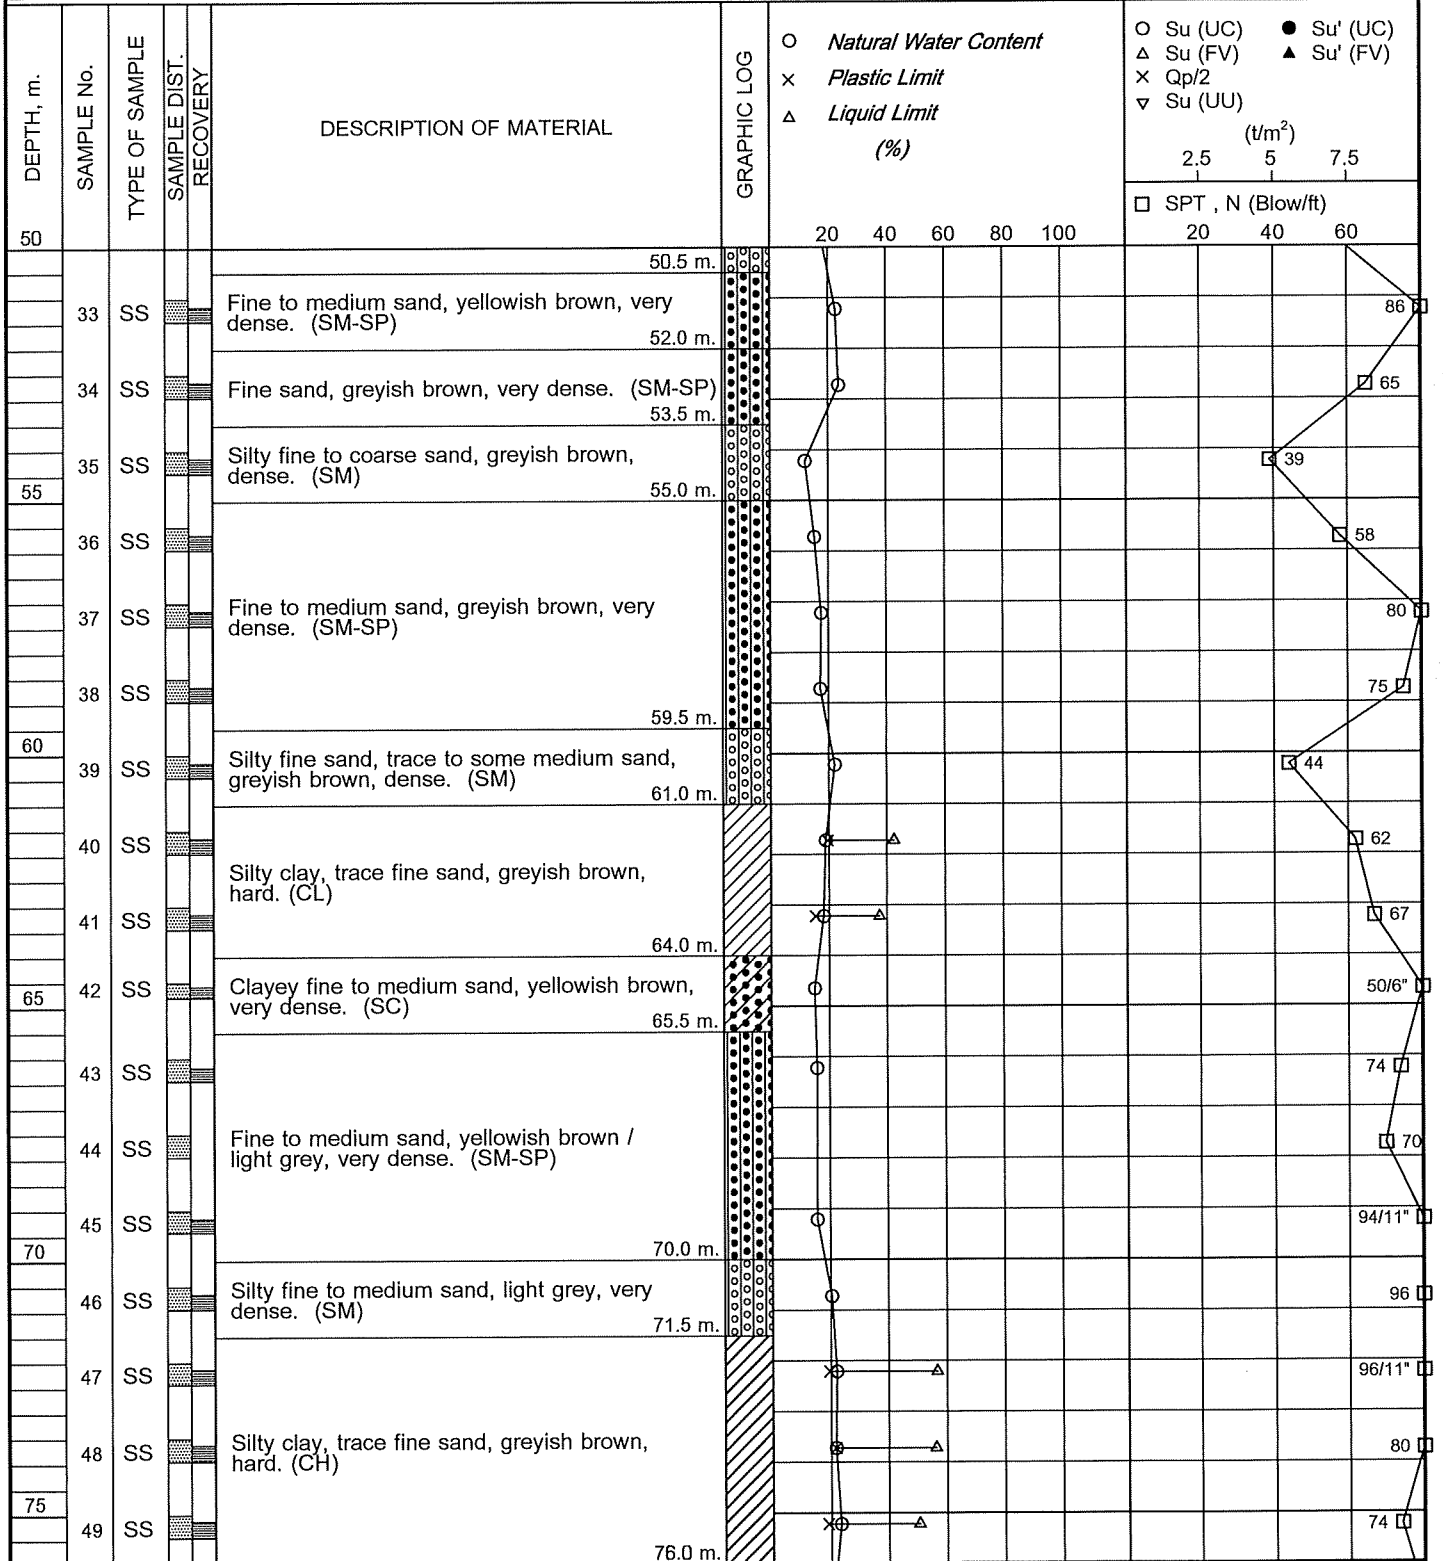

BORING STARTED : 24/10/24

RIG. ACKER

WL. -3.00 m

24 Hrs.
After Boring

BORING FINISHED : 28/10/24

FOREMAN : WN.

JOB No. : 1167287

LOG OF BORING No. OW-45

PROJECT : MRT Orange Line Project : Bang Khun Non -

LOCATION : Bangkok

Min Buri (Suwinthawong) Section

DEPTH, m.	SAMPLE No.	TYPE OF SAMPLE	SAMPLE DIST. RECOVERY	DESCRIPTION OF MATERIAL	GRAPHIC LOG	○ <i>Natural Water Content</i> × <i>Plastic Limit</i> △ <i>Liquid Limit (%)</i> ○ Su (UC) ● Su' (UC) △ Su (FV) ▲ Su' (FV) × Qp/2 ▽ Su (UU) (t/m²) 2.5 5 7.5 □ SPT, N (Blow/ft) 20 40 60
75						
	49	SS				
				76.0 m.		
	50	SS				
	51	SS		Silty clay, trace sand, trace lime concretion @ SS-50, greyish brown, hard. (CL)		
	52	SS				
80				79.95 m.		
				END OF BORING		
				(A) Concrete plate.		
				(B) Silty fine to medium sand, greyish brown. (Fill)		
				(C) Clay, trace fine sand, with decayed wood, dark brownish grey to dark grey. (Fill)		
85				(D) Silty clay, some sand, yellowish brown, hard. (CL)		



BORING STARTED : 24/10/24

RIG. ACKER

WL. -3.00 m 24 Hrs. After Boring

BORING FINISHED : 28/10/24

FOREMAN : WN.

JOB No. : 1167287