


LOG OF BORING No. OW-47

PROJECT : MRT Orange Line Project : Bang Khun Non -

LOCATION : Bangkok

Min Buri (Suwinthawong) Section

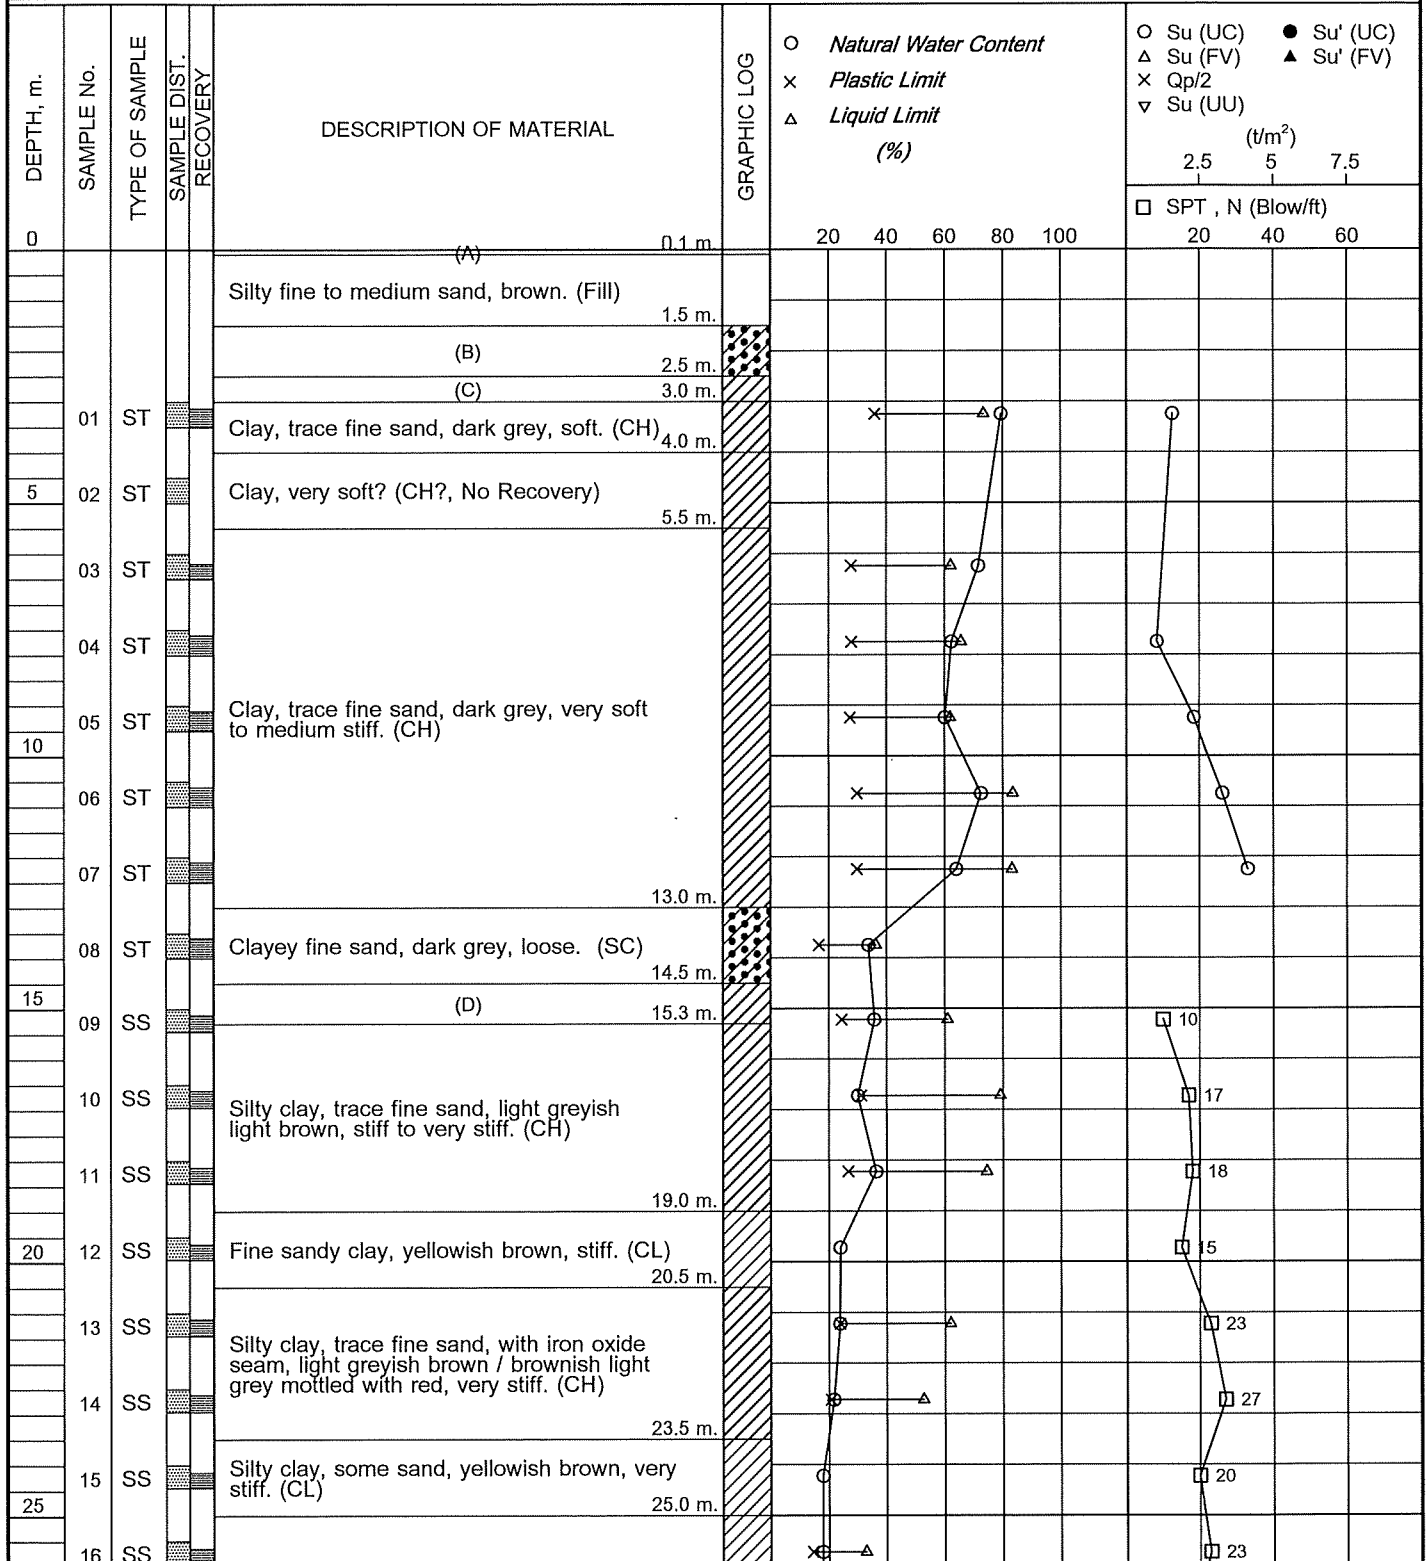

BORING STARTED : 13/11/24

RIG. ACKER

WL. -2.00 m 24 Hrs. After Boring

BORING FINISHED : 17/11/24

FOREMAN : WN.


JOB No. : 1167287

LOG OF BORING No. OW-47

PROJECT : MRT Orange Line Project : Bang Khun Non -

LOCATION : Bangkok

Min Buri (Suwinthawong) Section

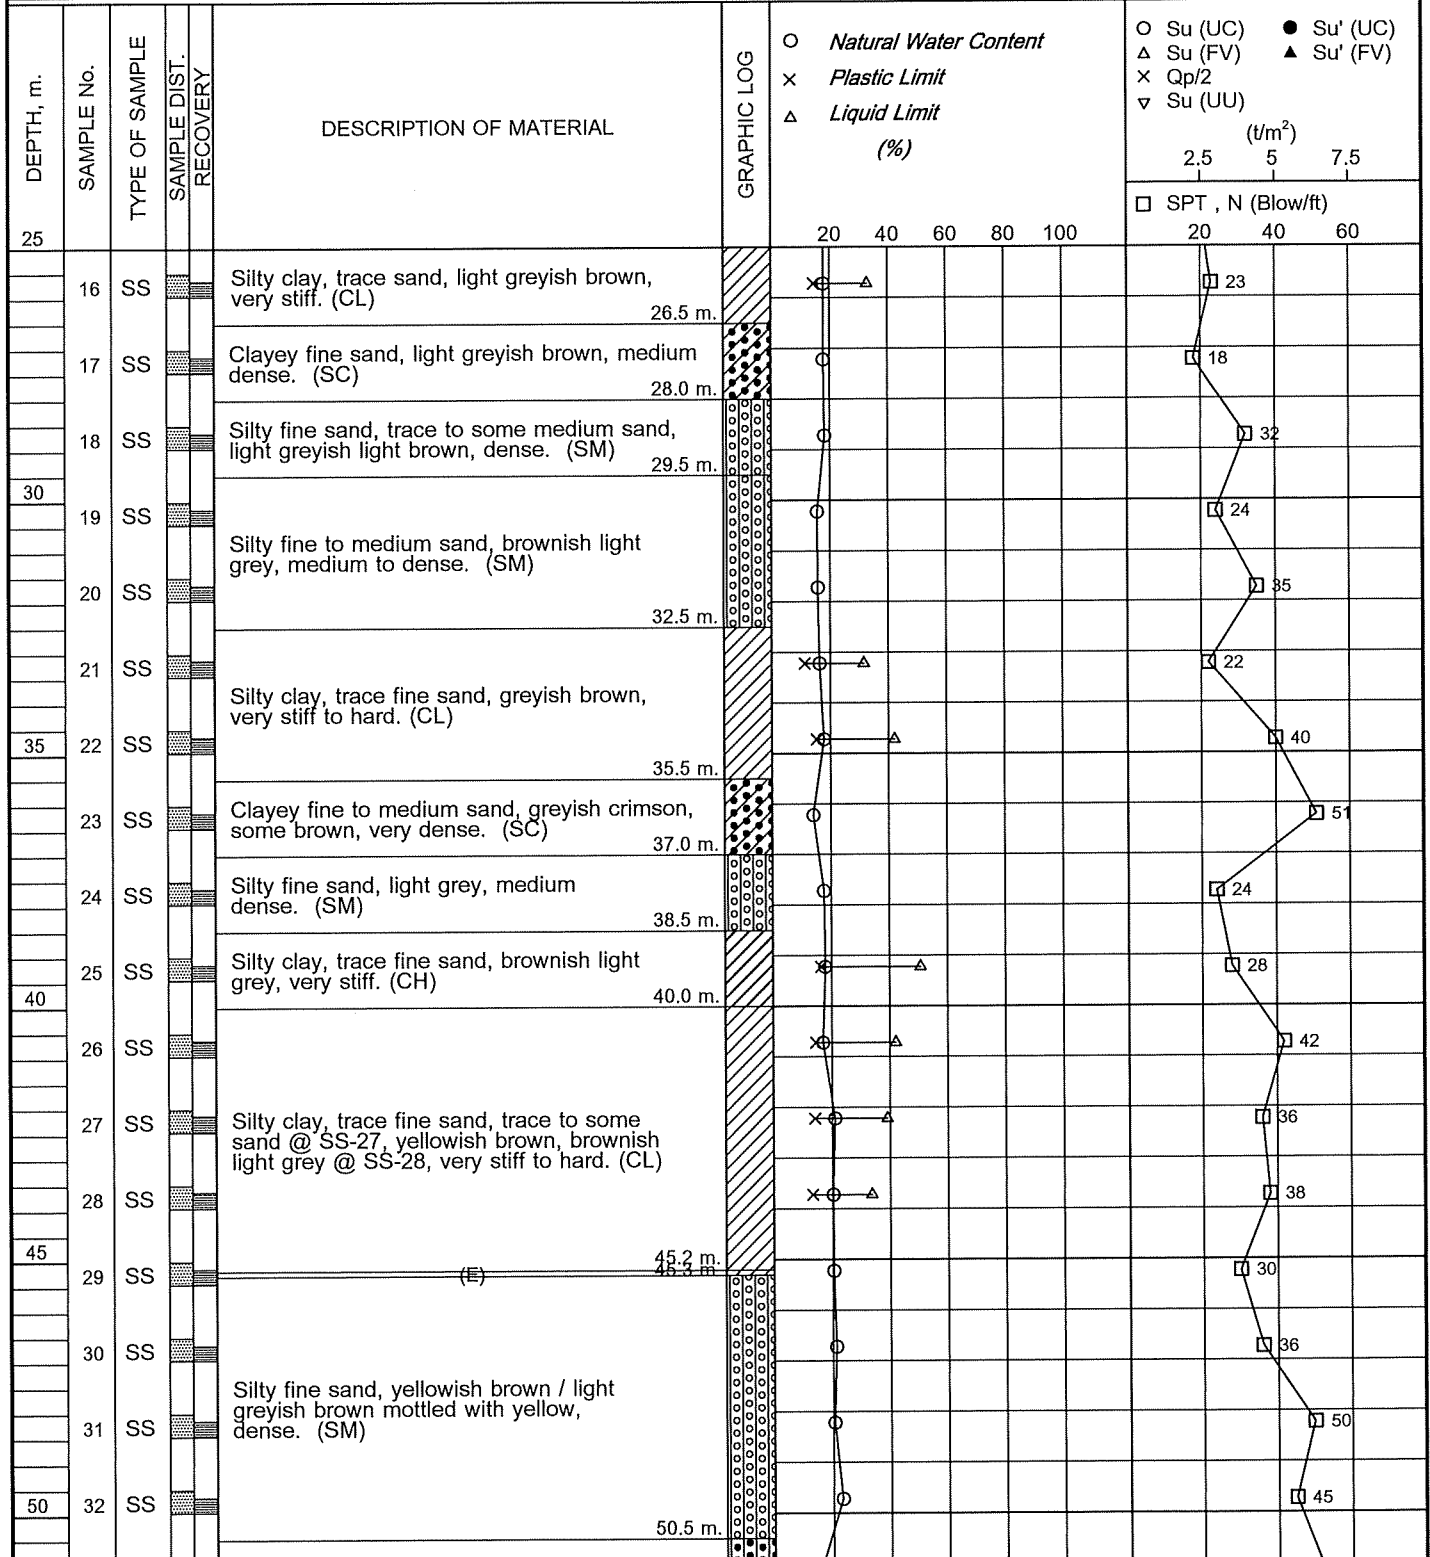

BORING STARTED : 13/11/24

RIG. ACKER

WL. -2.00 m 24 Hrs. After Boring

BORING FINISHED : 17/11/24

FOREMAN : WN.


JOB No. : 1167287

LOG OF BORING No. OW-47

PROJECT : MRT Orange Line Project : Bang Khun Non -

LOCATION : Bangkok

Min Buri (Suwinthawong) Section

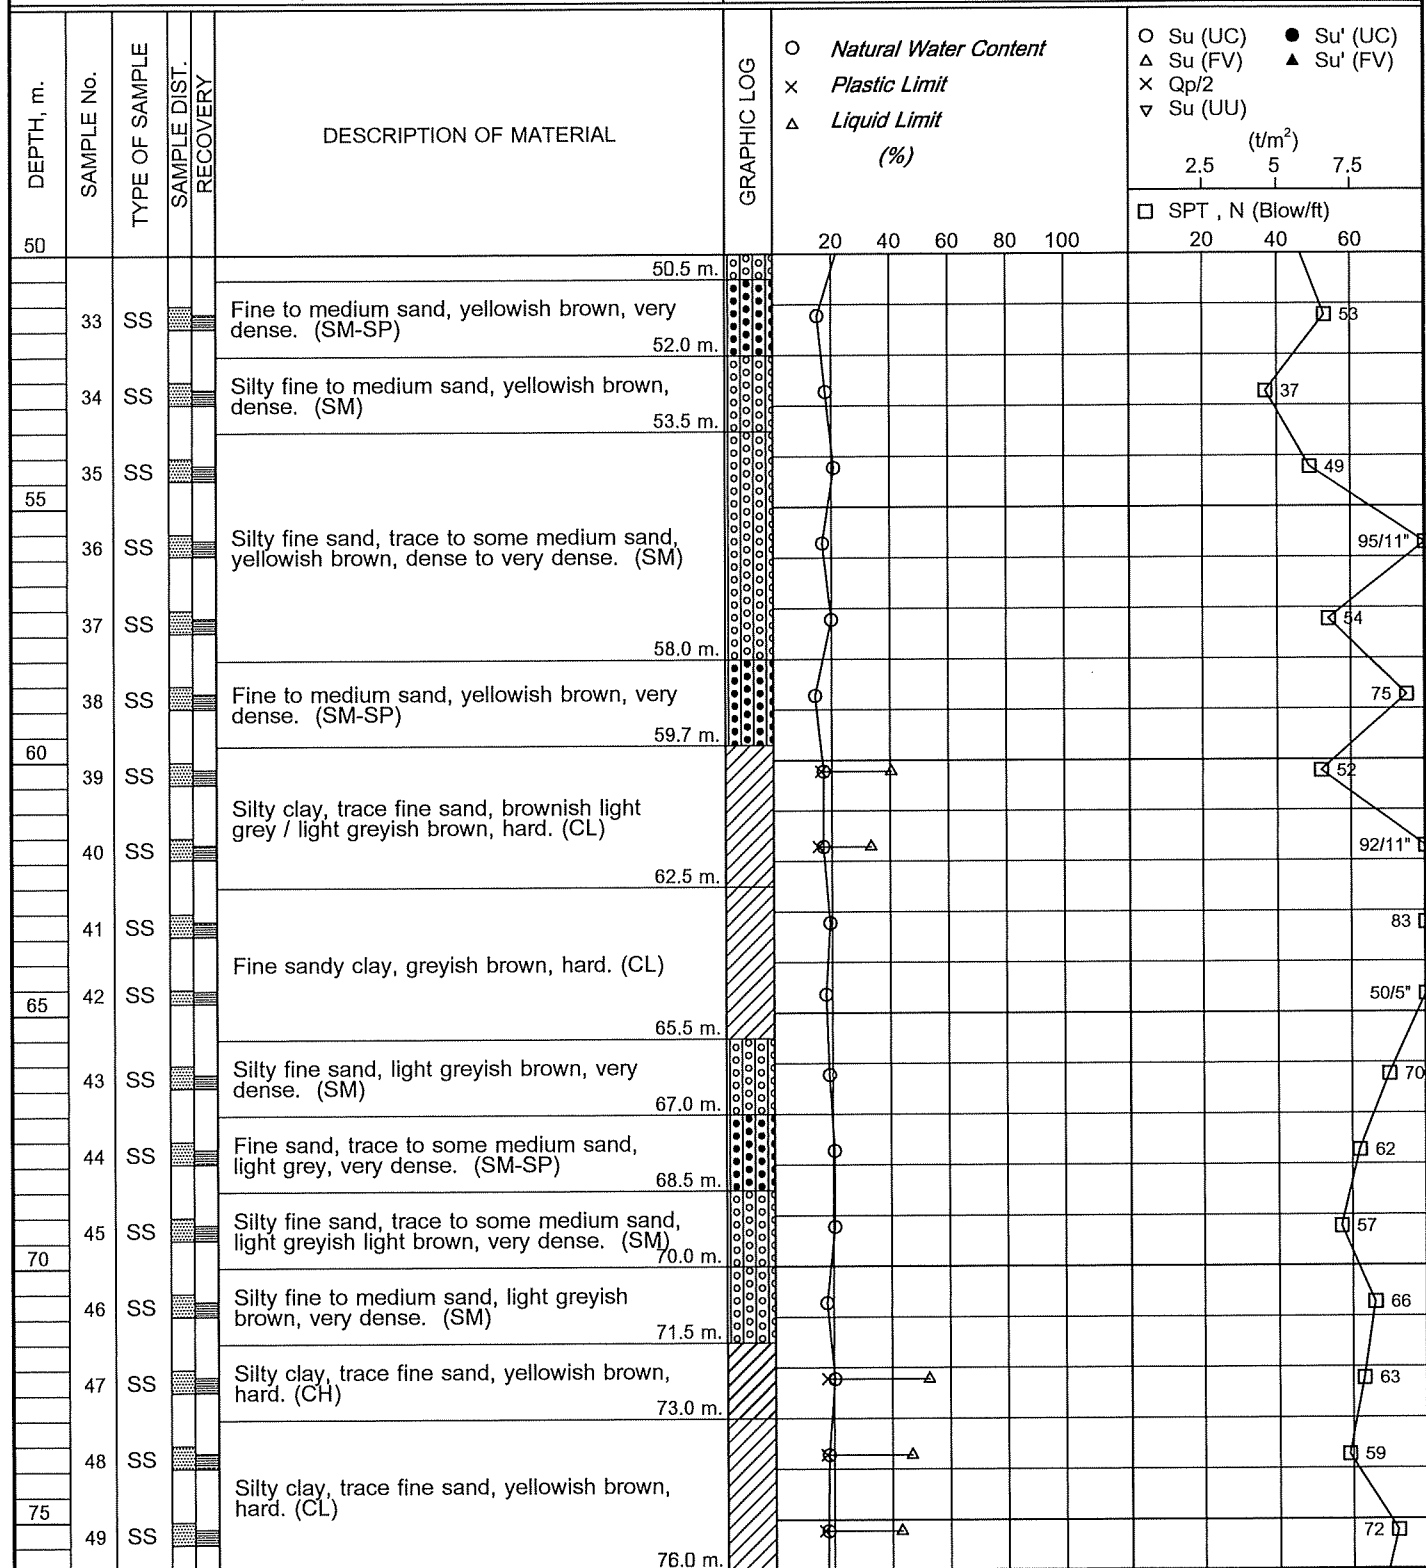

BORING STARTED : 13/11/24

RIG. ACKER

WL. -2.00 m

24 Hrs.
After Boring

BORING FINISHED : 17/11/24

FOREMAN : WN.

JOB No. : 1167287

LOG OF BORING No. OW-47

PROJECT : MRT Orange Line Project : Bang Khun Non -

LOCATION : Bangkok

Min Buri (Suwinthawong) Section

DEPTH, m.	SAMPLE No.	TYPE OF SAMPLE	SAMPLE DIST. RECOVERY	DESCRIPTION OF MATERIAL	GRAPHIC LOG	○ Natural Water Content × Plastic Limit △ Liquid Limit (%)	○ Su (UC) ● Su' (UC) △ Su (FV) ▲ Su' (FV) × Qp/2 ▽ Su (UU)	2.5 5 7.5 (t/m²)	□ SPT, N (Blow/ft) 20 40 60
75									
	49	SS							
				76.0 m.					72
	50	SS		Silty clay, trace fine sand, yellowish brown, hard. (CH)					67
				77.5 m.					
	51	SS		Silty clay, trace fine sand & lime concretion, yellowish brown, hard. (CL)					88
				79.0 m.					
80	52	SS		(F)					64
				79.95 m.					
				END OF BORING					
				(A) Concrete plate.					
				(B) Clayey fine to medium sand, grey to dark grey. (SC)					
				(C) Clay, trace to some fine sand, dark grey, soft. (CH)					
85				(D) Sandy clay, trace to some gravel, with decayed wood, grey, stiff. (CH)					
				(E) Fine sandy clay, greyish brown, very stiff. (CL)					
				(F) Silty clay, trace fine sand, yellowish brown, hard. (CH)					



BORING STARTED : 13/11/24

RIG. ACKER

WL. -2.00 m 24 Hrs. After Boring

BORING FINISHED : 17/11/24

FOREMAN : WN.

JOB No. : 1167287