


# LOG OF BORING No. OW-49

PROJECT : MRT Orange Line Project : Bang Khun Non -

LOCATION : Bangkok

Min Buri (Suwinthawong) Section

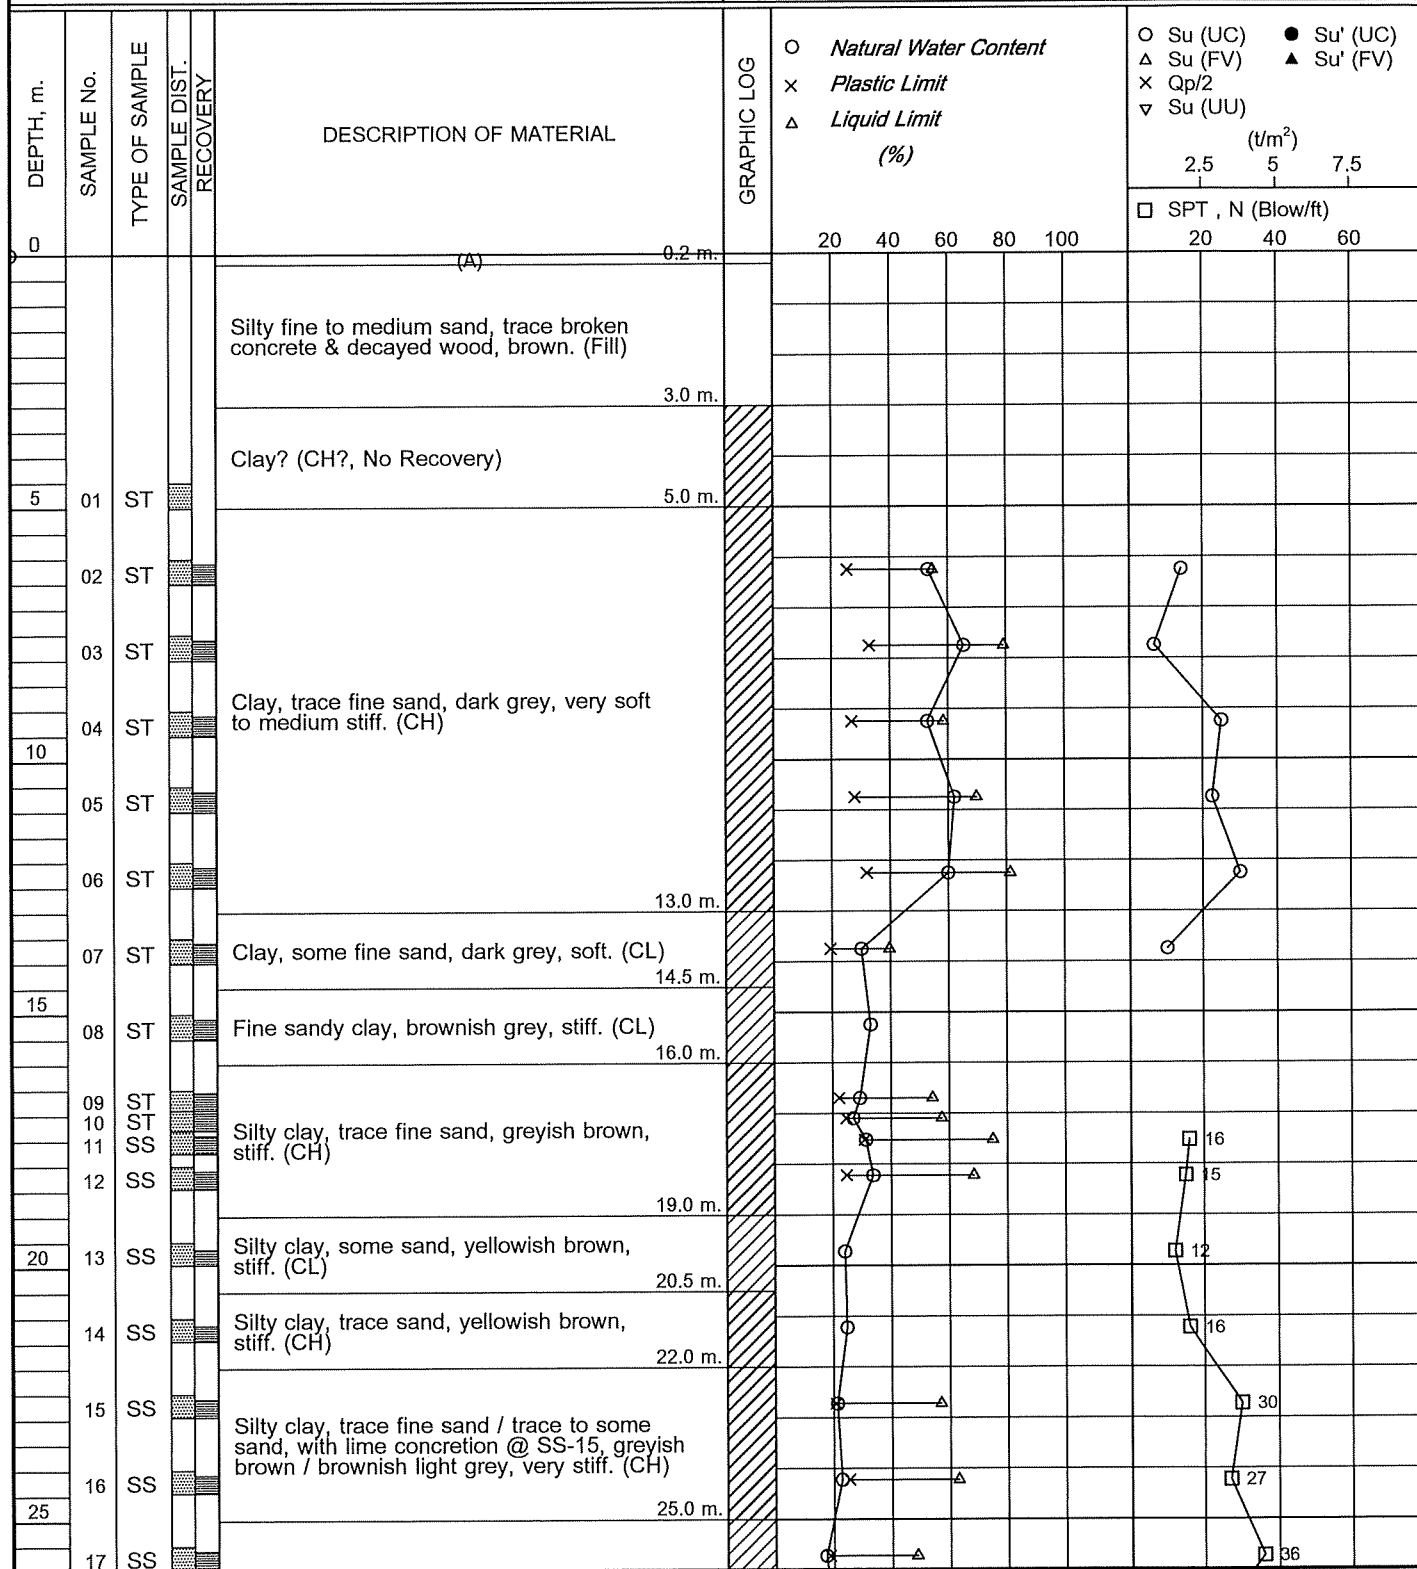

BORING STARTED : 19/11/24

RIG. ACKER

WL. -2.30 m 24 Hrs. After Boring

BORING FINISHED : 23/11/24

FOREMAN : RY.


JOB No. : 1167287

# LOG OF BORING No. OW-49

PROJECT : MRT Orange Line Project : Bang Khun Non -

LOCATION : Bangkok

Min Buri (Suwinthawong) Section

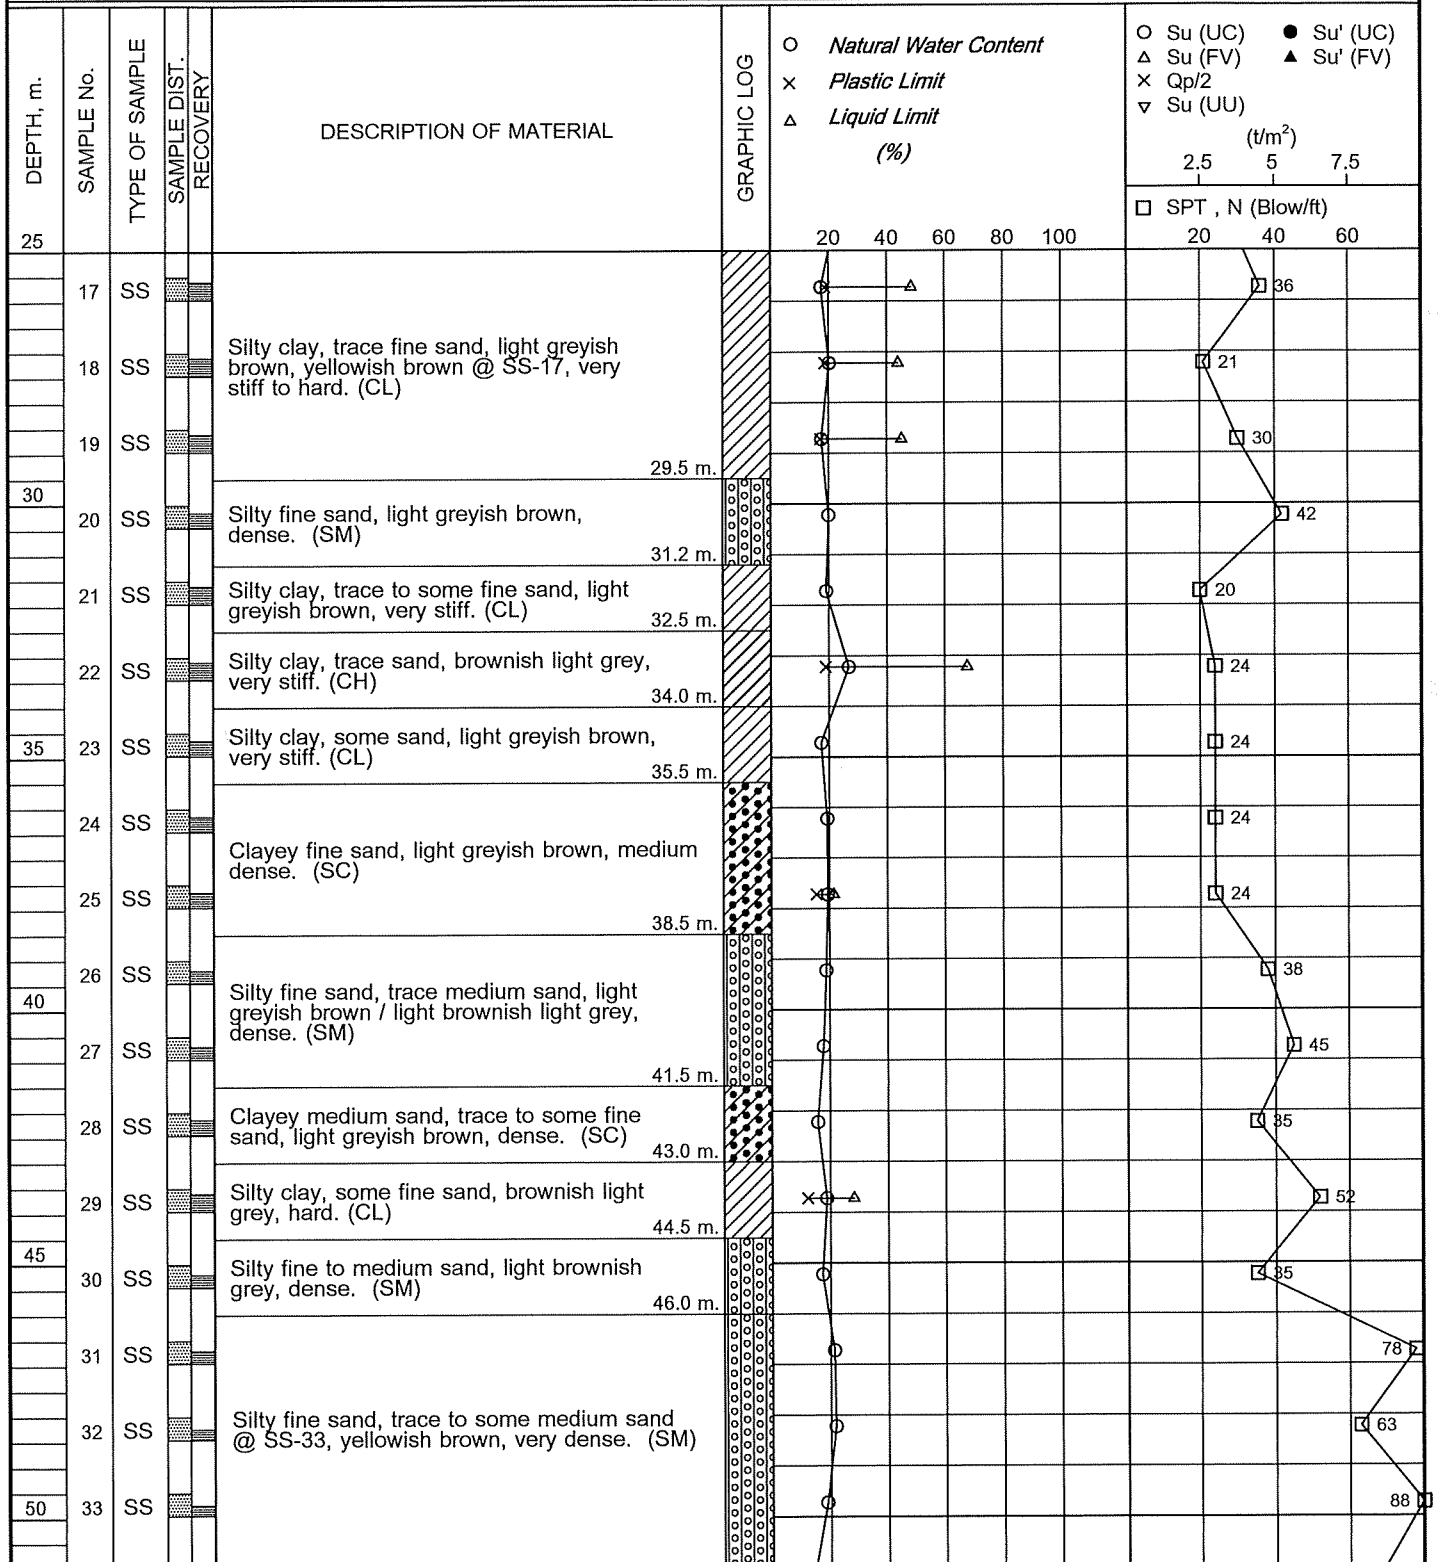

BORING STARTED : 19/11/24

RIG. ACKER

WL. -2.30 m 24 Hrs. After Boring

BORING FINISHED : 23/11/24

FOREMAN : RY.


JOB No. : 1167287

# LOG OF BORING No. OW-49

PROJECT : MRT Orange Line Project : Bang Khun Non -

LOCATION : Bangkok

Min Buri (Suwinthawong) Section

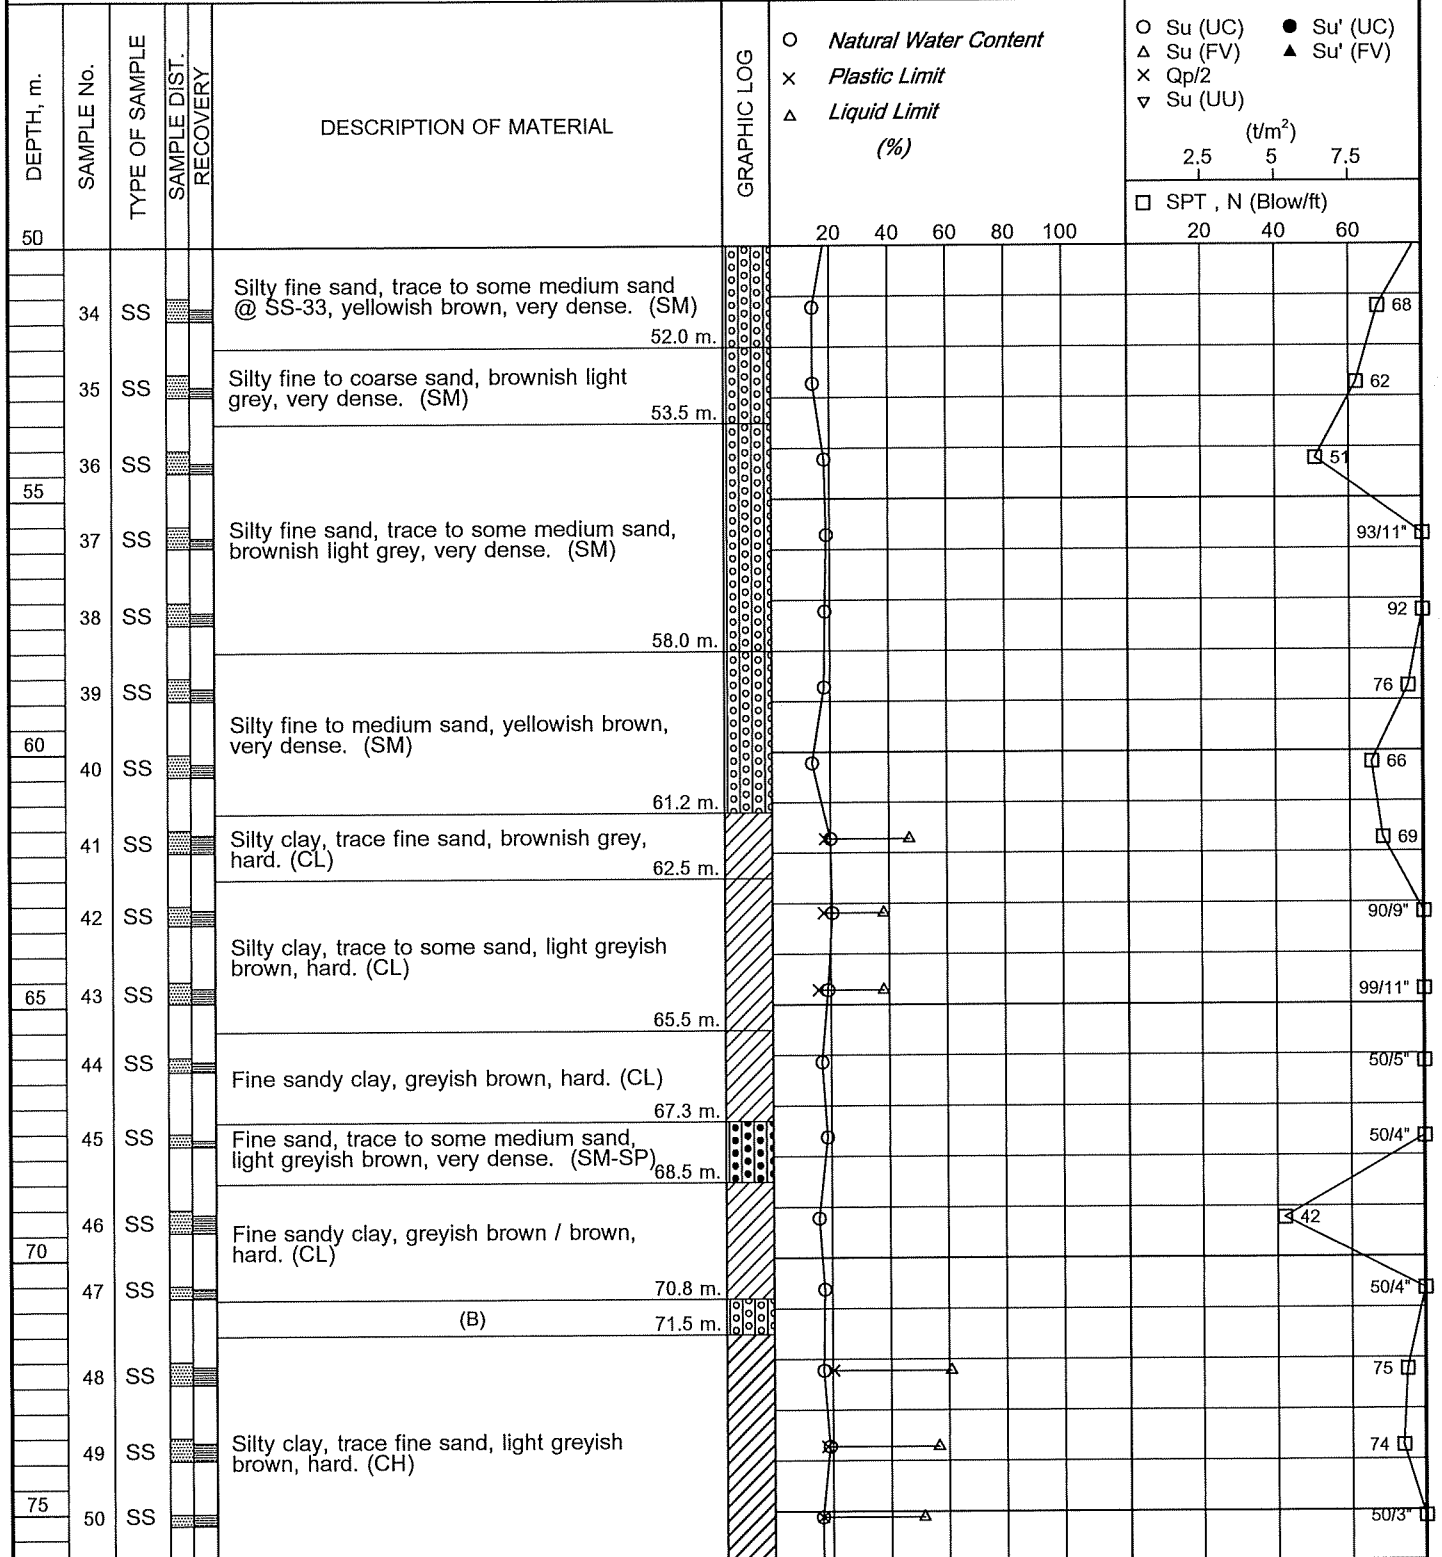

BORING STARTED : 19/11/24

RIG. ACKER

WL. -2.30 m 24 Hrs. After Boring

BORING FINISHED : 23/11/24

FOREMAN : RY.

JOB No. : 1167287

| LOG OF BORING No. OW-49                             |            |                |                          |                                                                 |             |   |
|-----------------------------------------------------|------------|----------------|--------------------------|-----------------------------------------------------------------|-------------|---|
| PROJECT : MRT Orange Line Project : Bang Khun Non - |            |                |                          | LOCATION : Bangkok                                              |             |   |
| Min Buri (Suwinthawong) Section                     |            |                |                          |                                                                 |             |   |
| DEPTH, m.                                           | SAMPLE No. | TYPE OF SAMPLE | SAMPLE DIST.<br>RECOVERY | DESCRIPTION OF MATERIAL                                         | GRAPHIC LOG | ○ Natural Water Content<br>× Plastic Limit<br>Δ Liquid Limit (%)<br>○ Su (UC)<br>Δ Su (FV)<br>× Qp/2<br>▽ Su (UU)<br>● Su' (UC)<br>▲ Su' (FV)<br>(t/m²)<br>□ SPT , N (Blow/ft) |
| 75                                                  |            |                |                          |                                                                 |             | 20 40 60 80 100   |
|                                                     | 50         | SS             |                          |                                                                 |             | 20 40 60 80 100   |
|                                                     | 51         | SS             |                          | Silty clay, trace fine sand, light greyish brown, hard. (CH)    |             | 20 40 60 80 100   |
|                                                     | 52         | SS             |                          |                                                                 |             | 20 40 60 80 100   |
|                                                     | 53         | SS             |                          | Silty clay, some sand, light greyish brown, hard. (CL)          |             | 20 40 60 80 100   |
| 80                                                  |            |                |                          |                                                                 |             | 20 40 60 80 100   |
|                                                     |            |                |                          | (A) Concrete plate & lean concrete.                             |             |   |
|                                                     |            |                |                          | (B) Silty fine sand, trace clay pocket, brown, very dense. (SM) |             |   |
| 85                                                  |            |                |                          |                                                                 |             |   |