


LOG OF BORING No. OW-53

PROJECT : MRT Orange Line Project : Bang Khun Non -

LOCATION : Bangkok

Min Buri (Suwinthawong) Section

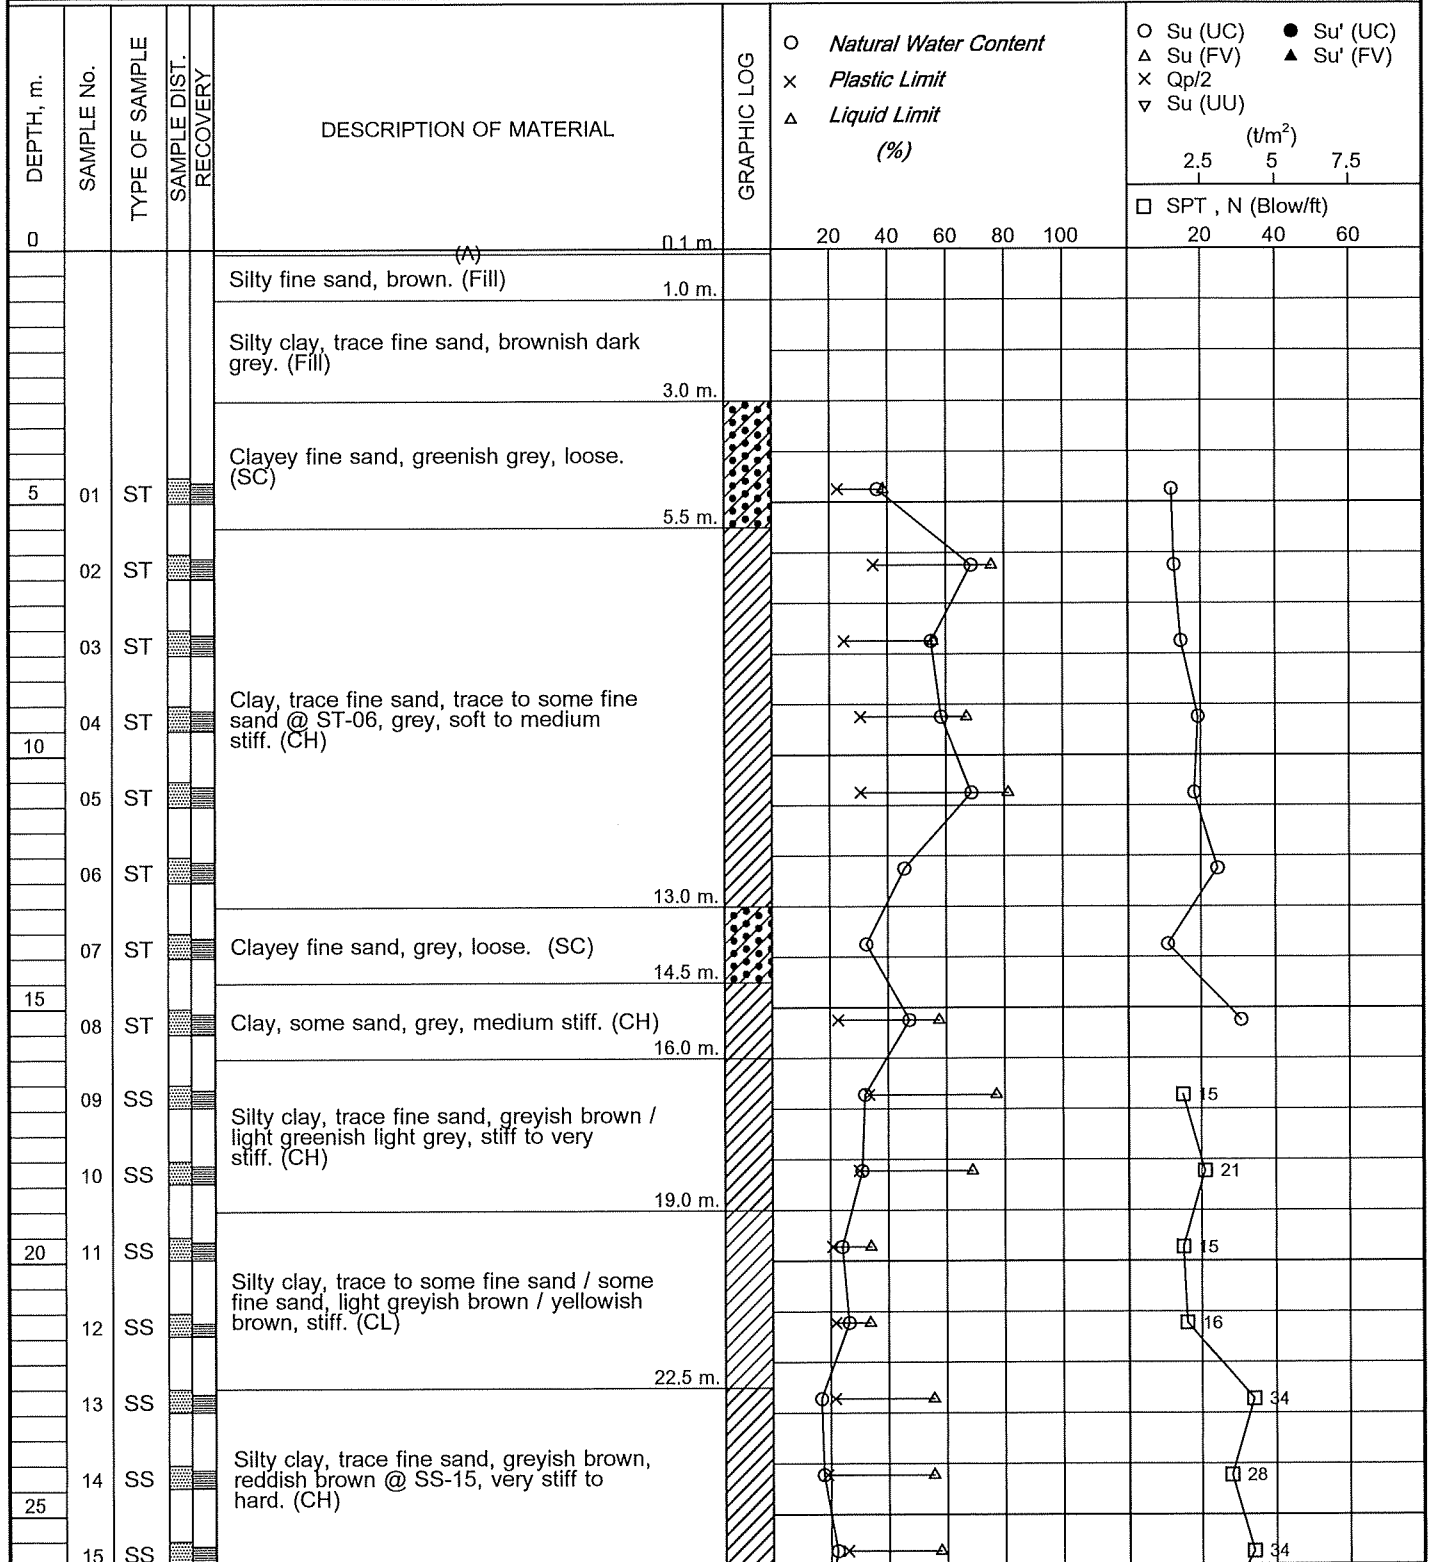

BORING STARTED : 13/12/24

RIG. ACKER

WL. -1.10 m 24 Hrs. After Boring

BORING FINISHED : 18/12/24

FOREMAN : RY.


JOB No. : 1167287

LOG OF BORING No. OW-53

PROJECT : MRT Orange Line Project : Bang Khun Non -

LOCATION : Bangkok

Min Buri (Suwinthawong) Section

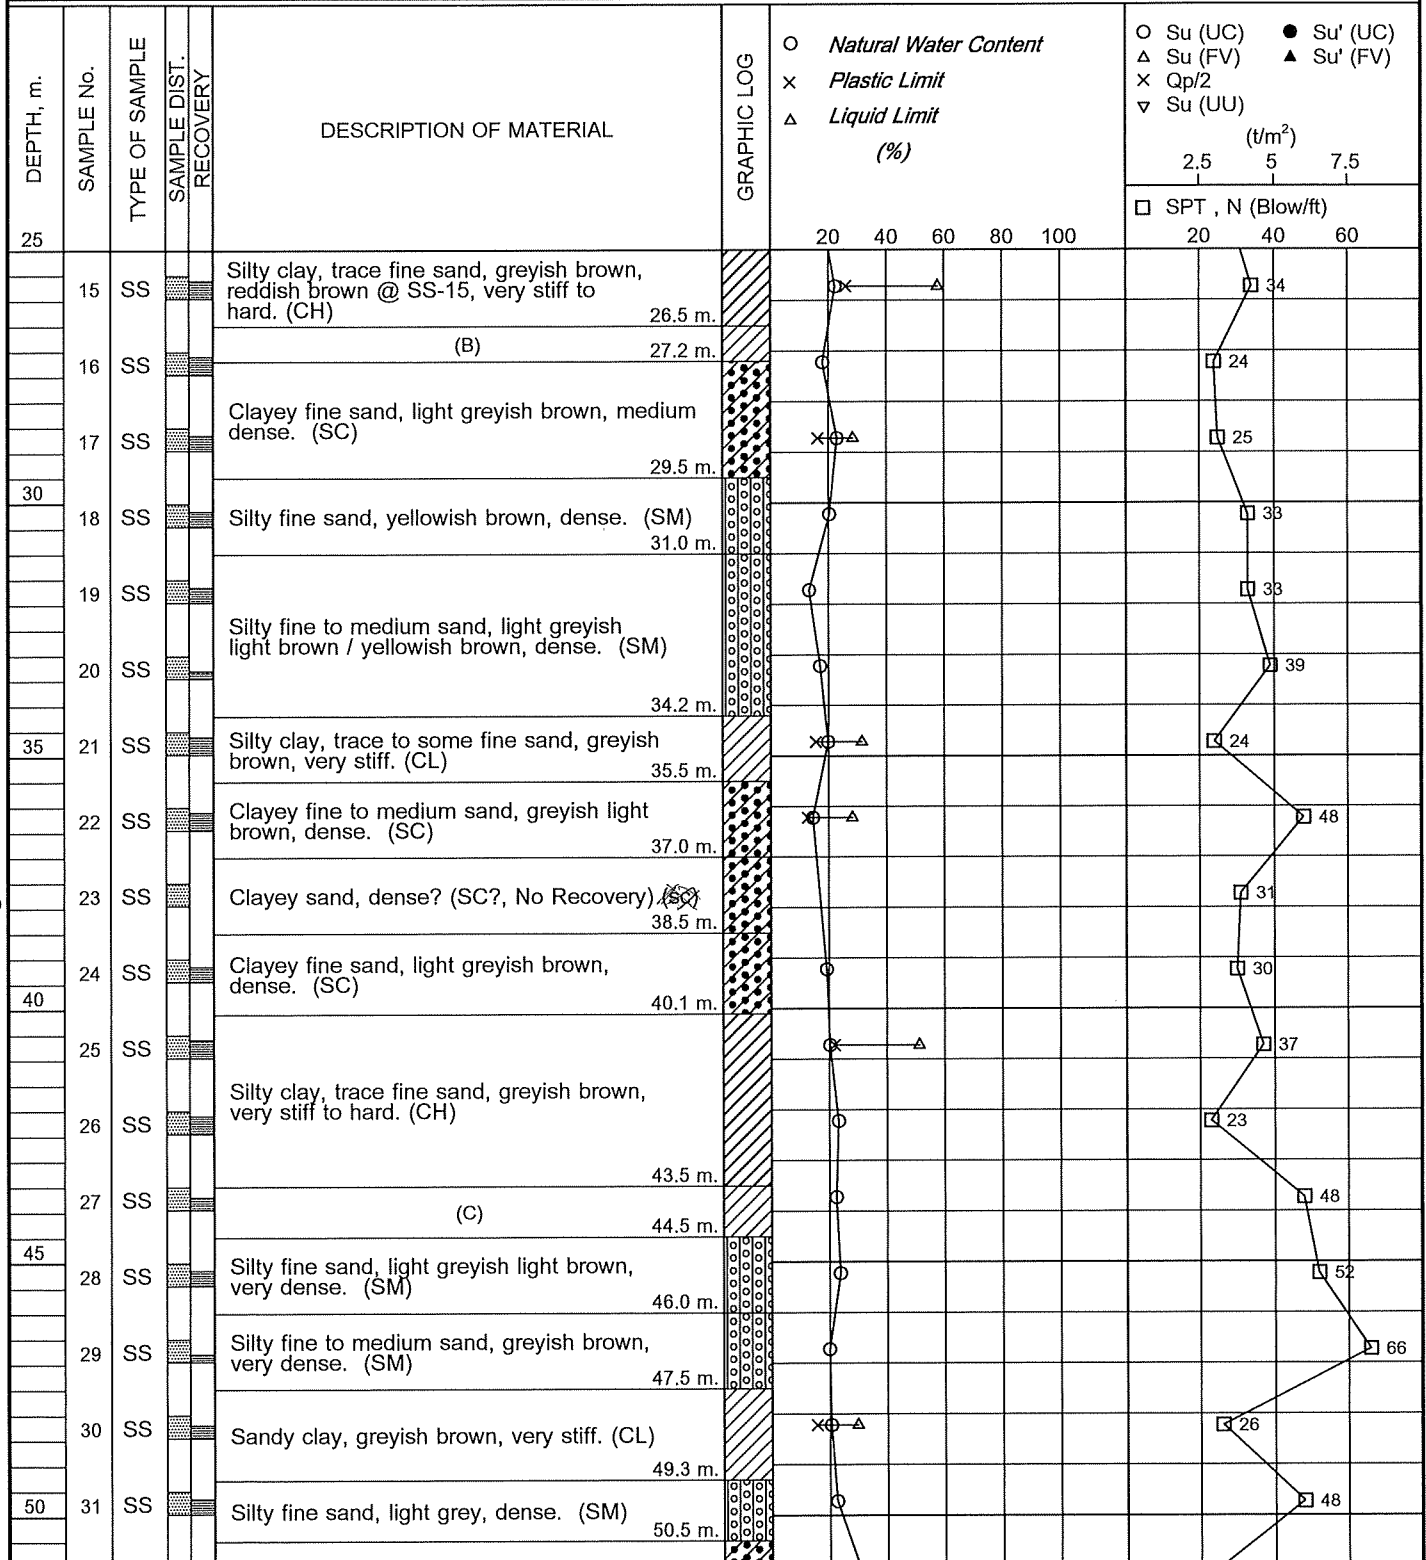

BORING STARTED : 13/12/24

RIG. ACKER

WL. -1.10 m

24 Hrs.
After Boring

BORING FINISHED : 18/12/24

FOREMAN : RY.


JOB No. : 1167287

LOG OF BORING No. OW-53

PROJECT : MRT Orange Line Project : Bang Khun Non -

LOCATION : Bangkok

Min Buri (Suwinthawong) Section

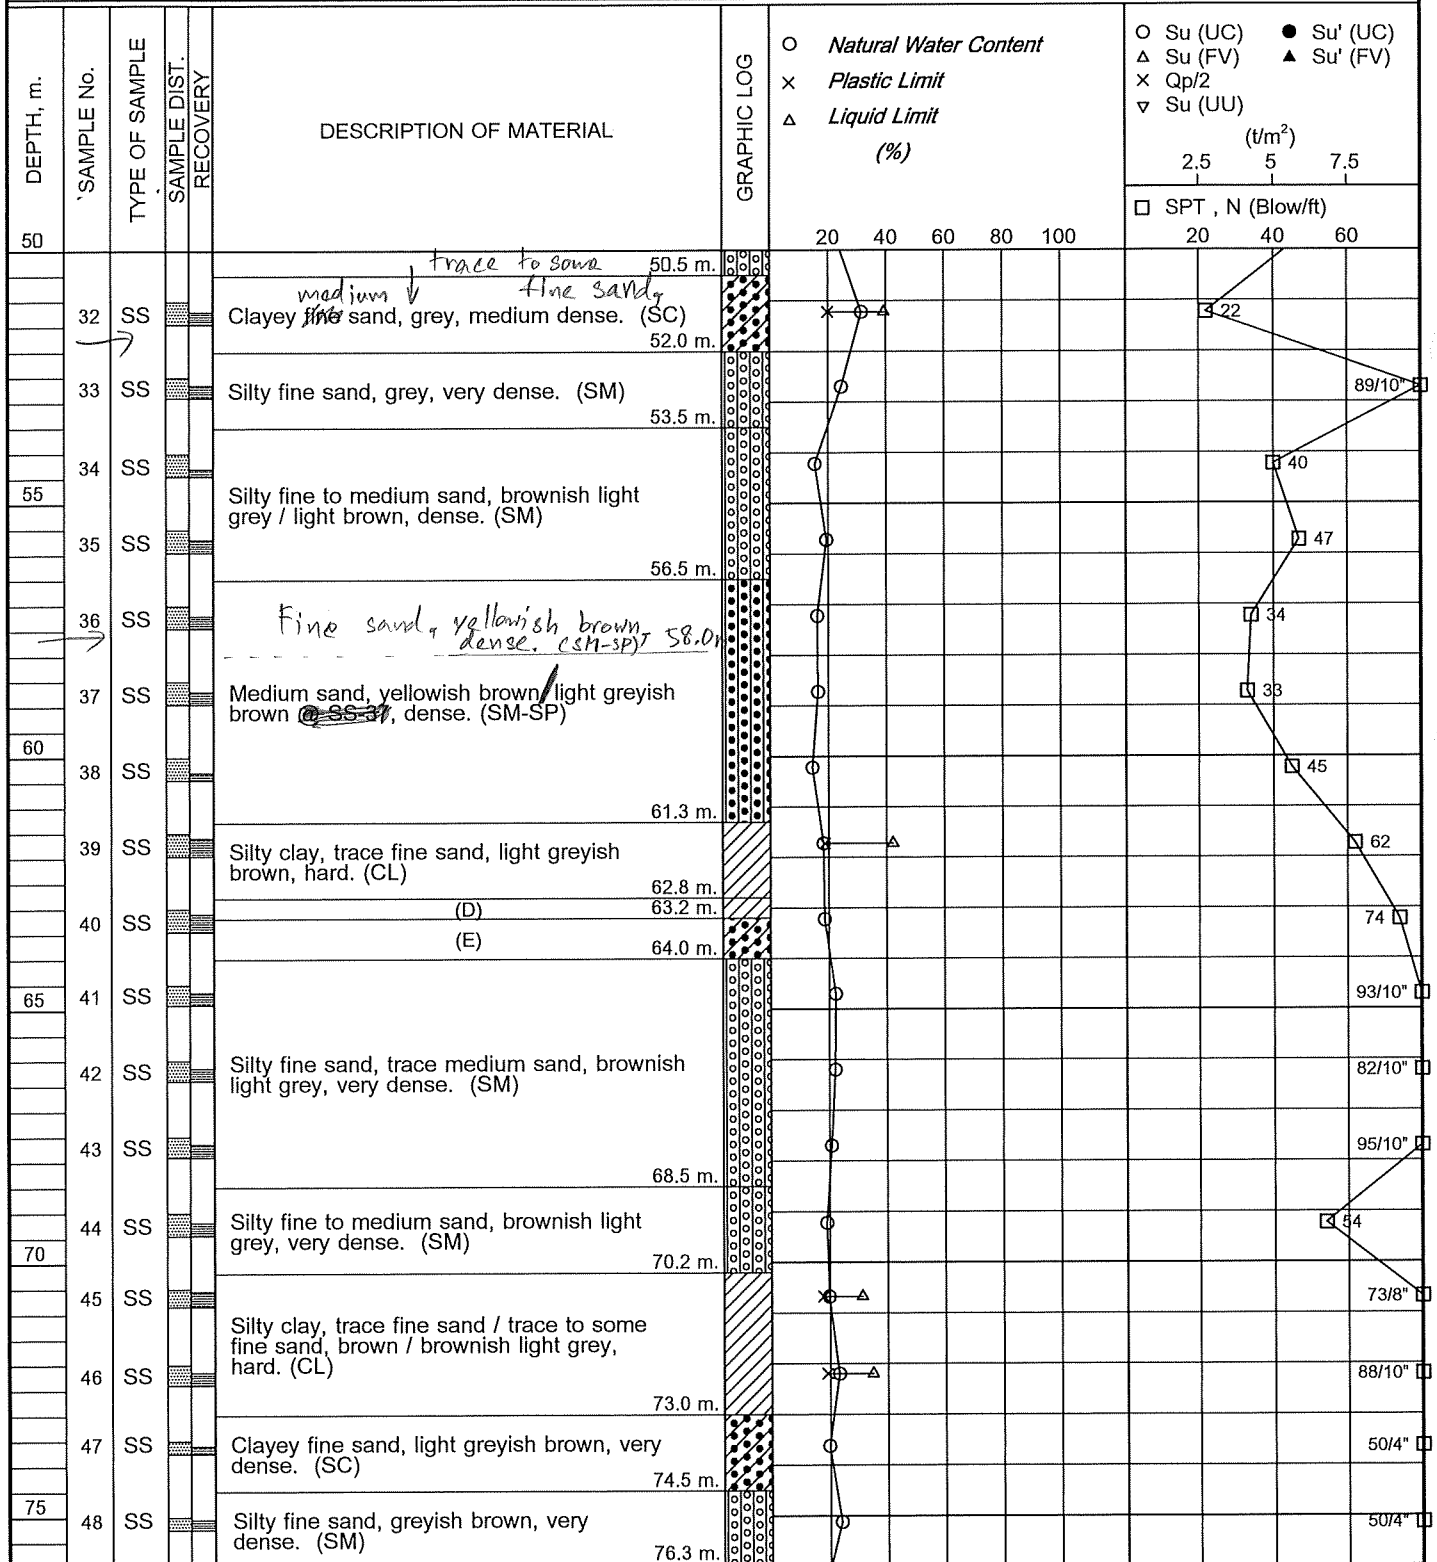

BORING STARTED : 13/12/24

RIG. ACKER

WL. -1.10 m 24 Hrs. After Boring

BORING FINISHED : 18/12/24

FOREMAN : RY.

JOB No. : 1167287

LOG OF BORING No. OW-53

PROJECT : MRT Orange Line Project : Bang Khun Non -

LOCATION : Bangkok

Min Buri (Suwinthawong) Section

DEPTH, m.	SAMPLE No.	TYPE OF SAMPLE	SAMPLE DIST. RECOVERY	DESCRIPTION OF MATERIAL	GRAPHIC LOG	○ Natural Water Content × Plastic Limit △ Liquid Limit (%)	○ Su (UC) ● Su' (UC) △ Su (FV) ▲ Su' (FV) × Qp/2 ▽ Su (UU)	2.5 5 7.5 (t/m²)	□ SPT , N (Blow/ft) 20 40 60
75	48	SS		Silty fine sand, greyish brown, very dense. (SM)					
				76.3 m.					
	49	SS							
	50	SS		Silty clay, trace fine sand, some fine sand @ SS-50, greyish brown, hard. (CL)					
				80.00 m.					
80	51	SS							
				END OF BORING					
				(A) Concrete plate.					
				(B) Fine sandy clay, light greyish brown, very stiff. (CL)					
				(C) Fine sandy clay, light greyish brown, hard. (CL)					
85				(D) Fine sandy clay brownish light grey, hard. (CL)					
				(E) Clayey fine sand, brownish light grey, very dense. (SC)					



BORING STARTED : 13/12/24

RIG. ACKER

WL. -1.10 m 24 Hrs. After Boring

BORING FINISHED : 18/12/24

FOREMAN : RY.

JOB No. : 1167287