


LOG OF BORING No. OW-54

PROJECT : MRT Orange Line Project : Bang Khun Non -

LOCATION : Bangkok

Min Buri (Suwinthawong) Section

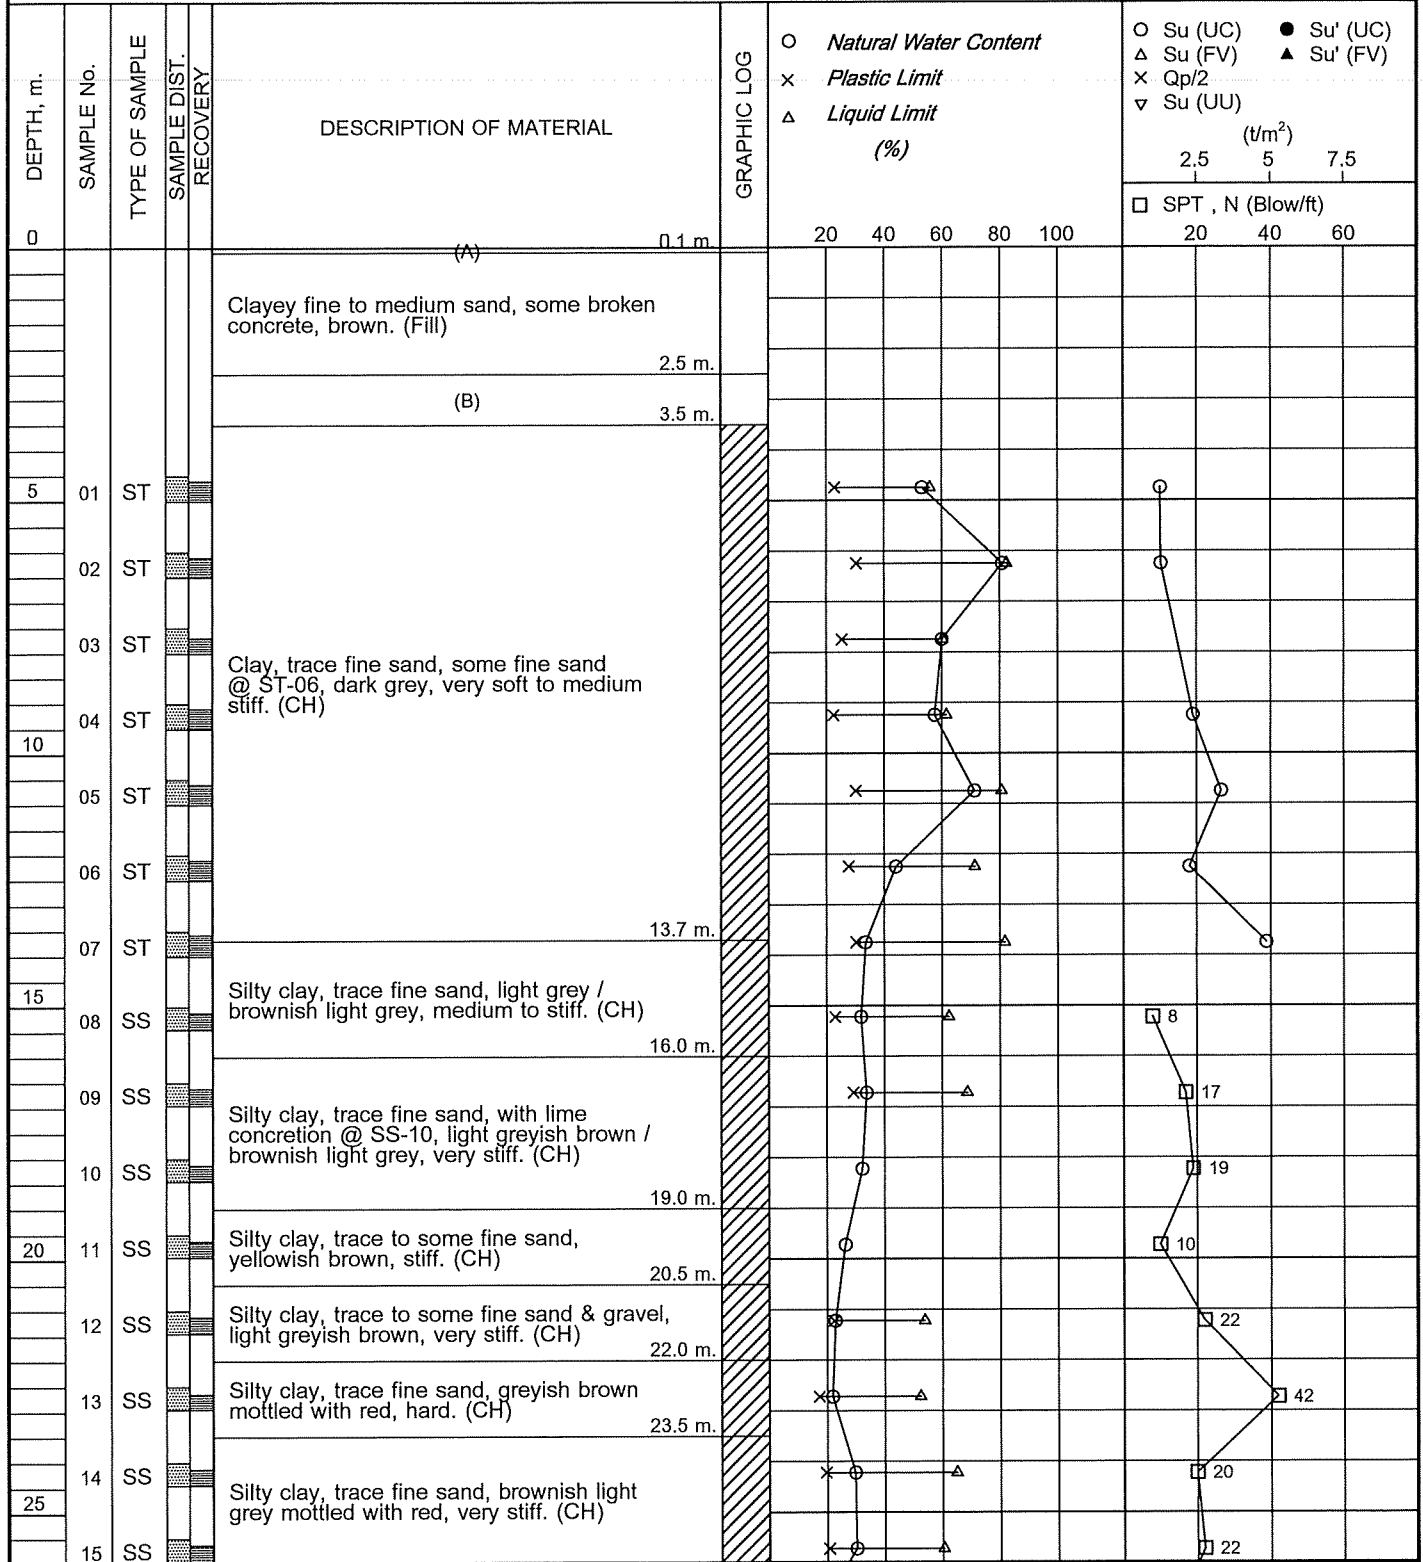

BORING STARTED : 06/04/25

RIG. ACKER

WL. -2.50 m 24 Hrs. After Boring

BORING FINISHED : 10/04/25

FOREMAN : WN.


JOB No. : 1167287

LOG OF BORING No. OW-54

PROJECT : MRT Orange Line Project : Bang Khun Non -

LOCATION : Bangkok

Min Buri (Suwinthawong) Section

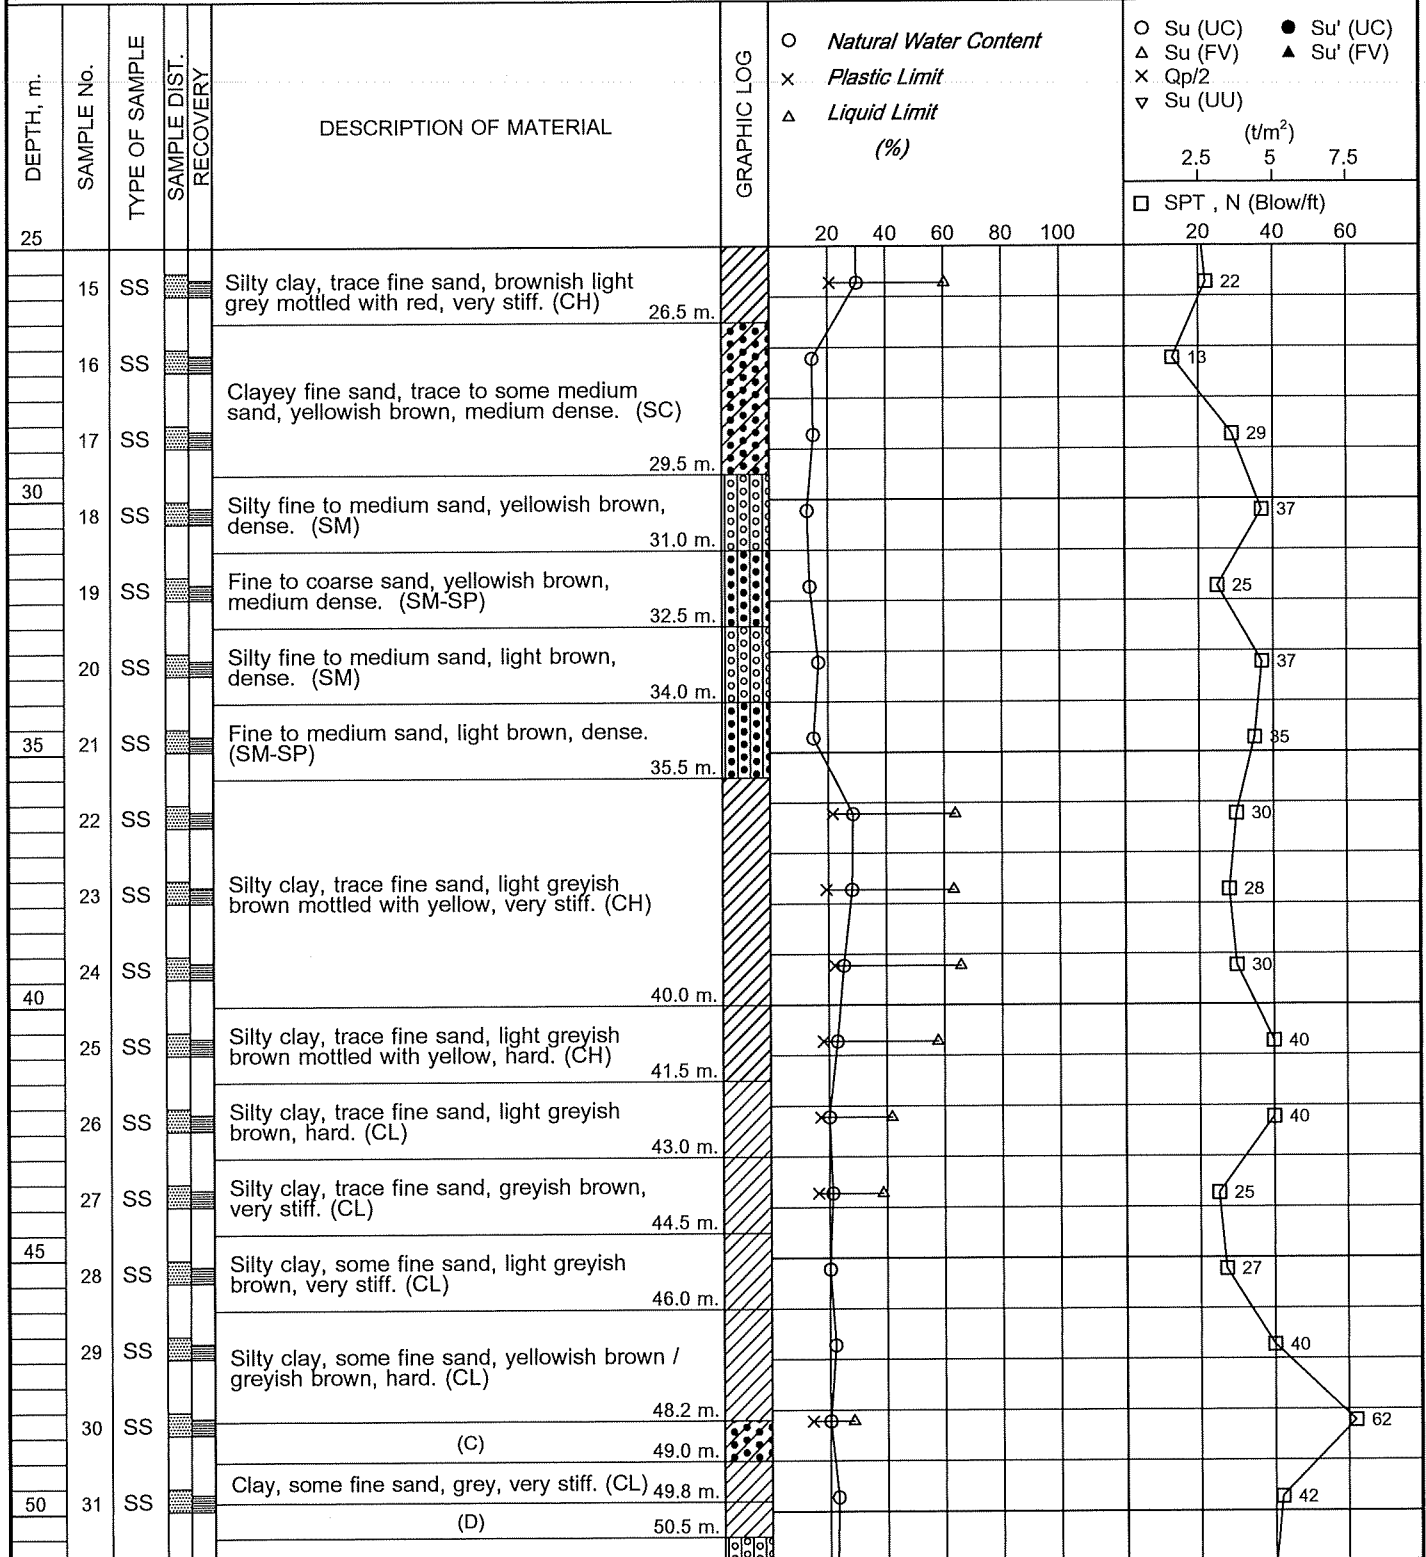

BORING STARTED : 06/04/25

RIG. ACKER

WL. -2.50 m 24 Hrs. After Boring

BORING FINISHED : 10/04/25

FOREMAN : WN.


JOB No. : 1167287

LOG OF BORING No. OW-54

PROJECT : MRT Orange Line Project : Bang Khun Non -

LOCATION : Bangkok

Min Buri (Suwinthawong) Section

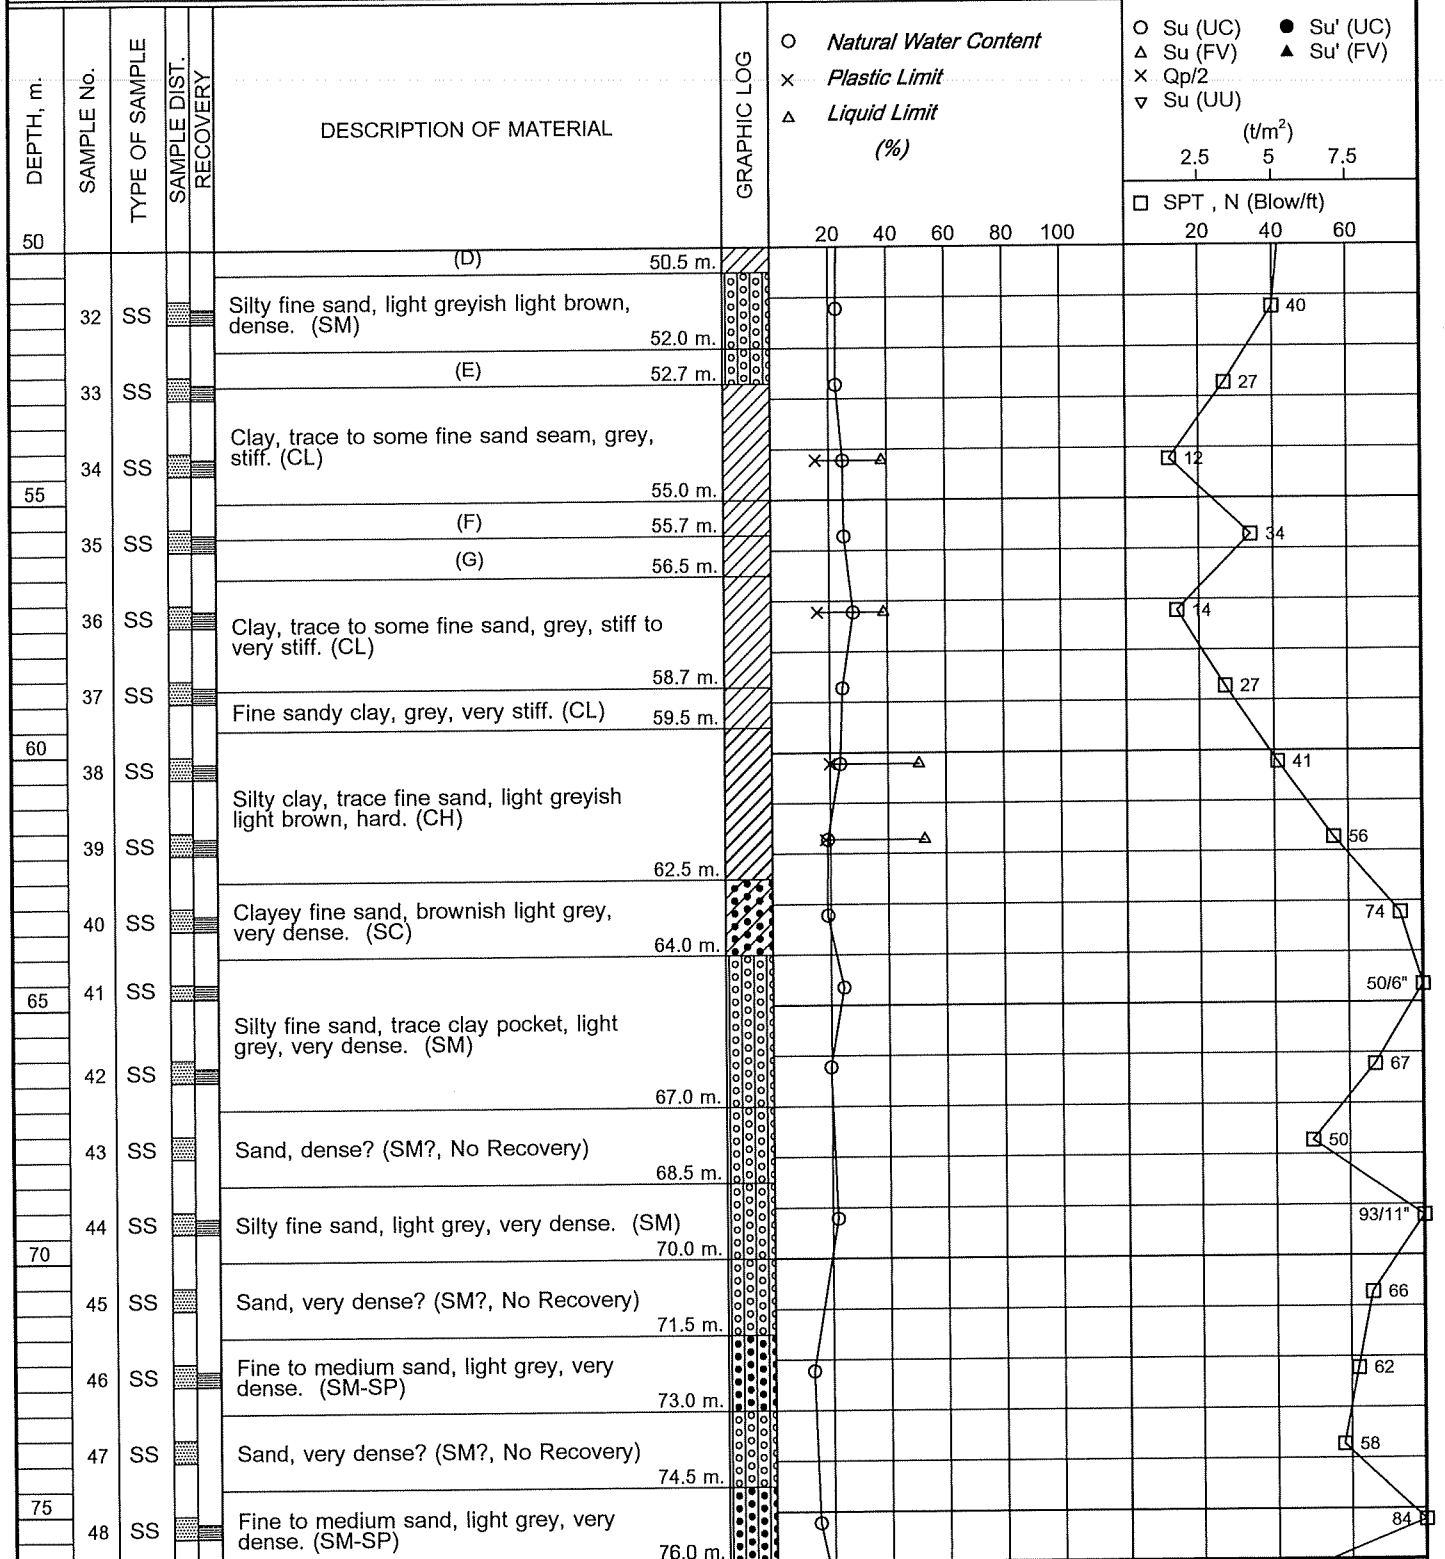

BORING STARTED : 06/04/25

RIG. ACKER

WL. -2.50 m

24 Hrs.
After Boring

BORING FINISHED : 10/04/25

FOREMAN : WN.


JOB No. : 1167287

LOG OF BORING No. OW-54

PROJECT : MRT Orange Line Project : Bang Khun Non -

LOCATION : Bangkok

Min Buri (Suwinthawong) Section

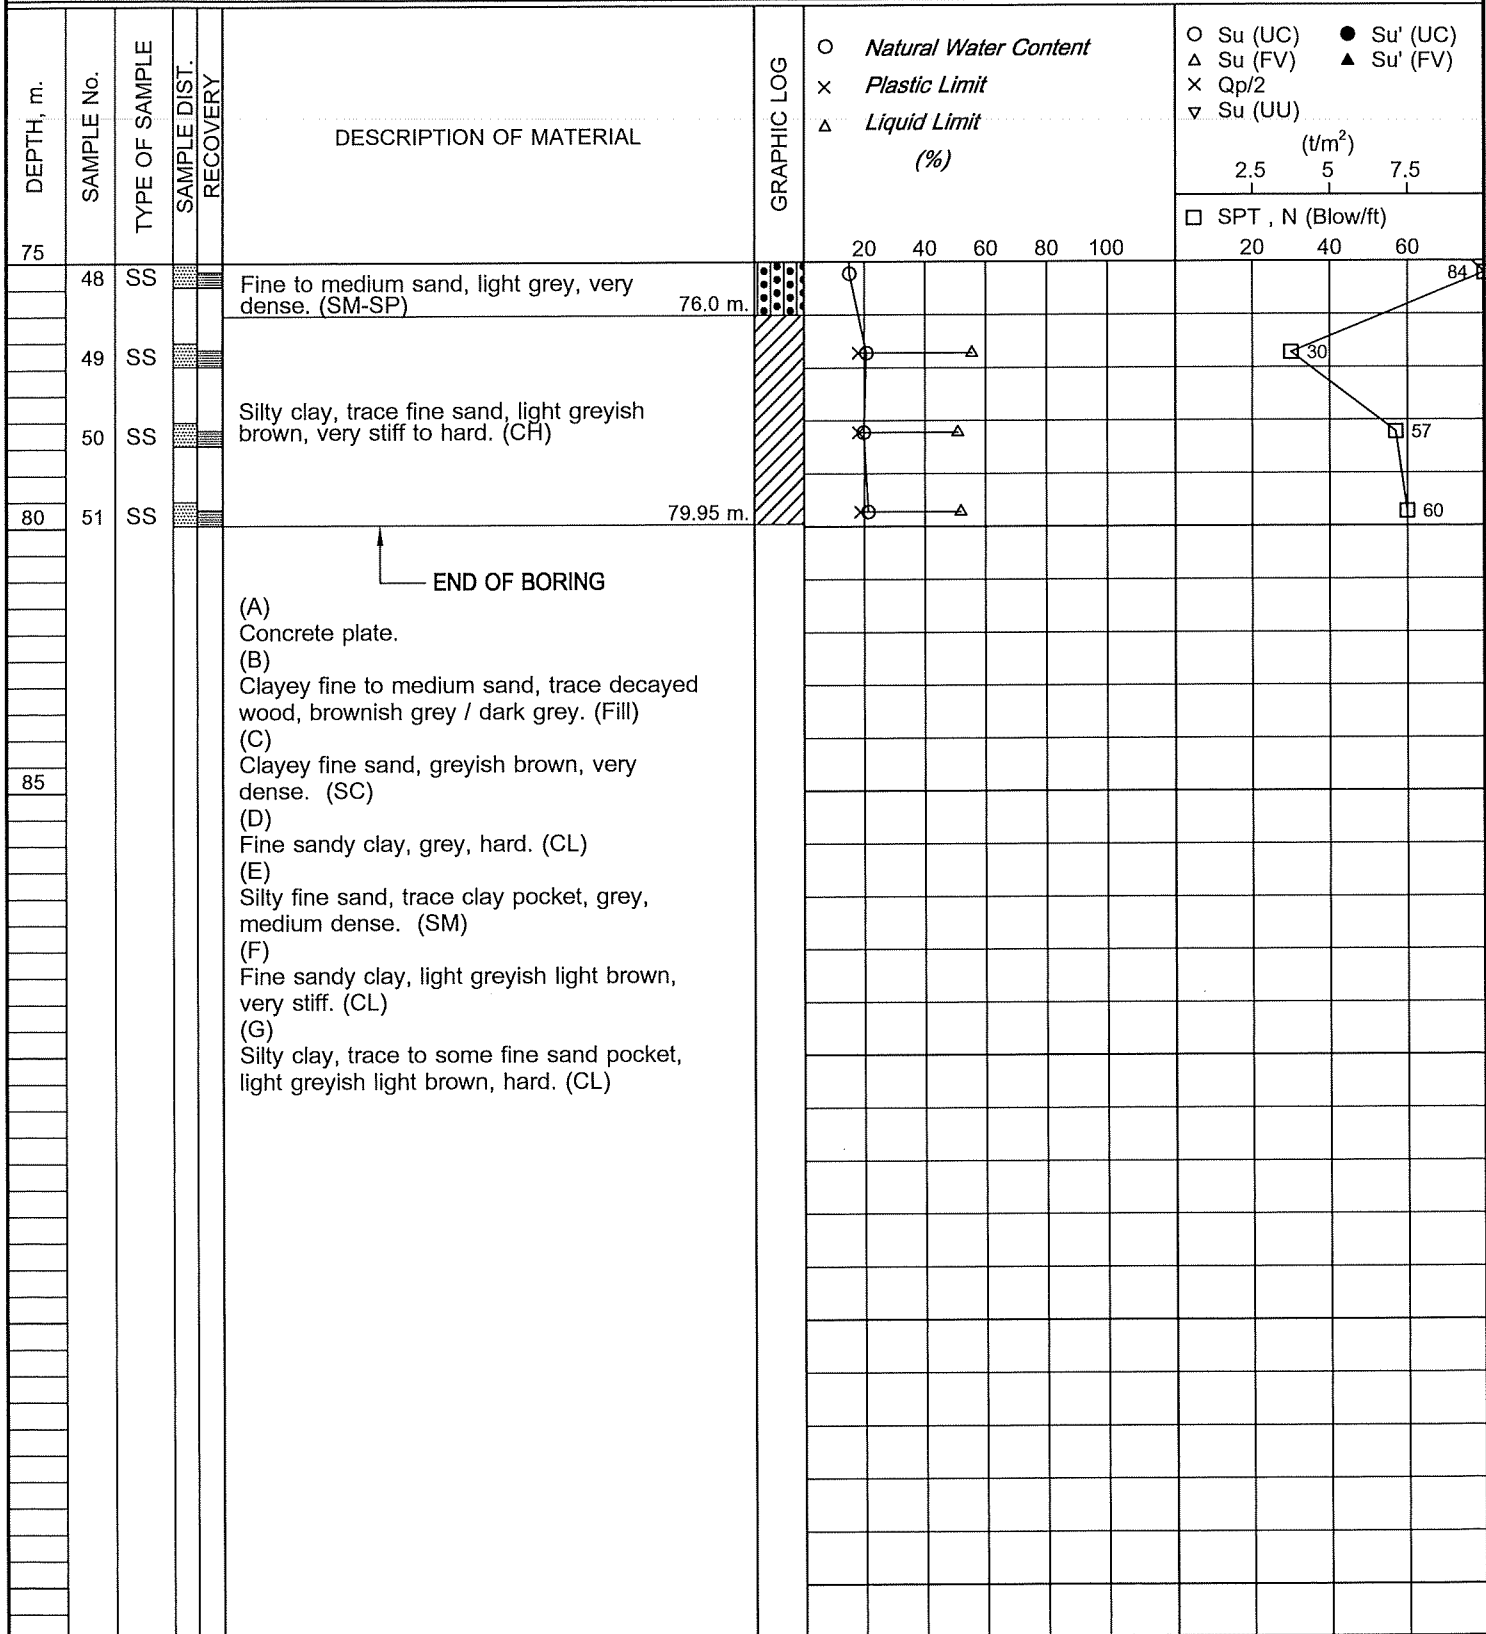

BORING STARTED : 06/04/25

RIG. ACKER

WL. -2.50 m 24 Hrs.
After Boring

BORING FINISHED : 10/04/25

FOREMAN : WN.

JOB No. : 1167287