


LOG OF BORING No. OW-55

PROJECT : MRT Orange Line Project : Bang Khun Non -

LOCATION : Bangkok

Min Buri (Suwinthawong) Section

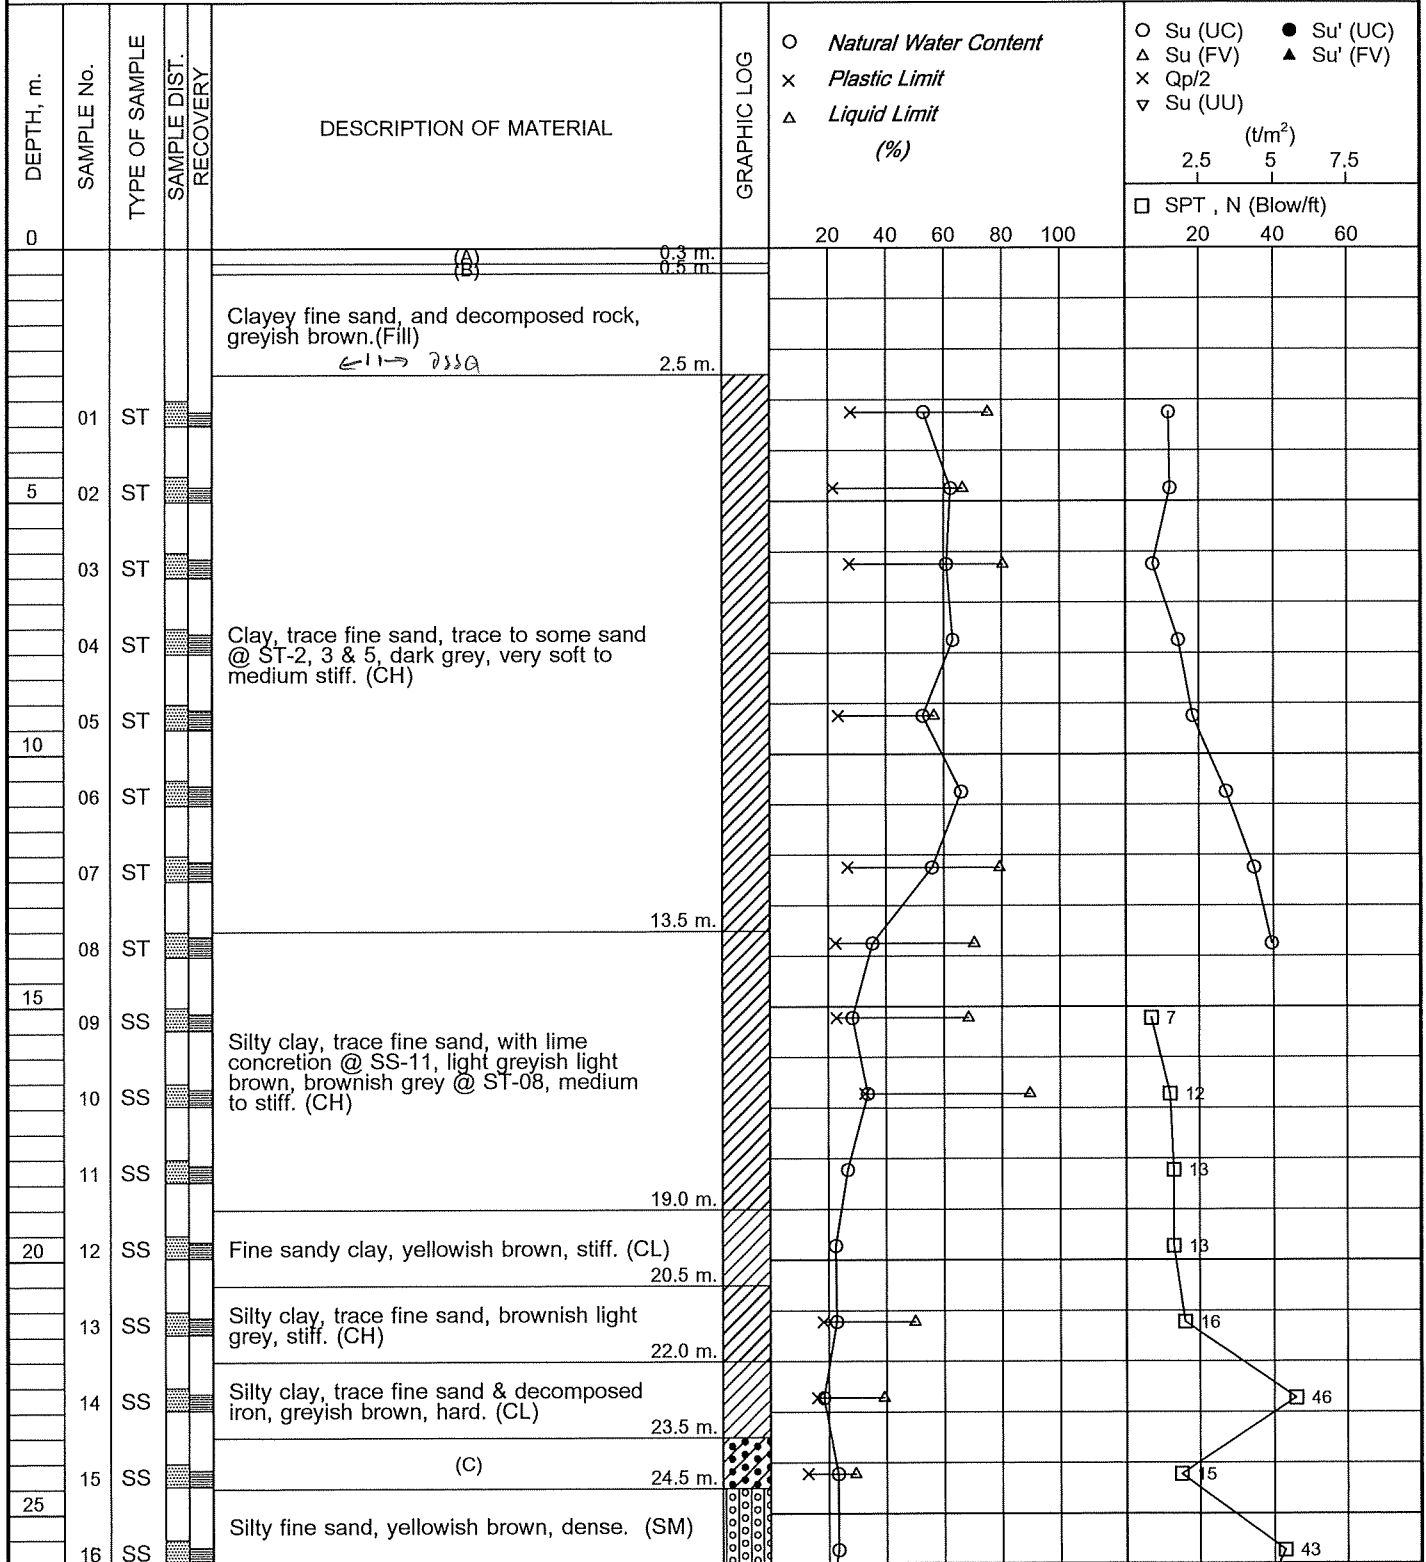

BORING STARTED : 20/12/24

RIG. ACKER

WL. -2.50 m

24 Hrs. After Boring

BORING FINISHED : 24/12/24

FOREMAN : WN.


JOB No. : 1167287

LOG OF BORING No. OW-55

PROJECT : MRT Orange Line Project : Bang Khun Non -

LOCATION : Bangkok

Min Buri (Suwinthawong) Section

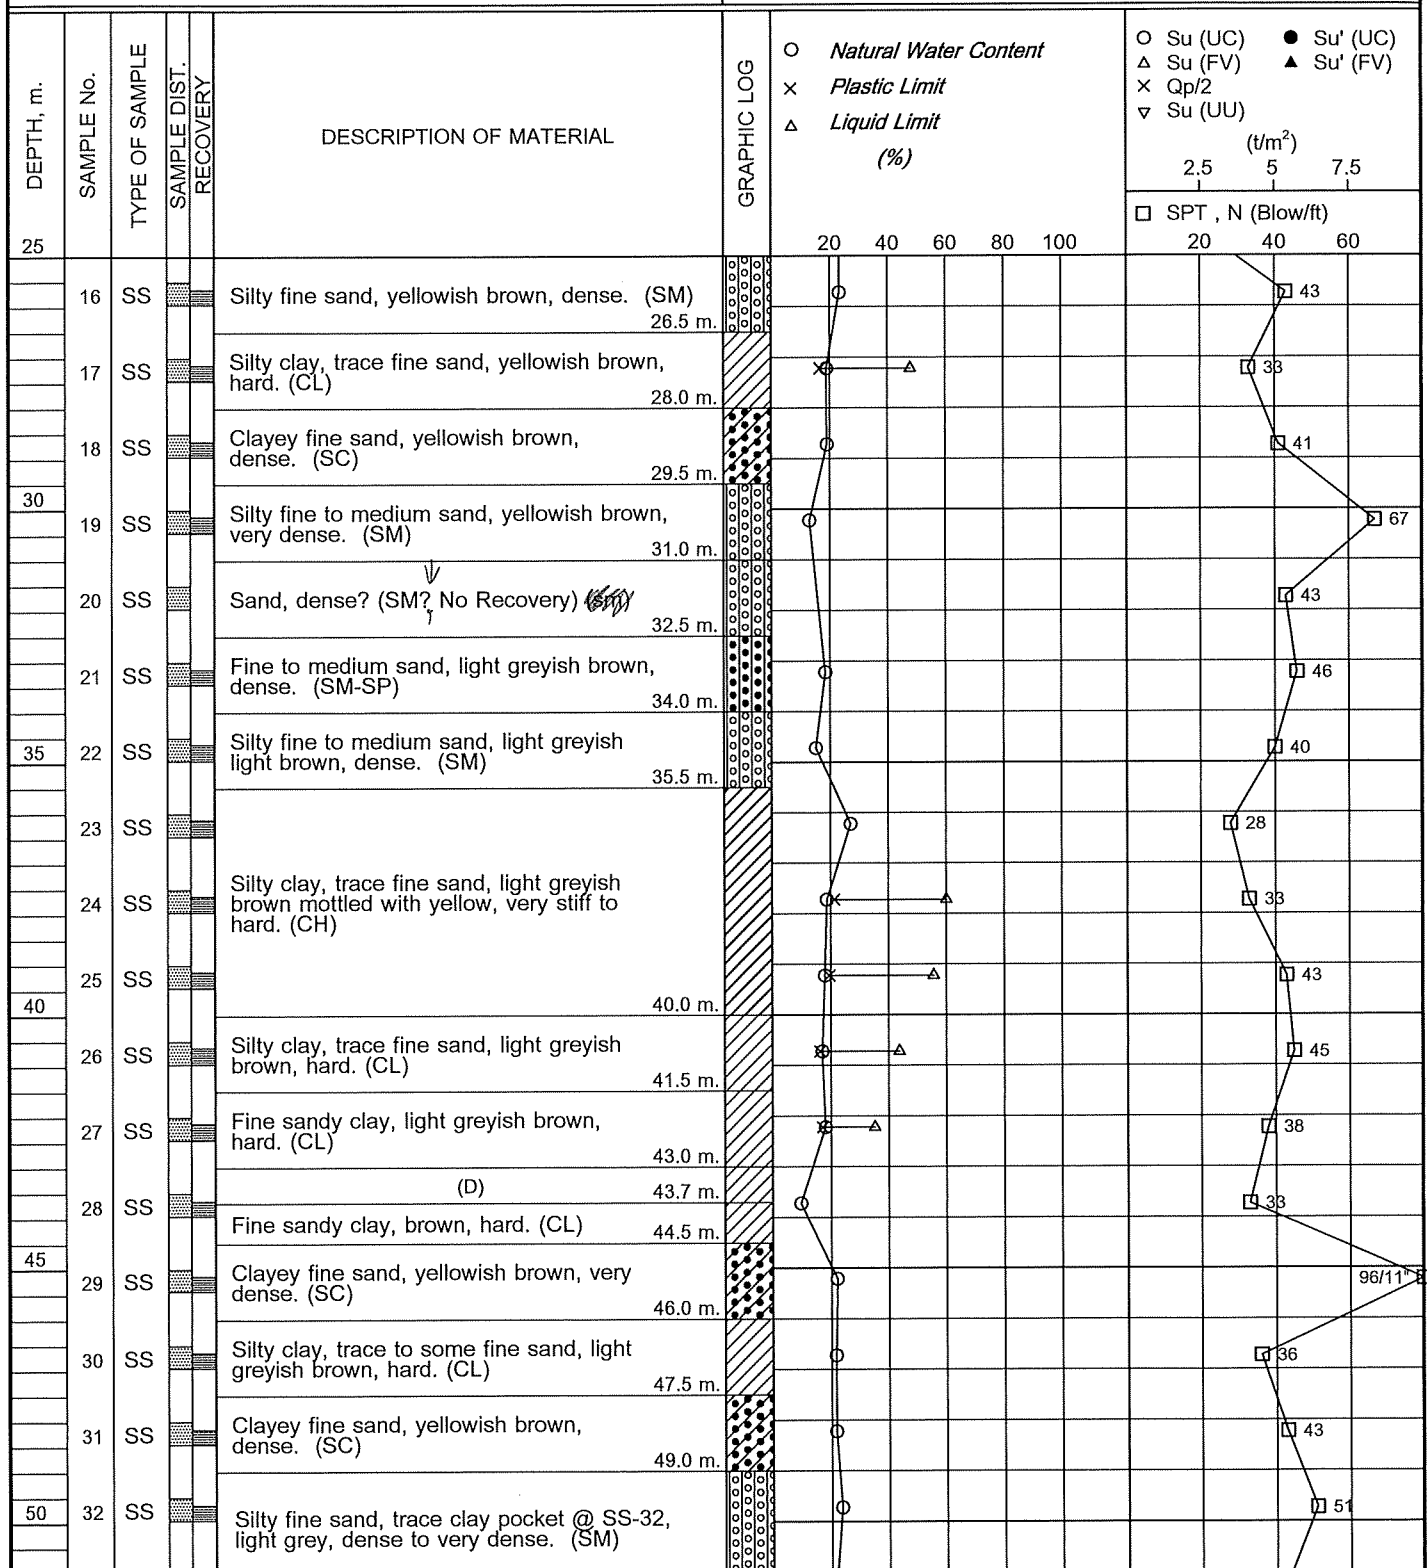

BORING STARTED : 20/12/24

RIG. ACKER

WL. -2.50 m 24 Hrs. After Boring

BORING FINISHED : 24/12/24

FOREMAN : WN.


JOB No. : 1167287

LOG OF BORING No. OW-55

PROJECT : MRT Orange Line Project : Bang Khun Non -

LOCATION : Bangkok

Min Buri (Suwinthawong) Section

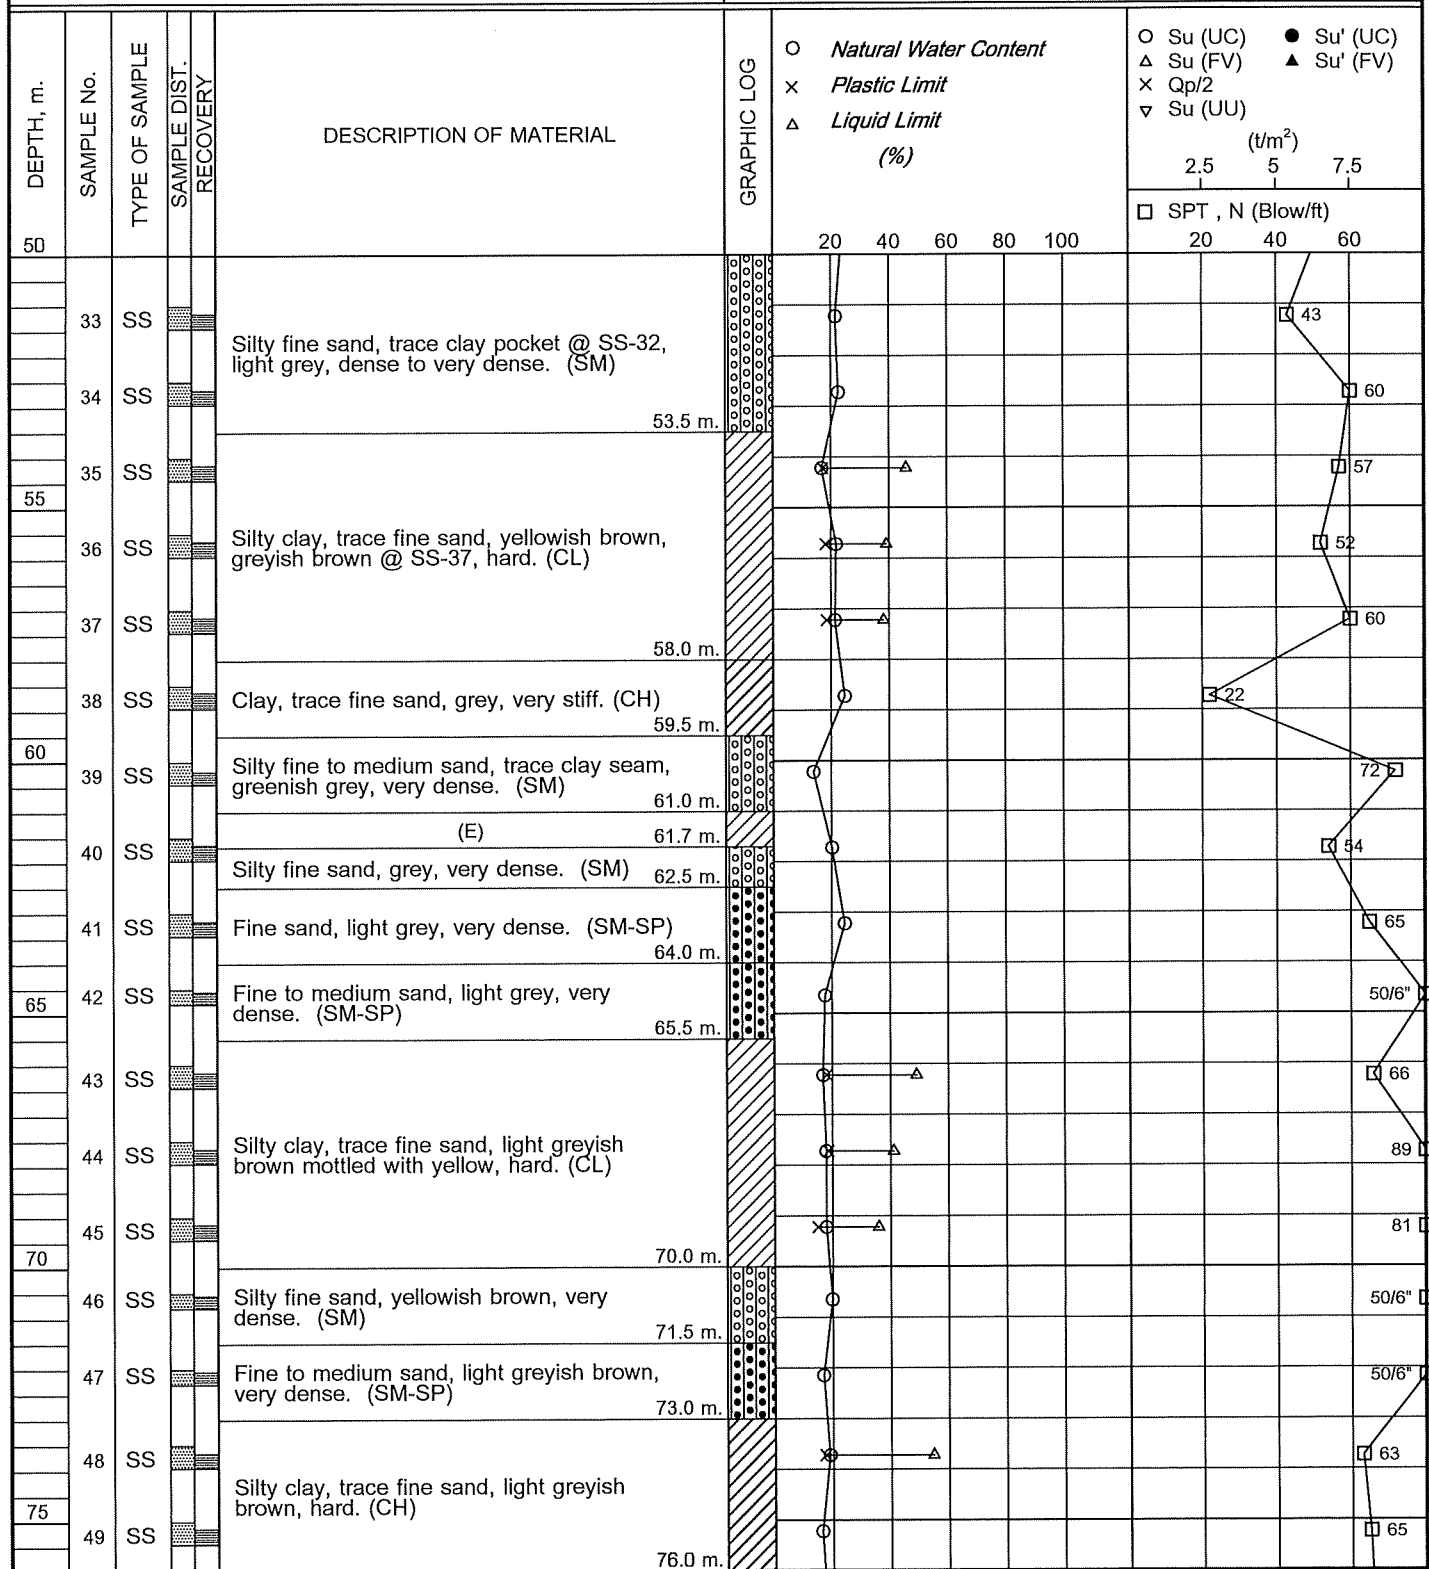

BORING STARTED : 20/12/24

RIG. ACKER

WL. -2.50 m

24 Hrs.
After Boring

BORING FINISHED : 24/12/24

FOREMAN : WN.

JOB No. : 1167287

LOG OF BORING No. OW-55

PROJECT : MRT Orange Line Project : Bang Khun Non -

LOCATION : Bangkok

Min Buri (Suwinthawong) Section

DEPTH, m.	SAMPLE No.	TYPE OF SAMPLE	SAMPLE DIST. RECOVERY	DESCRIPTION OF MATERIAL	GRAPHIC LOG	○ <i>Natural Water Content</i> × <i>Plastic Limit</i> Δ <i>Liquid Limit (%)</i>	○ Su (UC) ● Su' (UC) Δ Su (FV) ▲ Su' (FV) × Qp/2 ▽ Su (UU) (t/m ²) 2.5 5 7.5 □ SPT, N (Blow/ft) 20 40 60
75	49	SS					
				76.0 m.			
	50	SS					
	51	SS		Silty clay, trace fine sand & lime concretion light greyish brown, hard. (CH)			
	52	SS		85 79.95 m.			
80							
				END OF BORING			
				(A) Concrete slab.			
				(B) Silty fine to medium sand, brown. (Fill)			
				(C) Clayey fine sand, light greyish brown, medium dense. (SC)			
85				(D) Silty clay, trace to some fine sand, brown, hard. (CL)			
				(E) Sandy clay, grey, hard. (CL)			



BORING STARTED : 20/12/24

RIG. ACKER

WL. -2.50 m 24 Hrs.
After Boring

BORING FINISHED : 24/12/24

FOREMAN : WN.

JOB No. : 1167287