


# LOG OF BORING No. OW-57

PROJECT : MRT Orange Line Project : Bang Khun Non -

LOCATION : Bangkok

Min Buri (Suwinthawong) Section

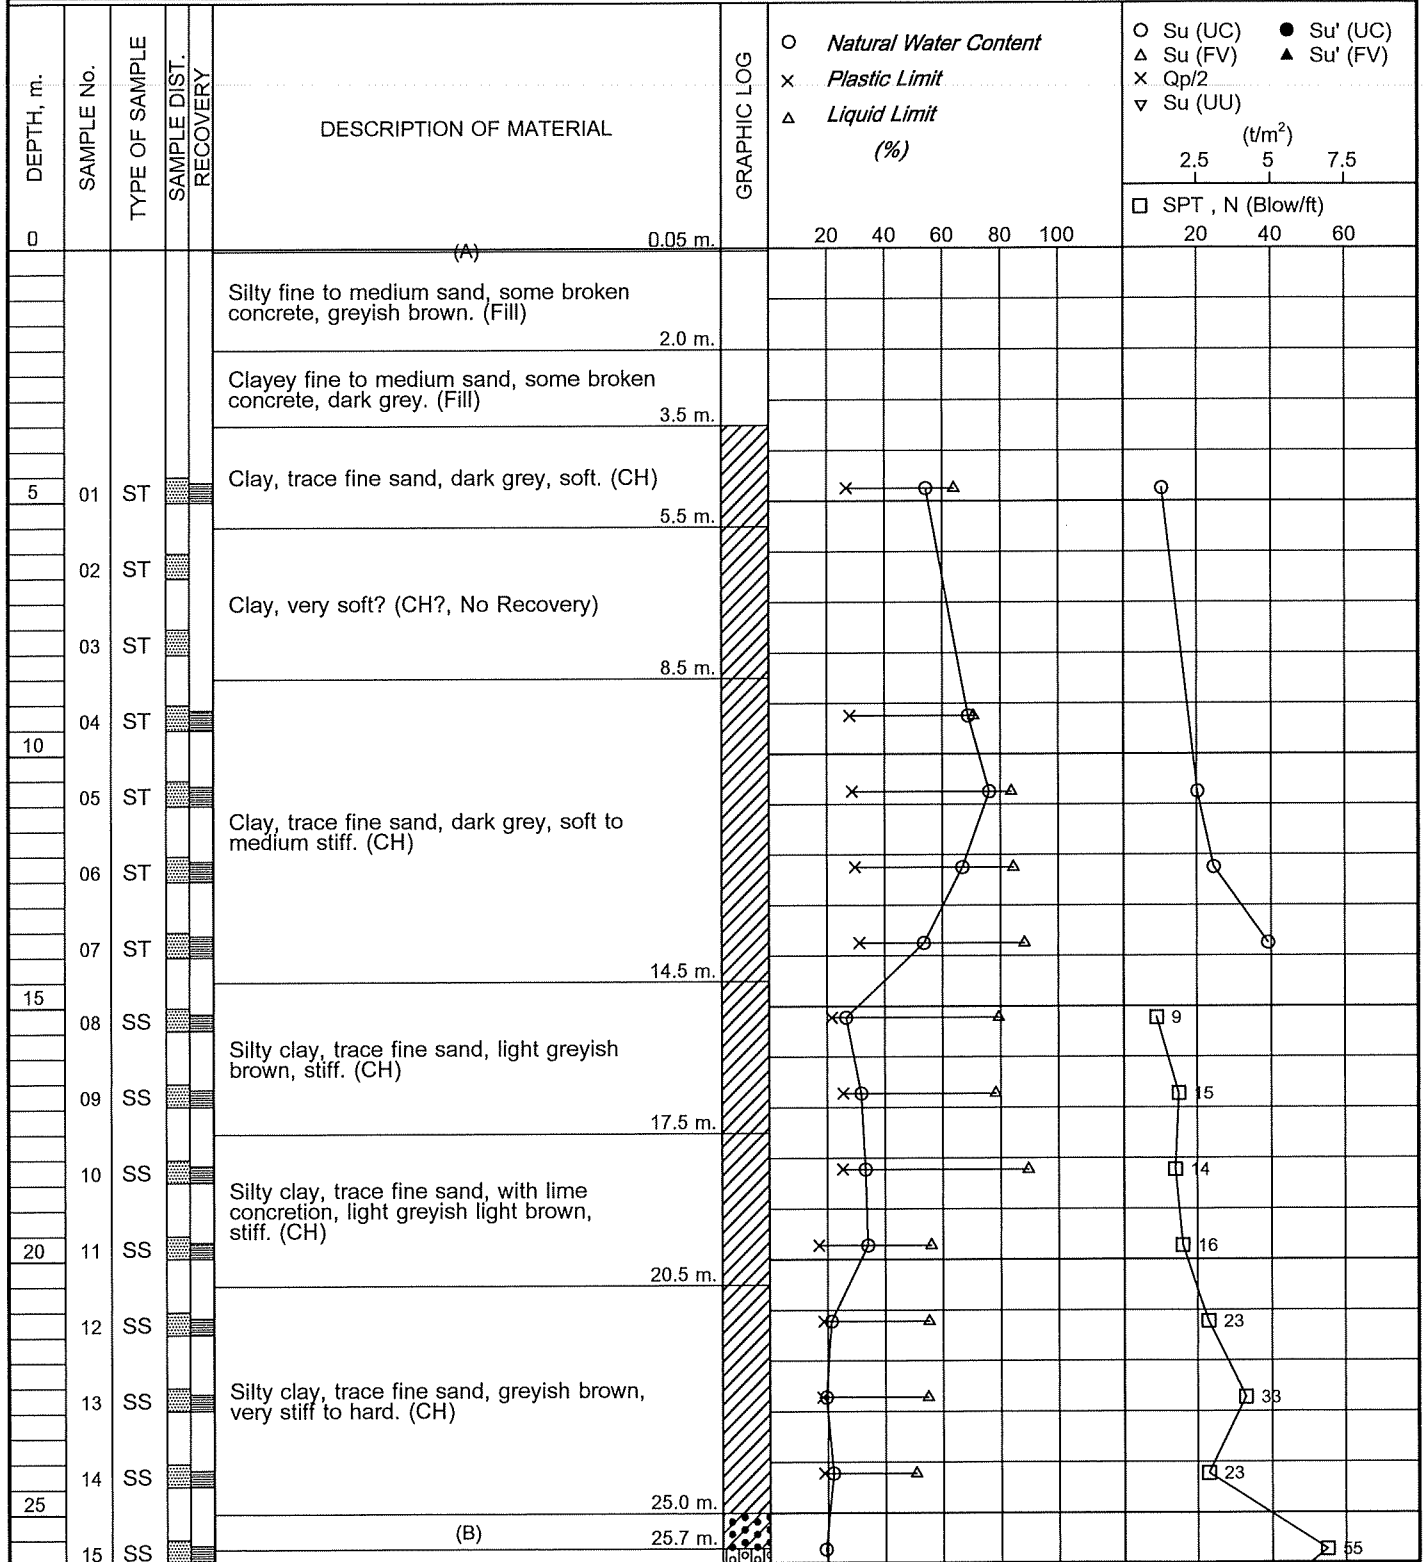

BORING STARTED : 27/03/25

RIG. ACKER

WL. -2.00 m

24 Hrs.  
After Boring

BORING FINISHED : 30/03/25

FOREMAN : WN.


JOB No. : 1167287

# LOG OF BORING No. OW-57

PROJECT : MRT Orange Line Project : Bang Khun Non -

LOCATION : Bangkok

Min Buri (Suwinthawong) Section

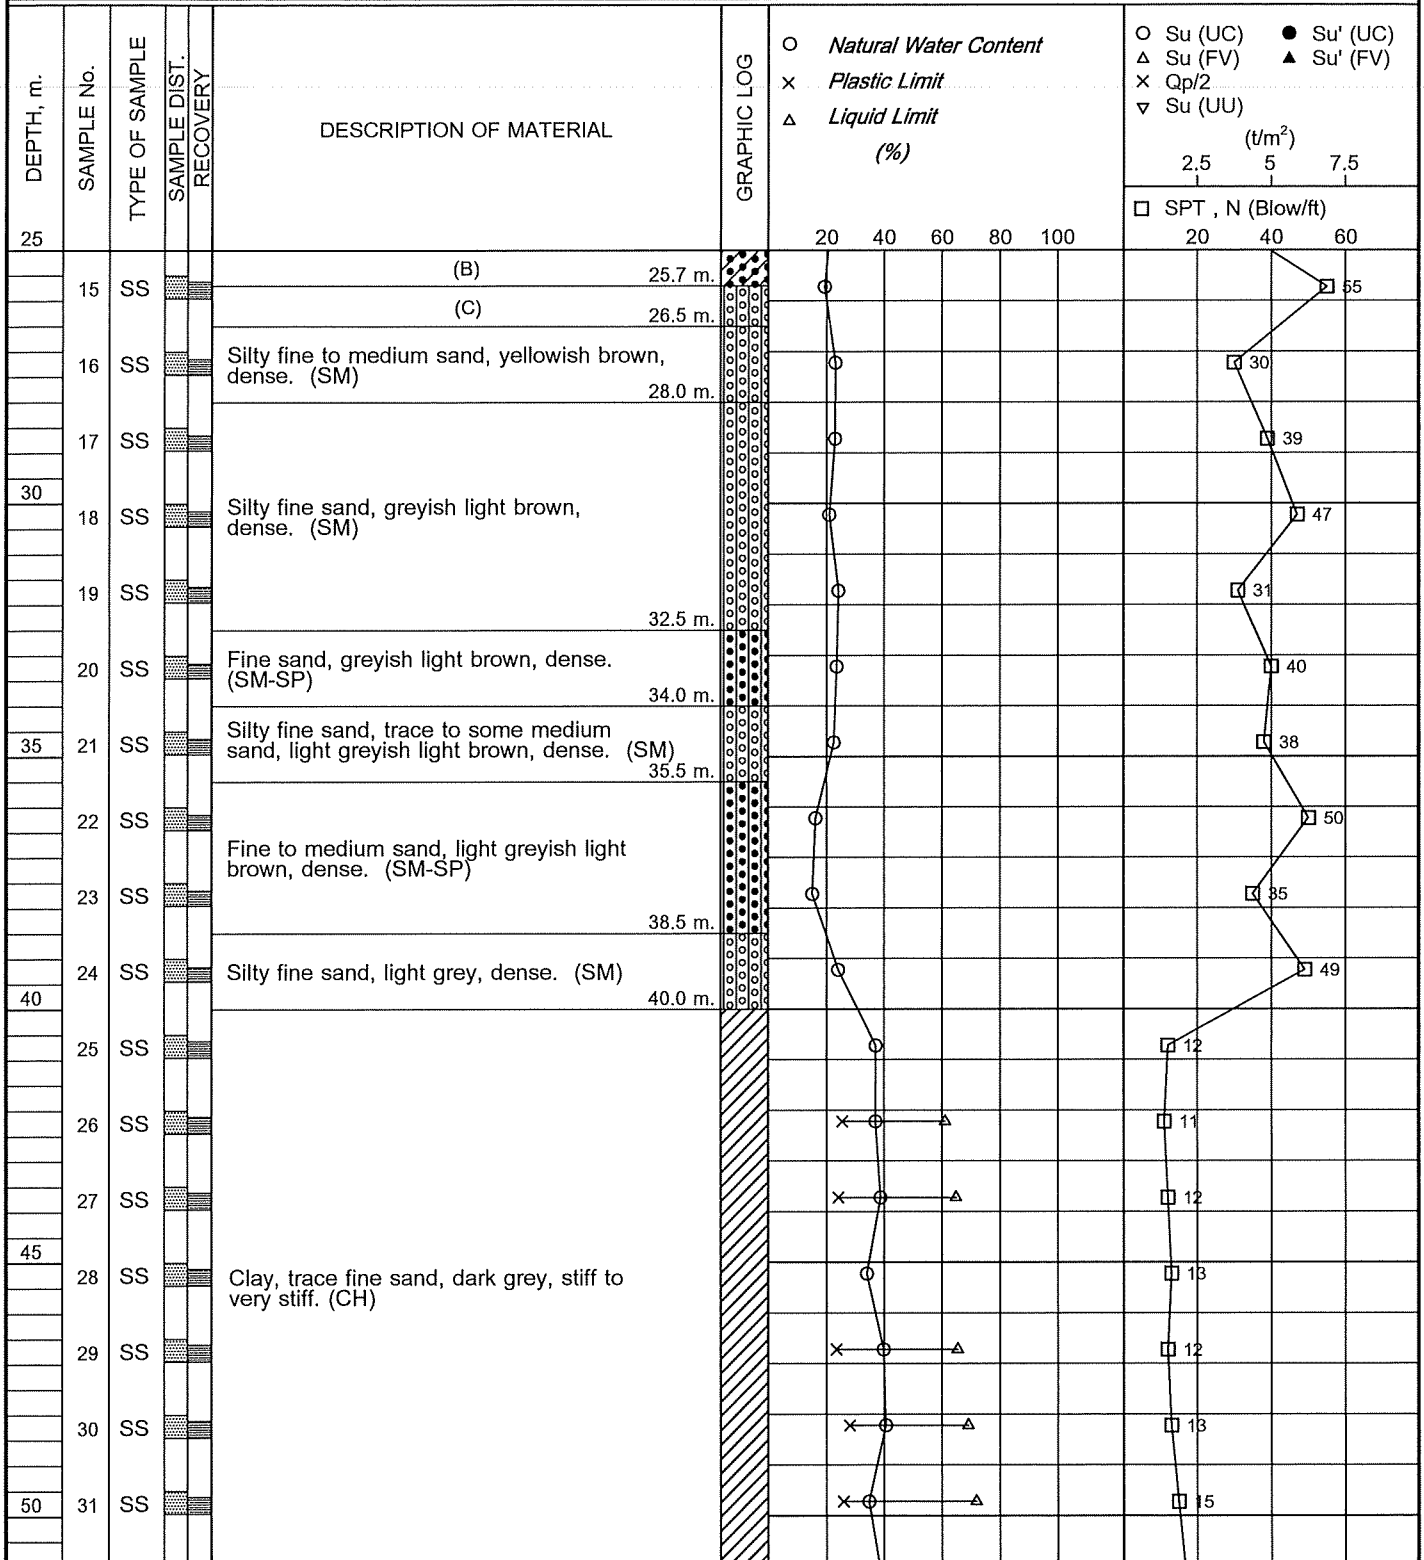

BORING STARTED : 27/03/25

RIG. ACKER

WL. -2.00 m

24 Hrs.  
After Boring

BORING FINISHED : 30/03/25

FOREMAN : WN.

JOB No. : 1167287

# LOG OF BORING No. OW-57

PROJECT : MRT Orange Line Project : Bang Khun Non -

LOCATION : Bangkok

Min Buri (Suwinthawong) Section

