


LOG OF BORING No. OW-63

PROJECT : MRT Orange Line Project : Bang Khun Non -

LOCATION : Bangkok

Min Buri (Suwinthawong) Section

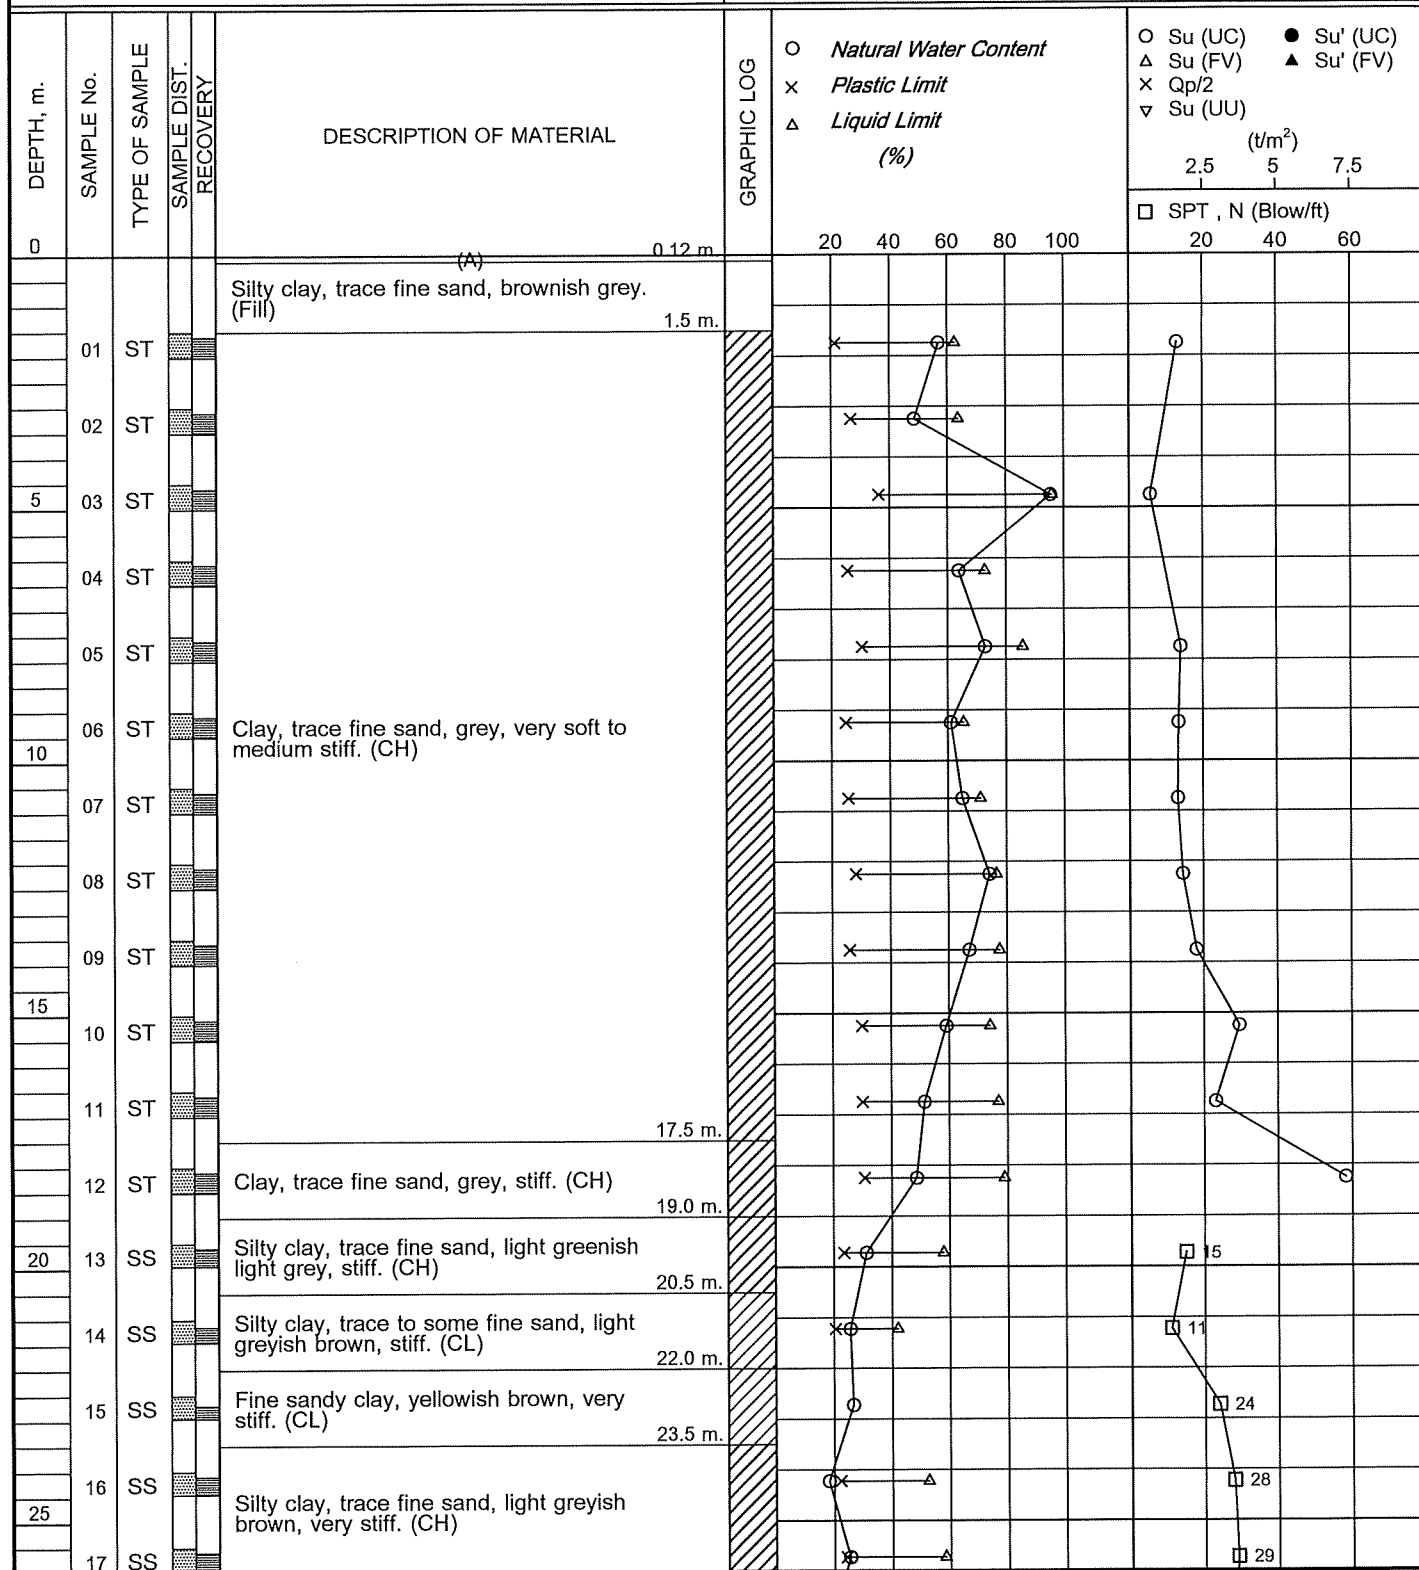

BORING STARTED : 14/01/25

RIG. ACKER

WL. -2.30 m 24 Hrs. After Boring

BORING FINISHED : 17/01/25

FOREMAN : RY.


JOB No. : 1167287

LOG OF BORING No. OW-63

PROJECT : MRT Orange Line Project : Bang Khun Non -

LOCATION : Bangkok

Min Buri (Suwinthawong) Section

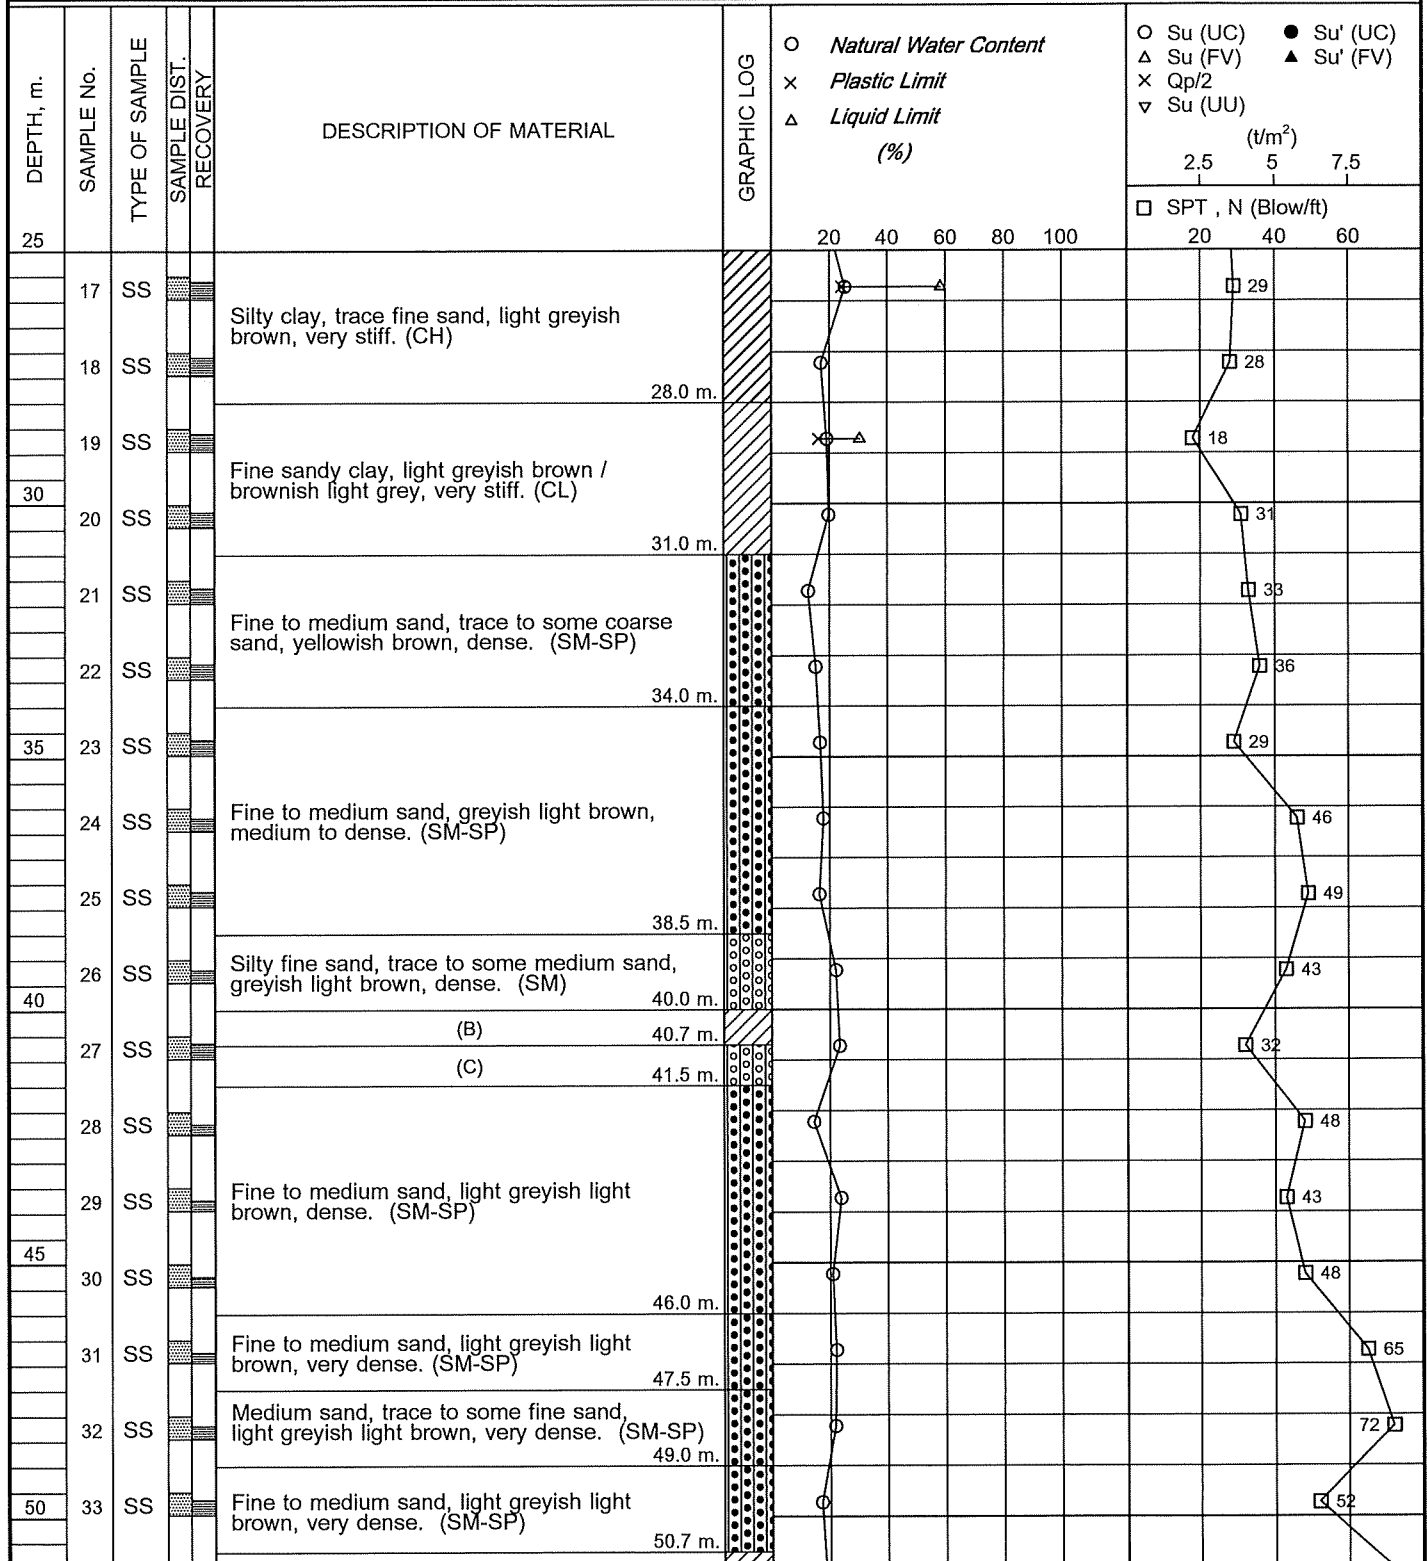

BORING STARTED : 14/01/25

RIG. ACKER

WL. -2.30 m

24 Hrs.
After Boring

BORING FINISHED : 17/01/25

FOREMAN : RY.


JOB No. : 1167287

LOG OF BORING No. OW-63

PROJECT : MRT Orange Line Project : Bang Khun Non -

LOCATION : Bangkok

Min Buri (Suwinthawong) Section

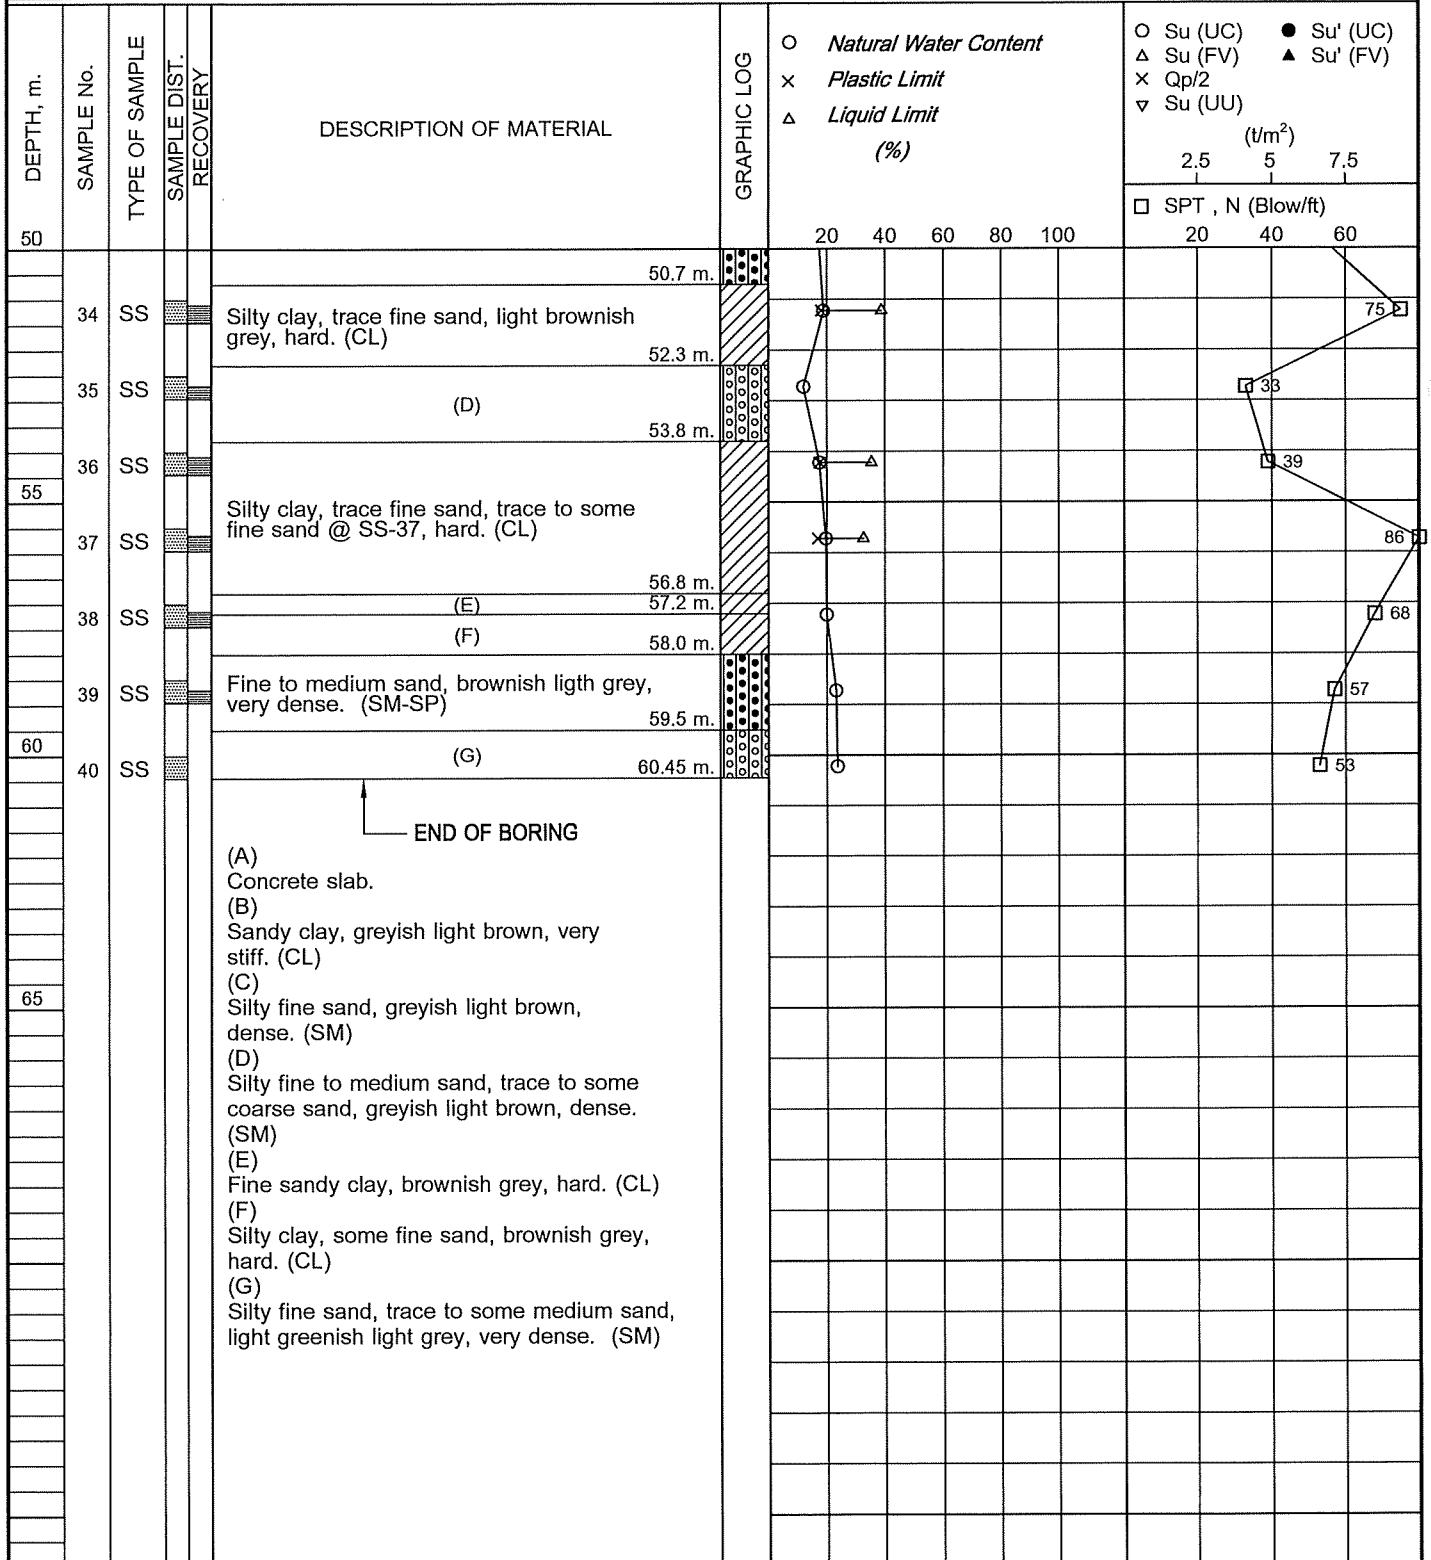

BORING STARTED : 14/01/25

RIG. ACKER

WL. -2.30 m 24 Hrs. After Boring

BORING FINISHED : 17/01/25

FOREMAN : RY.

JOB No. : 1167287